MAVJUD HOLAT (fotodagi chizma)

№	m²	№	m²
1	18,79	9	70,56
2	2,00	10	69,99
3	2,24	11	52,48
4	2,68	12	17,37
5	3,01	13	69,40
6	6,54	14	69,40
7	33,88	15	68,84
8	—		

Umumiy maydon 617 m², foydali 557,74 m². 8-xonaning raqami va maydoni fotoda ko'rinmaydi (hisob bo'yicha ≈ 70 m²).

O'ZGARISHLAR

O'zgarmaydi (buyurtmachi talabi): ZN1 va ZN2 zinalari, sanuzel bloki (2–6), 12-xona — ADM.
Buziladi: 7 va 11-xonalar orasidagi devor; 13–15-xonalarning koridor qismidagi devorlari; SR1–SR3 eshiklari uchun o'rta devorda teshik.
Quriladi: K1 koridorining janubiy devori (SR4–SR6 doskalari shu devorda), SR7 va K2 orasidagi devor, xonalar orasidagi bo'shliqlar yopiladi.

ISHLAR HAJMI (taxminiy)

Yangi devor, GKL 100	45,9 m · ≈ 138 m²
Buziladigan devor	10,9 m
Yangi eshik, 900 × 2100	7 ta

IZOH

Fotodagi chizmada: «Xonalar ichki qismi loyiha hujjatlarisiz qayta ta'mirlangan». Devorlarni buzish va qurishdan oldin ijaraga beruvchining yozma roziligi olinadi. O'lchamlar fotodan olingan — ish boshlanishidan oldin joyida o'lchanadi.

MASSHTAB 1:100

0 1 2 3 4 5 m

SHARTLI BELGILAR

- saqlanadigan devor
- yangi devor (GKL 100 / bo'shliqni yopish)
- yangi eshik (900)
- ustun
- buziladigan devor
- o'zgarmaydigan qism
- tashqi devor

PDP Academy · Xadra filiali

Chizma	**Mavjud holat va o'zgarishlar**		
Manba: mavjud holat chizmasi (foto), 2-qavat · umumiy 617 m², foydali 557,74 m²			
Toshkent sh., Xadra — 2-qavat			
Masshtab **1:100**	Sana **25.09.2026**	Versiya **v1.0**	Varaq **1 / 3**
Bajardi			
Tekshirdi / tasdiqladi — direktor			

MAYDON

Ichki gabarit	23 900 × 24 400
Umumiy maydon (hujjat)	617 m²
Foydali maydon (hujjat)	557,74 m²
O'quv xonalari, 7 ta · 164 o'rin	442,0 m²
Admin va sotuv (ADM, 12-xona)	17,6 m²
Koridorlar K1, K2 va zina oldi zali ZL	51,1 m²
Zinalar va sanuzel bloki (o'zgarmaydi)	45,8 m²
Toza balandlik	3000 mm (taxmin)

XONALAR

Xona	O'lcham, m	m²	O'rin	m²/kishi	Partalar
SR1	5.70 × 12.20	69,5	24	2,9	4 × 6 (2+2+2)
SR2	5.80 × 12.20	70,7	24	2,9	4 × 6 (2+2+2)
SR3	5.75 × 12.20	70,1	24	2,9	4 × 6 (2+2+2)
SR4	5.80 × 10.40	60,2	24	2,5	4 × 6 (2+2+2)
SR5	5.80 × 10.40	60,2	24	2,5	4 × 6 (2+2+2)
SR6	5.75 × 10.40	59,8	24	2,5	4 × 6 (2+2+2)
SR7	4.35 × 11.85	51,5	20	2,6	4 × 5 (2+3)
ADM	5.95 × 2.95	17,6	4	—	4 stol + 4 mijoz stuli
Jami		**442,0**	**164**		**6 × 24 + 1 × 20**

USTUNLAR — MAVJUD

Kod	O'q	X	Y	O'lcham
U1	2-B	6 050	6 300	400 × 400
U2	3-B	12 050	6 300	400 × 400
U3	4-B	18 050	6 300	400 × 400
U4	2-C	6 050	12 300	400 × 400
U5	3-C	12 050	12 300	400 × 400
U6	4-C	18 050	12 300	400 × 400
U7	2-D	6 050	18 450	400 × 400
U8	3-D	12 050	18 450	400 × 400 *
U9	4-D	18 050	18 450	400 × 400 *

Koordinata — ichki yuzaning yuqori-chap burchagidan, ustun markazi bo'yicha. O'qlar (taxminiy): 1…5 — 6 250 · 6 000 · 6 000 · 6 050; A…E — 6 500 · 6 000 · 6 150 · 6 150.

* U8, U9 fotoda ko'rinmaydi — to'r bo'yicha qo'yilgan, ular devor ichiga tushadi. Joyida tekshirilsin.

PARTA TO'RI (Beruniy standarti)

parta 690 × 500 · stul 380 × 420
qatorda 6 parta: 2 + 2 + 2 · guruhlar orasi 600 · blok eni 5 340
qator qadami 1 300 (parta 500 + o'tish 800) · 4 qator
doskadan 1-partagacha 2 440 · oxirgi parta 6 840 · sig'im 24
ustundan: oldi/orqa 500 · yon 0
ISTISNO: SR7 — qatorda 5 parta (2 + 3), 4 qator, sig'im 20; yon chekka 150
Doska 3000 (SR7 — 2400) kar devorda; eshiklar 900, ichkariga ochiladi, doska yonida.
K1, K2 koridorlari 1500. Yangi devorlar — GKL 100, ovoz izolyatsiyali.
ADM (12-xona) va zinalar mavjud holicha; 1-qavatda zina oldida resepshn va turniket.

MASSHTAB 1:100

0 1 2 3 4 5 m

SHARTLI BELGILAR

- kesilgan ichki devor
- mavjud ustun 400 × 400
- deraza (joyi taxminiy)
- stul 380 × 420
- o'qituvchi / xodim stoli
- kesilgan tashqi devor
- taxminiy ustun (fotoda yo'q)
- parta 690 × 500
- doska (kar devorda)

PDP Academy · Xadra filiali

Chizma: **Jihozlash rejasi**

Manba: mavjud holat chizmasi (foto), 2-qavat · umumiy 617 m², foydali 557,74 m²

Toshkent sh., Xadra — 2-qavat

Masshtab	Sana	Versiya	Varaq
1:100	25.09.2026	v1.0	2 / 3

Bajardi _____

Tekshirdi / tasdiqladi — direktor _____

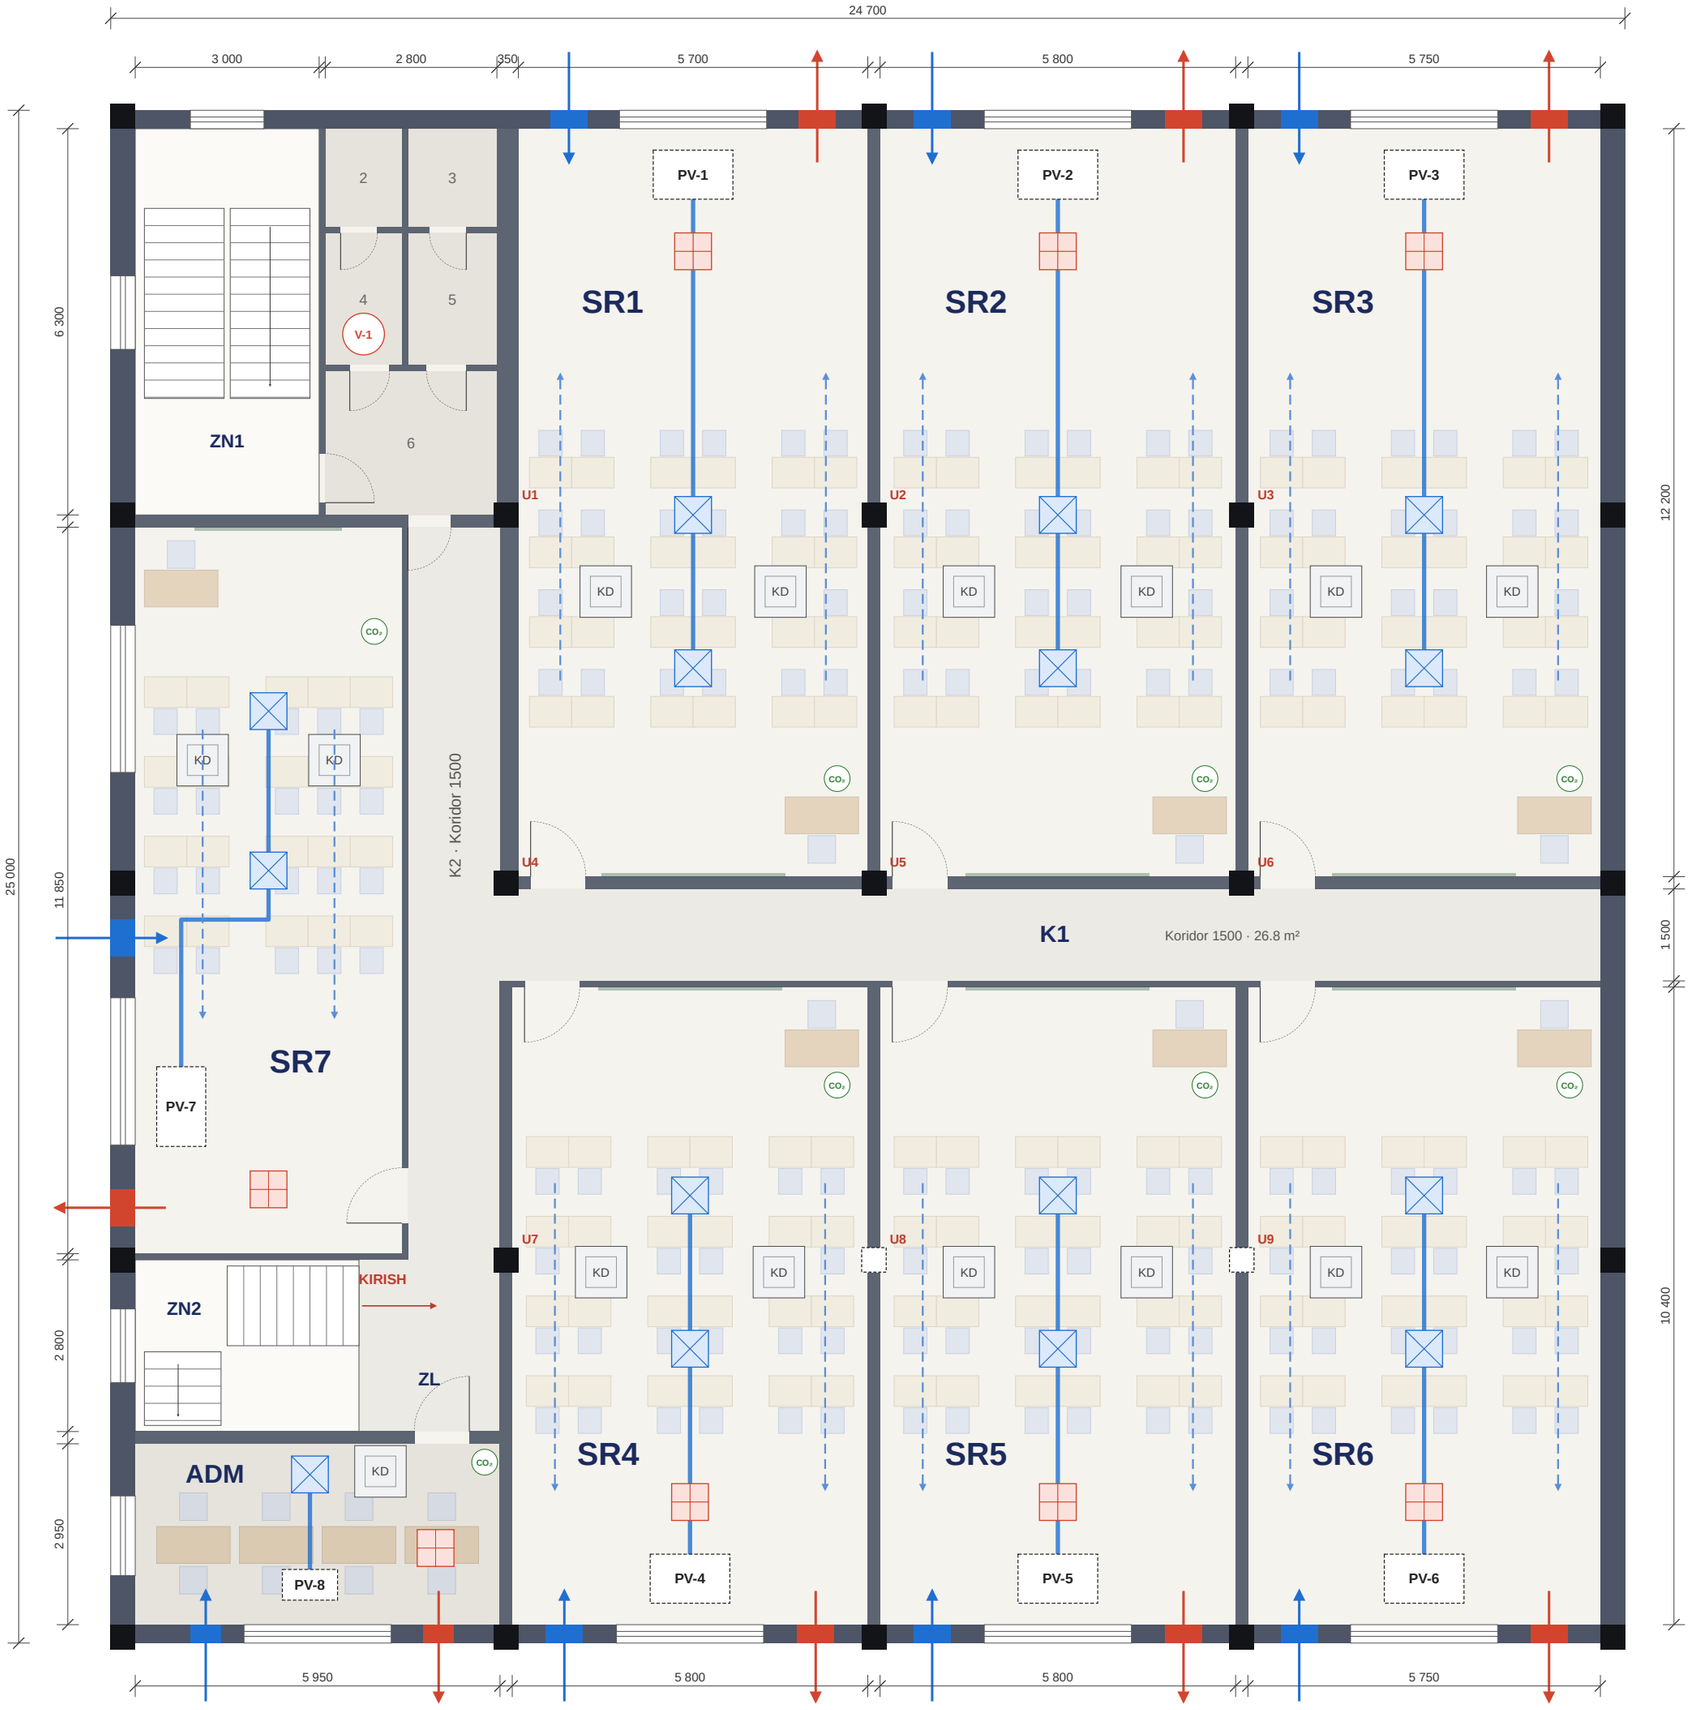

HAVO ALMASHINUVI — XONALAR BO'YICHA

Xona	Odam	Havo, m³/soat	Hajm, m³	Marta / soat	Sovutish, kVt	Qurilma
SR1	25	750	208	3,6	8,0	PV-1
SR2	25	750	212	3,5	8,0	PV-2
SR3	25	750	210	3,6	8,0	PV-3
SR4	25	750	181	4,2	8,0	PV-4
SR5	25	750	181	4,2	8,0	PV-5
SR6	25	750	179	4,2	8,0	PV-6
SR7	21	630	155	4,1	7,5	PV-7
ADM	6	180	53	3,4	3,0	PV-8
Jami		**5 310**			**58,5**	

HISOB ASOSI

30 m³/soat har bir kishiga (o'quvchilar + o'qituvchi). Bir kishi soatiga ~18 l CO_2 chiqaradi: 18 l ÷ (1000 − 420) ppm ≈ 31 m³/soat — xonada CO_2 1000 ppm dan oshmaydi.
Hajm — toza balandlik 3000 mm (taxmin) bo'yicha. Sovutish — odamlar, noutbuklar, proyektor, yoritish, derazadan quyosh va toza havo (rekuperator FIK 60%) yig'indisi, Toshkent yozi (+40 °C) uchun dastlabki baho.

YECHIM

Nega faqat deraza yetmaydi: SR1–SR6 chuqurligi 10,4–12,2 m, deraza faqat orqadagi qisqa devorda. Bir tomonlama tabiiy shamollatish ~2,5 × H ≈ 7,5 m gacha yetadi — doska tomondagi 3–5 m havosiz qoladi. Qish va yozda derazalar yopiq bo'ladi.
Har sinfga alohida PV qurilma (rekuperatorli, ~750 m³/soat, shovqin ≤ 35 dB(A)): deraza devori yonida shift ichida, havo fasad panjarasidan olinadi va chiqariladi. Toza havo doska tomonga beriladi, orqa tomondan so'riladi — oqim o'quvchilar ustidan o'tadi. CO_2 datchigi bilan boshqariladi; bo'sh xona o'chadi.
Konditsioner: har sinfga 2 ta KD (kasseta yoki kanalli), tashqi bloklar fasadda yoki tomda.
SR7: derazalar uzun (chap) devorda, xona eni 4,35 m — tabiiy shamollatish yaxshi ishlaydi; PV-7 yopiq deraza mavsumi uchun.
V-1: sanuzel chiqarish ventilyatsiyasi 4 × 50 = 200 m³/soat — mavjud shaxtani tekshirish. Koridorlar sanuzel orqali so'riladigan havo bilan shamollatiladi; tutun chiqarish talabini yong'in xavfsizligi mutaxassisi belgilaydi.

MASSHTAB 1:100

0 1 2 3 4 5 m

SHARTLI BELGILAR

- PV — rekuperatorli kiritish-chiqarish qurilmasi (shift ichida)
- toza havo diffuzori
- fasad panjarasi: toza havo kirishi
- KD — konditsioner ichki bloki
- CO_2 datchigi
- toza havo kanali
- so'rish panjarasi
- fasad panjarasi: iflos havo chiqishi
- xonadagi havo oqimi

PDP Academy · Xadra filiali			
Chizma	**Havo almashinuvi sxemasi**		
Manba: mavjud holat chizmasi (foto), 2-qavat · umumiy 617 m², foydali 557,74 m²			
Toshkent sh., Xadra — 2-qavat			
Masshtab **1:100**	Sana **25.09.2026**	Versiya **v1.0**	Varaq **3 / 3**
Bajardi			
Tekshirdi / tasdiqladi — direktor			