## 1-varaq · Devorlar va eshiklar rejasi (butun qavat), 1:100




## DEVORLAR VA ESHIKLAR — UMUMIY REJA

- mavjud devor / ustun (saqlanadi)
- yangi shisha devor (S…)
- yangi shisha eshik (E…), yoy — ochilishi
- zina panjarasi (P1), metall
- yangi GKL devor, 100 mm
- buziladigan devor
- ustun — joyida tekshiriladi

### Xonalar: ichki o'lchamlari (devor yuzidan devor yuzigacha)

| Xona | Eni × chuqurligi, mm | Maydon, m² |
|---|---|---|
| 1-xona | 5 700 × 7 700 | 43.9 |
| 2-xona | 5 800 × 7 700 | 44.6 |
| 3-xona | 5 750 × 7 700 | 44.2 |
| 4-xona | 5 750 × 5 600 | 32.2 |
| 5-xona | 5 750 × 7 700 | 44.2 |
| 6-xona | 5 800 × 7 700 | 44.6 |
| 7-xona | 5 800 × 7 700 | 44.6 |
| XZ1 · sotuv | 5 700 × 2 600 | 14.8 |
| XZ2 · admin | 5 800 × 2 600 | 15.1 |
| XZ3 · ustozlar | 5 800 × 2 800 | 16.2 |
| XZ4 · call-markaz | 5 700 × 2 800 | 16.0 |
| Koworking | 5 950 × 11 850 | 70.5 |
| CEO | 5 950 × 2 950 | 17.6 |
| KL1 · kladovka | 2 800 × 1 500 | 4.2 |
| KL2 · kladovka | 2 800 × 1 500 | 4.2 |
| Kirish zali | 2 300 × 2 900 | 6.6 |

### Devor turlari

- **GKL 100:** metall profil 75 mm (stoyka qadami 600), ikki tomonida 12.5 mm gipsokarton; ichida 50 mm mineral paxta (shovqin uchun, tavsiya); poldan shiftgacha 3 500 mm.
- **Shisha devor:** poldan 2 500 mm gacha shisha (laminatlangan, kamida 2 × 6 mm yoki 10 mm toblangan), alyumin profilda; 2 500–3 500 mm — GKL (shisha ustida). 1 000–1 600 mm da matli plyonka.
- **Eshiklar (founder, 16.10):** shisha, 1 000 × 2 100 mm, **yonga suriladigan** (Damas eshigi kabi): barg xona ichida, yuqori relsda devor bo'ylab suriladi, ochilganda yonidagi shisha oldida turadi; ustida 400 mm qo'zg'almas shisha. Kladovka eshiklari — 800 × 2 100, ichkariga ochiladi. Jadvali — 2-varaqda.
- **Bo'shliqlarni yopish** (eski eshik va o'tish joylari, 1-varaqdagi to'q sariq bo'laklar) — GKL, mavjud devor qalinligida (200–300 mm), ikki tomoni tekislanadi.
- **4-xona doska devori (17.10):** g'arbiy mavjud devorga GKL qoplama 100 mm (profil 75 + 12.5 mm ikki qatlam), U6 ustuni yuzi bilan tekis — interaktiv doska va bambuk panel shu yuzaga; doska eshik tomonida.


**Buyurtmachi va founder (16.10):** K1 va K2 koridorlari 4-xona orqali uning o'rtasigacha (x 21 000) davom etadi; oxirida ko'ndalang GKL devor va eshik — orqasi **kladovka** (KL1, KL2), ustida kanalli konditsioner. 3-, 4-, 5-xonaning koridor tomoni kladovkagacha shisha; 4-xona kichrayadi (5.75 × 5.6 m). Barcha 11 eshik — 1 m, suriladigan.
**Buyurtmachi qarorlari (14.10):** (1) xizmat xonalari zonasidagi **eski o'rta devor (C o'qi) buzilmaydi** — 2 × 2 xona: K2 tomonda XZ1 sotuv va XZ2 admin (yonma-yon; XZ2 eshigi o'rtada, XZ1 niki — g'arbiy chetda, 18.10), K1 tomonda XZ4 call-markaz va XZ3 ustozlar; koridor tomoni shisha. (2) **Kirishdagi ZN2 zinasi bilan koworking orasidagi devor buziladi** — o'rniga zina tuynugi chetida metall panjara P1 (h 1 100, uzunligi 3 650).

### Ishni boshlashdan oldin joyida tekshiriladi

- Barcha o'lchamlar mavjud chizma fotosidan olingan: ish boshlashdan oldin ustunlar (U1–U9) va mavjud devorlar yuzasi o'lchab chiqiladi; farq 30 mm dan katta bo'lsa — loyihachiga xabar beriladi.
- U8, U9 ustunlari fotoda ko'rinmaydi — U7 bilan bir chiziqda deb olingan (punktir).
- Shisha devorlar GKL karkas va eshik o'rinlari belgilangandan keyin **joyida o'lchanib** buyurtma qilinadi (jadvaldagi o'lchamlar — loyiha bo'yicha).
- Poldan shiftgacha 3 500 mm (buyurtmachi); to'sinlar bo'lsa, GKL va shisha ustidagi qism moslanadi.
- ZN2 devorini buzishdan oldin: devor yuk ko'taruvchi emasligi va zinapoya to'sig'i bo'yicha yong'in xavfsizligi talabi tekshiriladi (ijaraga beruvchi va yong'in nazorati bilan kelishiladi). Panjara: balandligi 1 100 mm, tik ustunchalar orasi ≤ 110 mm (bolalar uchun xavfsiz).

**PDP Academy · Xadra filiali**

| | |
|---|---|
| Chizma | **Devorlar va eshiklar rejasi (o'lchamli)** |
| Ish chizmasi — ustalar uchun. Toshkent sh., Xadra — 2-qavat | |
| Masshtab 1:100 | Sana 14.10.2026 |
| Versiya v1.2 | Varaq 1 / 2 |
| Bajardi: _____ | Tekshirdi: _____ |

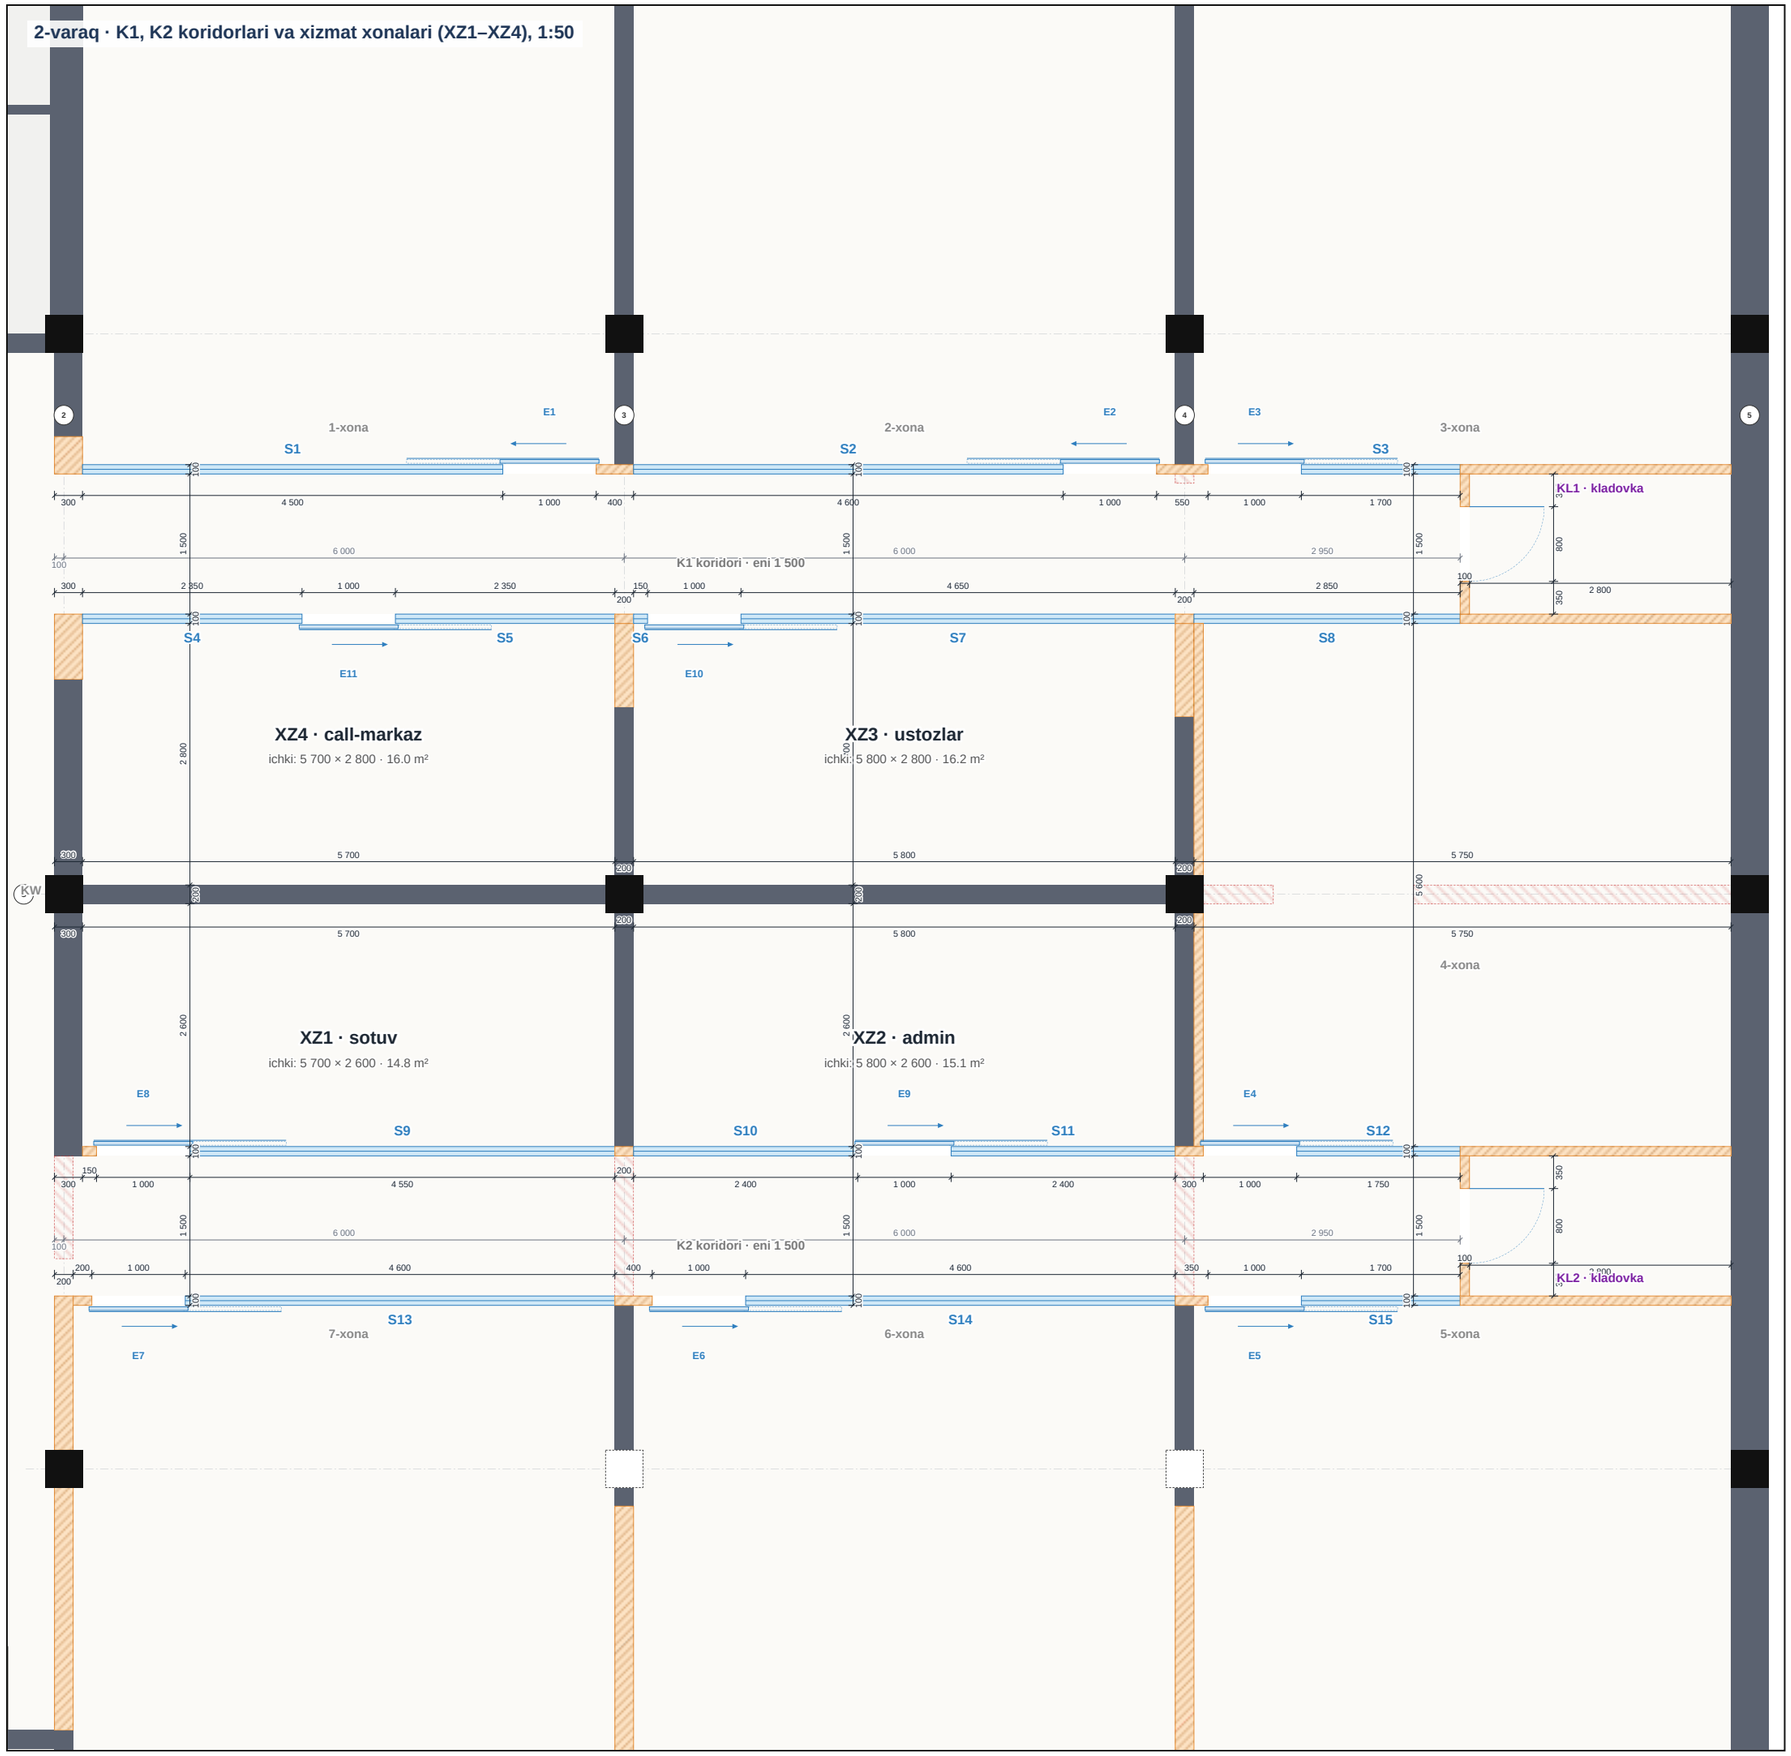


## SHISHA DEVORLAR, ESHIKLAR VA GKL — JADVALLAR

### Eshiklar (yangi) — 13 ta: 11 ta shisha suriladigan (1 m, barg xona ichida) va 2 ta kladovka eshigi


| Kod | Xona | Joyi | x, mm | O'lchami | Turi (koridordan qaraganda) |
|---|---|---|---|---|---|
| **E1** | 1-xona | K1 shimoliy devori | 10 750–11 750 | 1 000 × 2 100 | suriladi chapga |
| **E2** | 2-xona | K1 shimoliy devori | 16 750–17 750 | 1 000 × 2 100 | suriladi chapga |
| **E3** | 3-xona | K1 shimoliy devori | 18 300–19 300 | 1 000 × 2 100 | suriladi o'ngga |
| **E4** | 4-xona | K2 shimoliy devori | 18 250–19 250 | 1 000 × 2 100 | suriladi o'ngga |
| **E5** | 5-xona | K2 janubiy devori | 18 300–19 300 | 1 000 × 2 100 | suriladi chapga |
| **E6** | 6-xona | K2 janubiy devori | 12 350–13 350 | 1 000 × 2 100 | suriladi chapga |
| **E7** | 7-xona | K2 janubiy devori | 6 350–7 350 | 1 000 × 2 100 | suriladi chapga |
| **E8** | XZ1 · sotuv | K2 shimoliy devori | 6 400–7 400 | 1 000 × 2 100 | suriladi o'ngga |
| **E9** | XZ2 · admin | K2 shimoliy devori | 14 550–15 550 | 1 000 × 2 100 | suriladi o'ngga |
| **E10** | XZ3 · ustozlar | K1 janubiy devori | 12 300–13 300 | 1 000 × 2 100 | suriladi chapga |
| **E11** | XZ4 · call-markaz | K1 janubiy devori | 8 600–9 600 | 1 000 × 2 100 | suriladi chapga |
| **E12** | KL1 · kladovka | K1 oxiri (x 21 000) | 8 150–8 950 | 800 × 2 100 | ochiladi, ichkariga |
| **E13** | KL2 · kladovka | K2 oxiri (x 21 000) | 15 450–16 250 | 800 × 2 100 | ochiladi, ichkariga |

### Shisha devorlar (S) — balandligi 2 500 mm

| Kod | Joyi | x, mm | Uzunligi | m² |
|---|---|---|---|---|
| **S1** | K1 shimoliy devori | 6 250–10 750 | 4 500 | 11.25 |
| **S2** | K1 shimoliy devori | 12 150–16 750 | 4 600 | 11.50 |
| **S3** | K1 shimoliy devori | 19 300–21 000 | 1 700 | 4.25 |
| **S4** | K1 janubiy devori | 6 250–8 600 | 2 350 | 5.88 |
| **S5** | K1 janubiy devori | 9 600–11 950 | 2 350 | 5.88 |
| **S6** | K1 janubiy devori | 12 150–12 300 | 150 | 0.38 |
| **S7** | K1 janubiy devori | 13 300–17 950 | 4 650 | 11.63 |
| **S8** | K1 janubiy devori | 18 150–21 000 | 2 850 | 7.13 |
| **S9** | K2 shimoliy devori | 7 400–11 950 | 4 550 | 11.38 |
| **S10** | K2 shimoliy devori | 12 150–14 550 | 2 400 | 6.00 |
| **S11** | K2 shimoliy devori | 15 550–17 950 | 2 400 | 6.00 |
| **S12** | K2 shimoliy devori | 19 250–21 000 | 1 750 | 4.38 |
| **S13** | K2 janubiy devori | 7 350–11 950 | 4 600 | 11.50 |
| **S14** | K2 janubiy devori | 13 350–17 950 | 4 600 | 11.50 |
| **S15** | K2 janubiy devori | 19 300–21 000 | 1 700 | 4.25 |
| | **Jami (eshiklarsiz)** | | **45 150** | **112.9** |

Yangi GKL bo'laklari (to'q sariq) — eshik va ustunlar yonida; o'lchamlari zanjirlarda. Bo'shliqlarni yopish — 1-varaqda.

### Shisha devor — tipik yoyilma (koridordan ko'rinish)

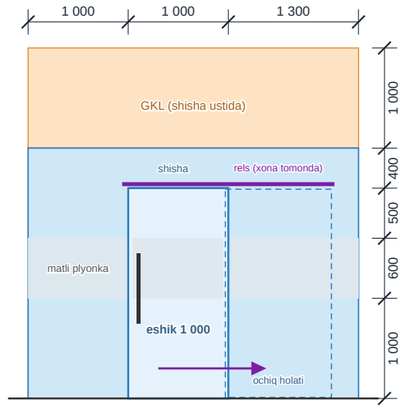


- Zanjirlar koridor ichida, koworking devori yuzasidan (x = 5 950) boshlanadi; o'qlar 2, 3, 4 — ustunlar markazi.
- XZ xonalari ichki eni 5 700 (XZ1, XZ2) va 5 800 (XZ3, XZ4); chuqurligi K1 tomonda 2 600, K2 tomonda 2 600 (o'rta devor 200 mm).

| | | | |
|---|---|---|---|
| **PDP Academy · Xadra filiali** | | | |
| Chizma | **Koridorlar va xizmat xonalari — shisha, eshiklar** | | |
| Ish chizmasi — ustalar uchun. Toshkent sh., Xadra — 2-qavat | | | |
| Masshtab 1:50 | Sana 14.10.2026 | Versiya v1.2 | Varaq 2 / 2 |
| Bajardi: _____ | Tekshirdi: _____ | | |