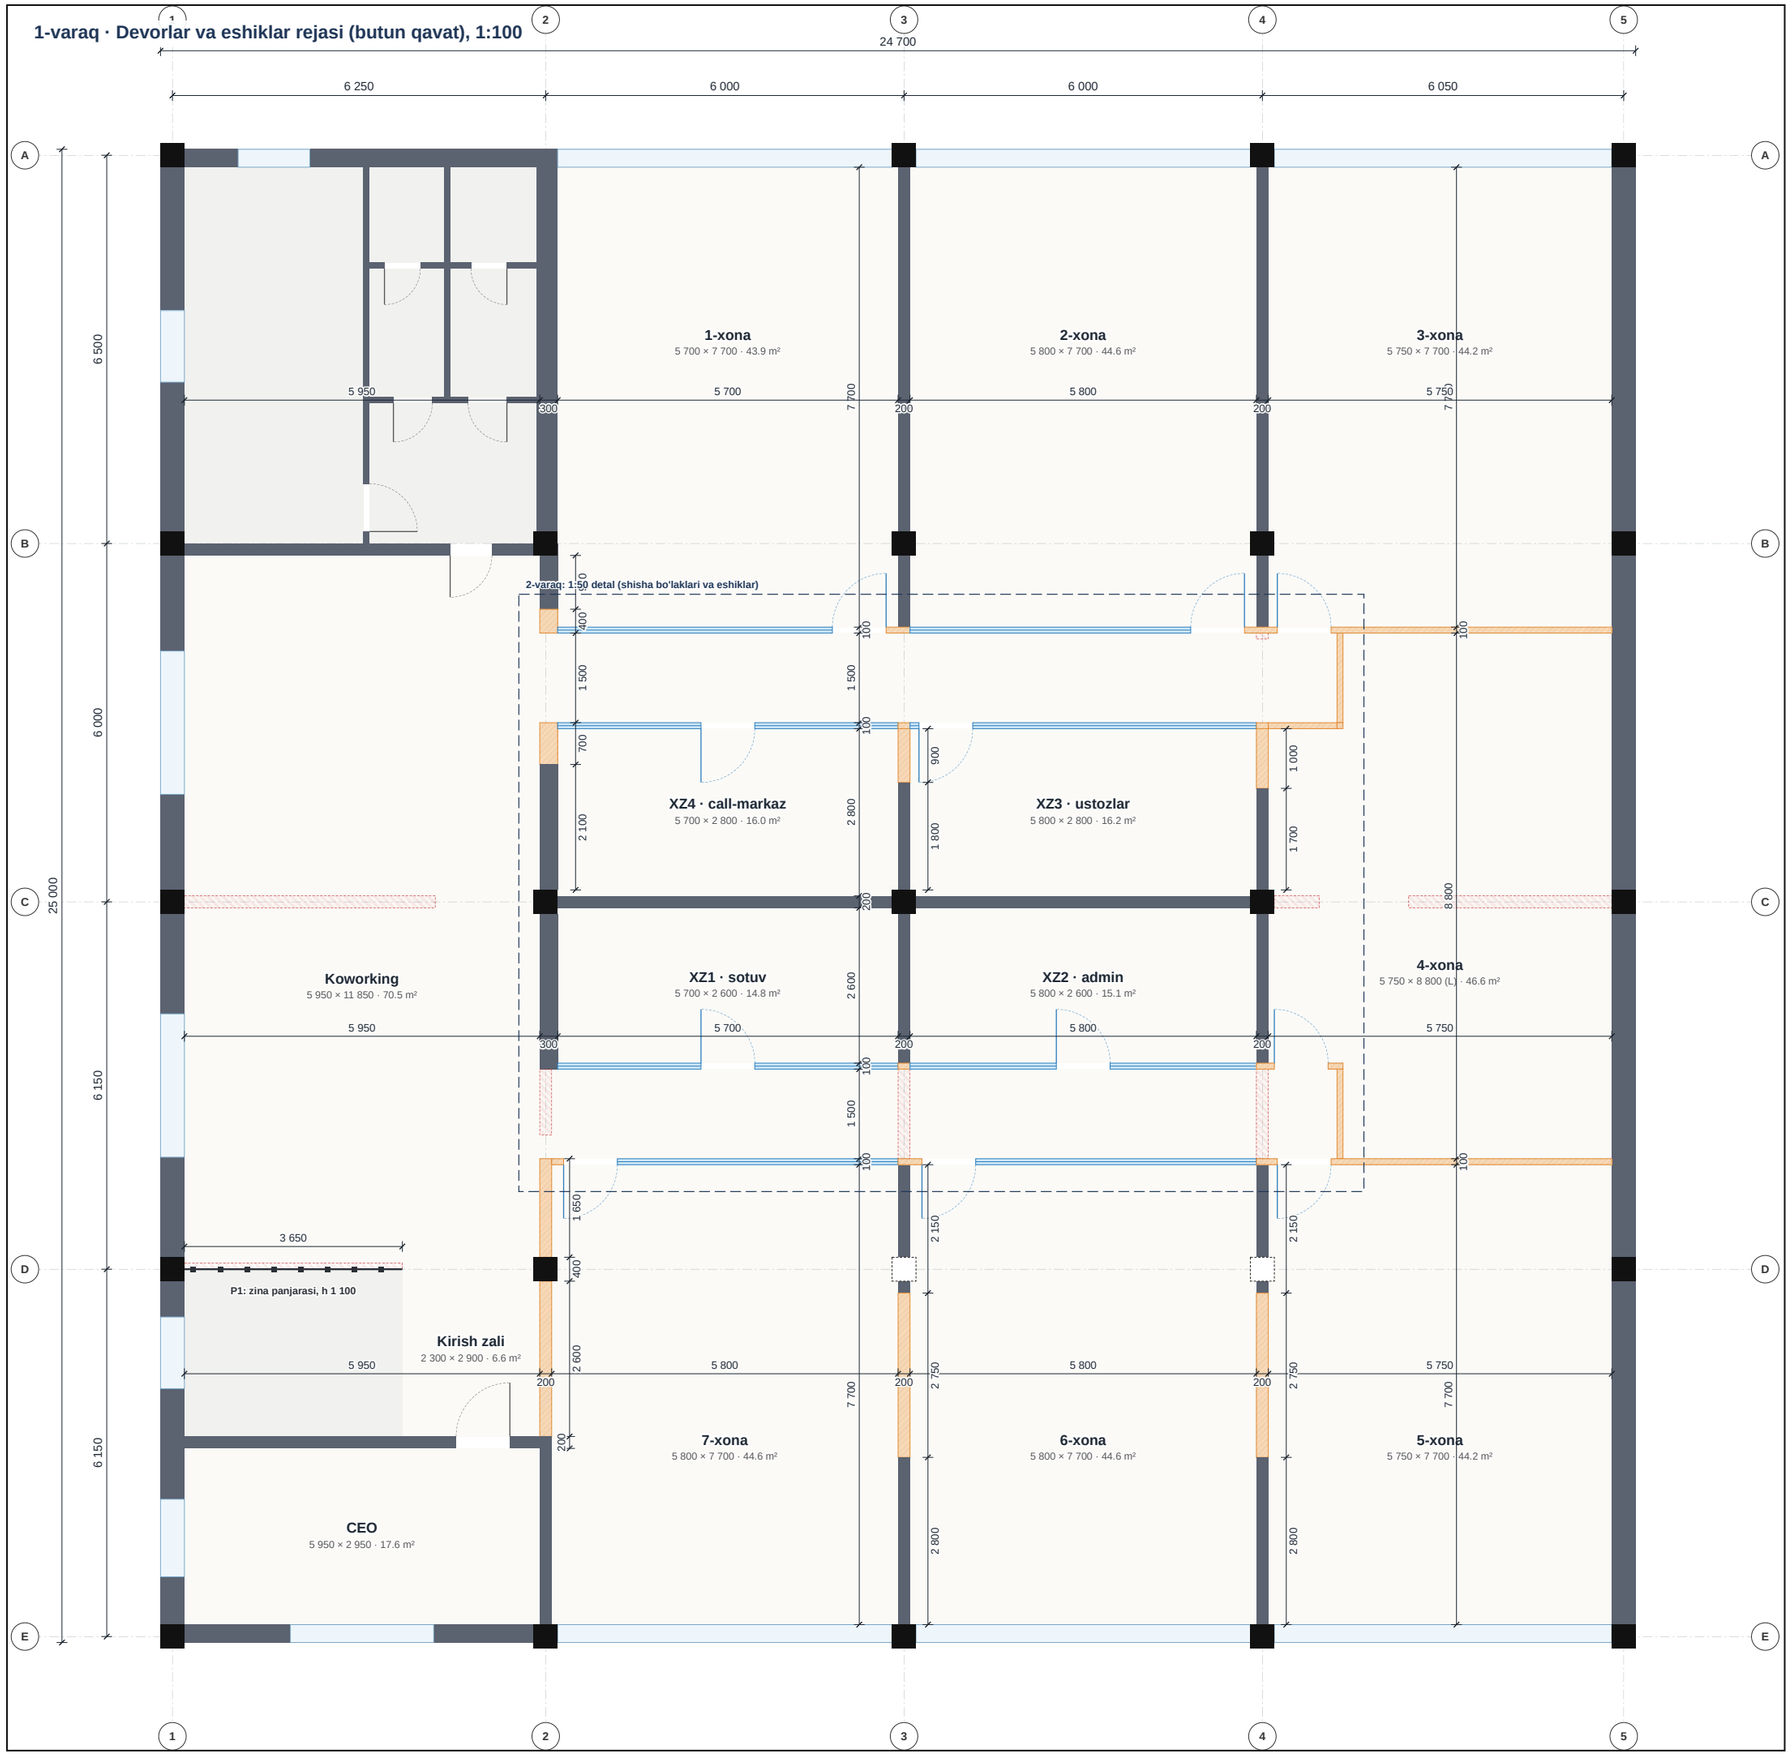


DEVORLAR VA ESHIKLAR — UMUMIY REJA

- mavjud devor / ustun (saqlanadi)
- yangi shisha devor (S…)
- yangi shisha eshik (E…), yoy — ochilishi
- zina panjarasi (P1), metall
- yangi GKL devor, 100 mm
- buziladigan devor
- ustun — joyida tekshiriladi

Xonalar: ichki o'lchamlari (devor yuzidan devor yuzigacha)

Xona	Eni × chuqurligi, mm	Maydon, m²
1-xona	5 700 × 7 700	43.9
2-xona	5 800 × 7 700	44.6
3-xona	5 750 × 7 700	44.2
4-xona	5 750 × 8 800 (L shakl)	46.6
5-xona	5 750 × 7 700	44.2
6-xona	5 800 × 7 700	44.6
7-xona	5 800 × 7 700	44.6
XZ1 · sotuv	5 700 × 2 600	14.8
XZ2 · admin	5 800 × 2 600	15.1
XZ3 · ustozlar	5 800 × 2 800	16.2
XZ4 · call-markaz	5 700 × 2 800	16.0
Koworking	5 950 × 11 850	70.5
CEO	5 950 × 2 950	17.6
Kirish zali	2 300 × 2 900	6.6

Devor turlari


- **GKL 100:** metall profil 75 mm (stoyka qadami 600), ikki tomonida 12.5 mm gipsokarton; ichida 50 mm mineral paxta (shovqin uchun, tavsiya); poldan shiftgacha 3 500 mm.
- **Shisha devor:** poldan 2 500 mm gacha shisha (laminatlangan, kamida 2 × 6 mm yoki 10 mm toblangan), alyumin profilda; 2 500–3 500 mm — GKL (shisha ustida). 1 000–1 600 mm da matli plyonka.
- **Eshiklar:** shisha, 900 × 2 100 mm, ustida 400 mm qo'zg'almas shisha; hammasi xona ichiga ochiladi. Jadvali — 2-varaqda.
- **Bo'shliqlarni yopish** (eski eshik va o'tish joylari, 1-varaqdagi to'q sariq bo'laklar) — GKL, mavjud devor qalinligida (200–300 mm), ikki tomoni tekislanadi.

Buyurtmachi qarorlari (14.10): (1) xizmat xonalari zonasidagi **eski o'rta devor (C o'qi) buzilmaydi** — 2 × 2 xona: K2 tomonda XZ1 sotuv va XZ2 admin (yonma-yon, eshiklari o'rtada), K1 tomonda XZ4 call-markaz va XZ3 ustozlar; koridor tomoni shisha. (2) **Kirishdagi ZN2 zinasi bilan koworking orasidagi devor buziladi** — o'rniga zina tuynugi chetida metall panjara P1 (h 1 100, uzunligi 3 650).

Ishni boshlashdan oldin joyida tekshiriladi

- Barcha o'lchamlar mavjud chizma fotosidan olingan: ish boshlashdan oldin ustunlar (U1–U9) va mavjud devorlar yuzasi o'lchab chiqiladi; farq 30 mm dan katta bo'lsa — loyihachiga xabar beriladi.
- U8, U9 ustunlari fotoda ko'rinmaydi — U7 bilan bir chiziqda deb olingan (punktir).
- Shisha devorlar GKL karkas va eshik o'rinlari belgilangandan keyin **joyida o'lchanib** buyurtma qilinadi (jadvaldagi o'lchamlar — loyiha bo'yicha).
- Poldan shiftgacha 3 500 mm (buyurtmachi); to'sinlar bo'lsa, GKL va shisha ustidagi qism moslanadi.
- ZN2 devorini buzishdan oldin: devor yuk ko'taruvchi emasligi va zinapoya to'sig'i bo'yicha yong'in xavfsizligi talabi tekshiriladi (ijaraga beruvchi va yong'in nazorati bilan kelishiladi). Panjara: balandligi 1 100 mm, tik ustunchalar orasi ≤ 110 mm (bolalar uchun xavfsiz).

PDP Academy · Xadra filiali			
Chizma	**Devorlar va eshiklar rejasi (o'lchamli)**		
Ish chizmasi — ustalar uchun. Toshkent sh., Xadra — 2-qavat			
Masshtab 1:100	Sana 14.10.2026	Versiya v1.2	Varaq 1 / 2
Bajardi: _____	Tekshirdi: _____		

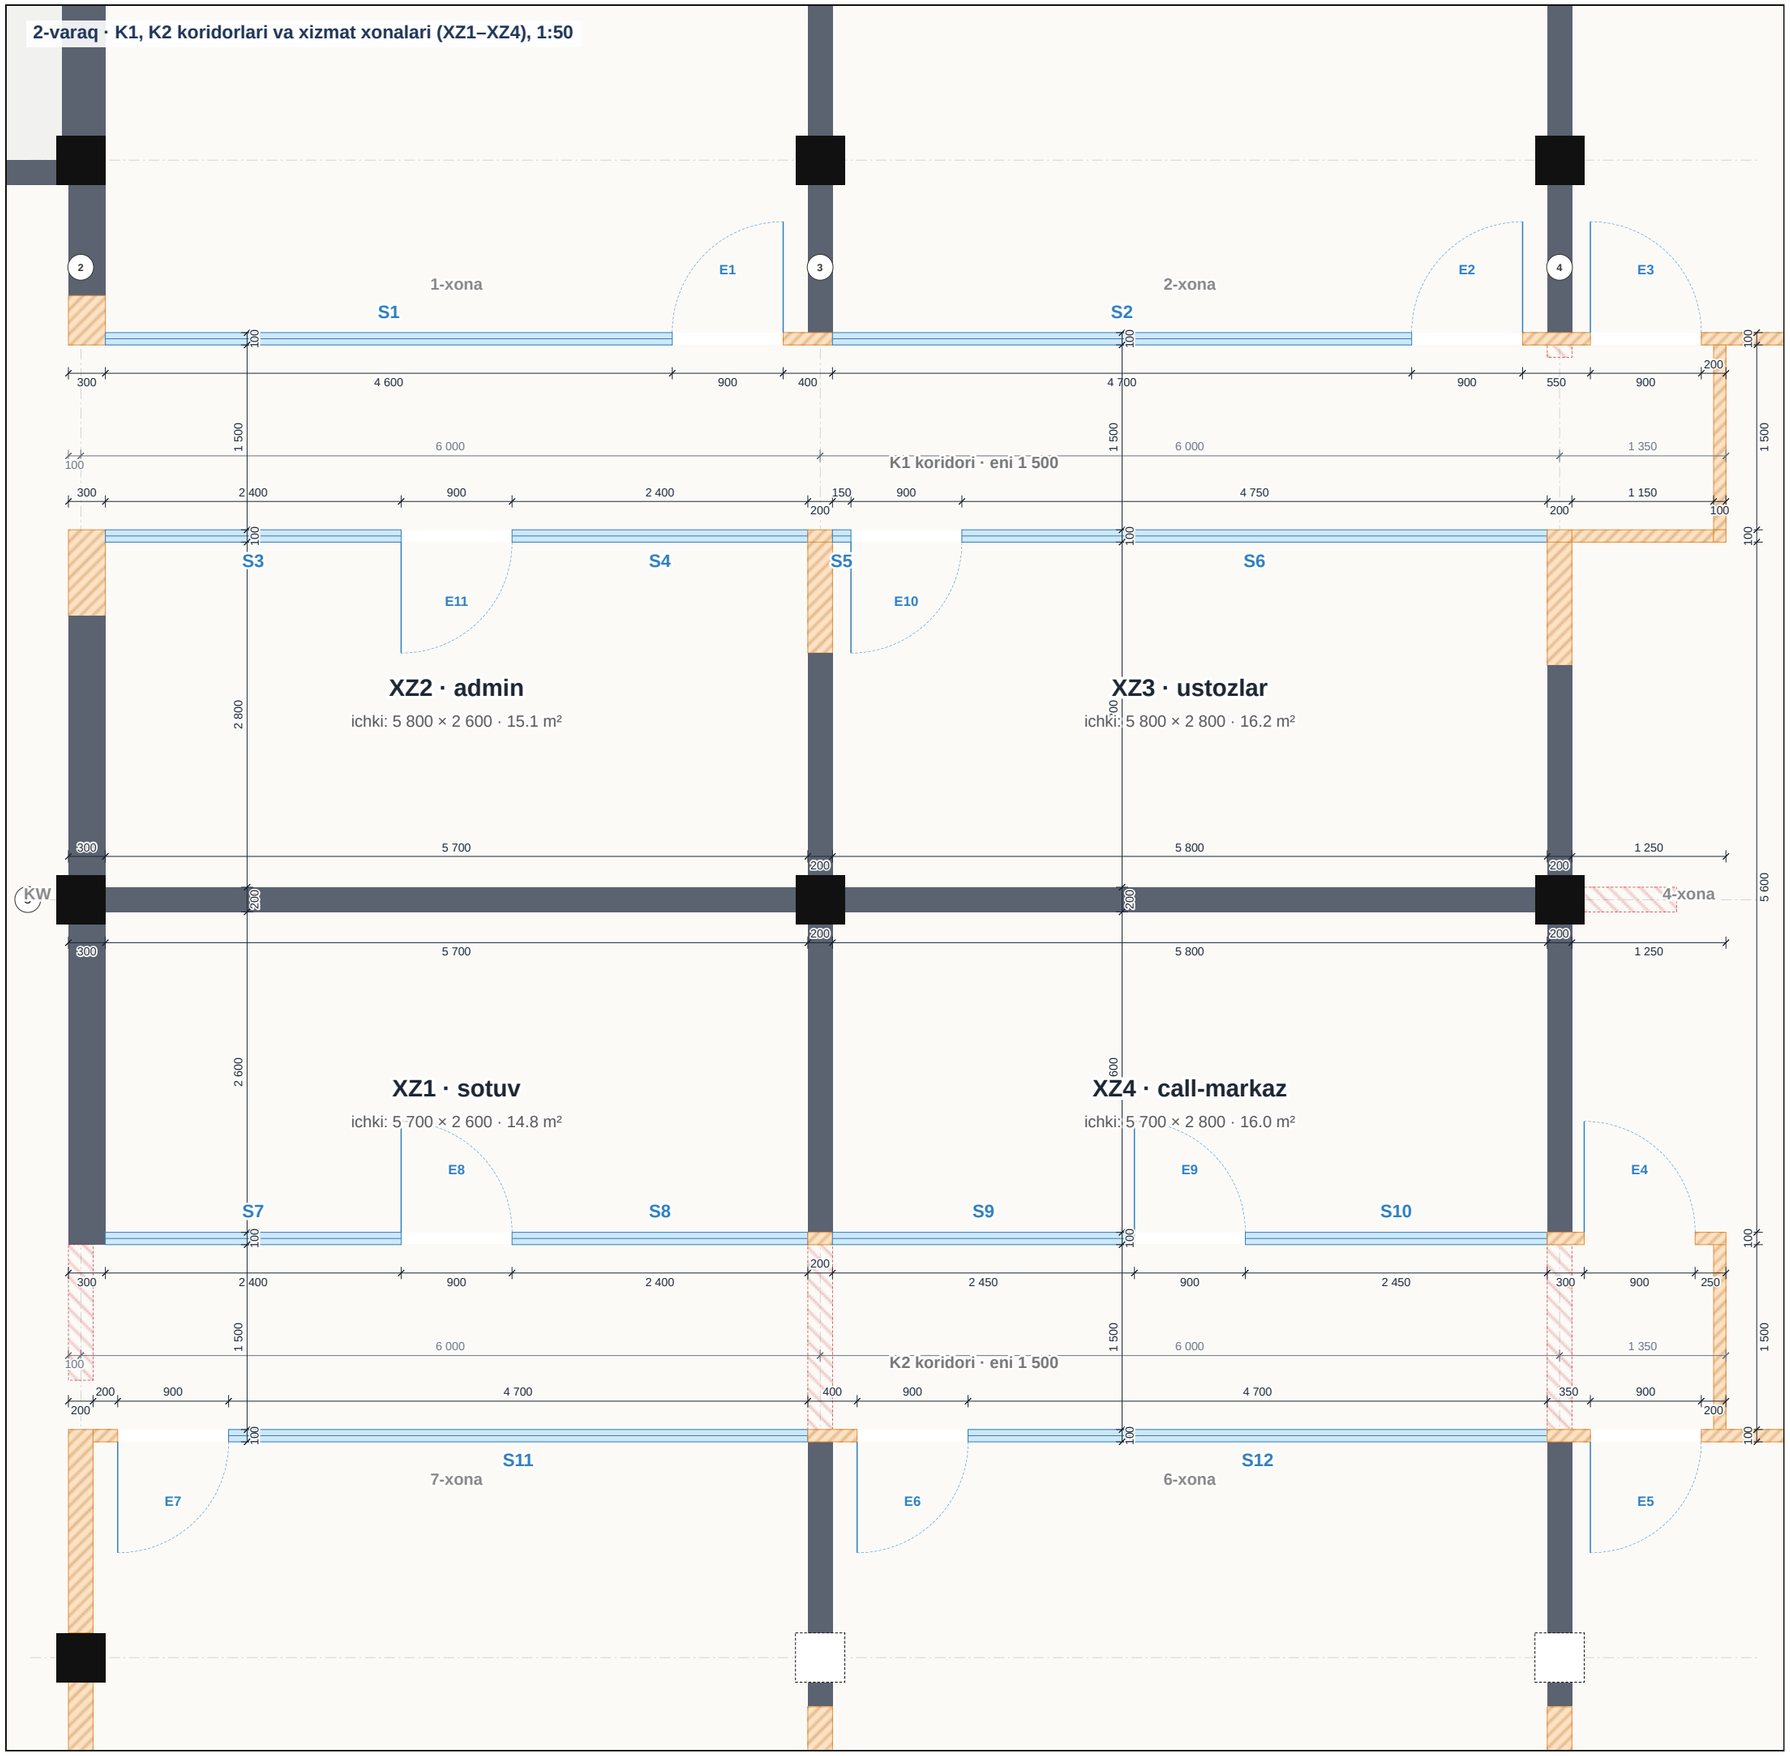

SHISHA DEVORLAR, ESHIKLAR VA GKL — JADVALLAR

Eshiklar (yangi, shisha) — 11 ta


Kod	Xona	Joyi	x, mm	O'lchami	Ilgagi (koridordan)
E1	1-xona	K1 shimoliy devori	10 850–11 750	900 × 2 100	o'ngda
E2	2-xona	K1 shimoliy devori	16 850–17 750	900 × 2 100	o'ngda
E3	3-xona	K1 shimoliy devori	18 300–19 200	900 × 2 100	chapda
E4	4-xona	K2 shimoliy devori	18 250–19 150	900 × 2 100	chapda
E5	5-xona	K2 janubiy devori	18 300–19 200	900 × 2 100	o'ngda
E6	6-xona	K2 janubiy devori	12 350–13 250	900 × 2 100	o'ngda
E7	7-xona	K2 janubiy devori	6 350–7 250	900 × 2 100	o'ngda
E8	XZ1 · sotuv	K2 shimoliy devori	8 650–9 550	900 × 2 100	chapda
E9	XZ2 · admin	K2 shimoliy devori	14 600–15 500	900 × 2 100	chapda
E10	XZ3 · ustozlar	K1 janubiy devori	12 300–13 200	900 × 2 100	o'ngda
E11	XZ4 · call-markaz	K1 janubiy devori	8 650–9 550	900 × 2 100	o'ngda

Shisha devorlar (S) — balandligi 2 500 mm

Kod	Joyi	x, mm	Uzunligi	m²
S1	K1 shimoliy devori	6 250–10 850	4 600	11.50
S2	K1 shimoliy devori	12 150–16 850	4 700	11.75
S3	K1 janubiy devori	6 250–8 650	2 400	6.00
S4	K1 janubiy devori	9 550–11 950	2 400	6.00
S5	K1 janubiy devori	12 150–12 300	150	0.38
S6	K1 janubiy devori	13 200–17 950	4 750	11.88
S7	K2 shimoliy devori	6 250–8 650	2 400	6.00
S8	K2 shimoliy devori	9 550–11 950	2 400	6.00
S9	K2 shimoliy devori	12 150–14 600	2 450	6.13
S10	K2 shimoliy devori	15 500–17 950	2 450	6.13
S11	K2 janubiy devori	7 250–11 950	4 700	11.75
S12	K2 janubiy devori	13 250–17 950	4 700	11.75
	Jami (eshiklarsiz)		**38 100**	**95.3**

Yangi GKL bo'laklari (to'q sariq) — eshik va ustunlar yonida; o'lchamlari zanjirlarda. Bo'shliqlarni yopish — 1-varaqda.

Shisha devor — tipik yoyilma (koridordan ko'rinish)

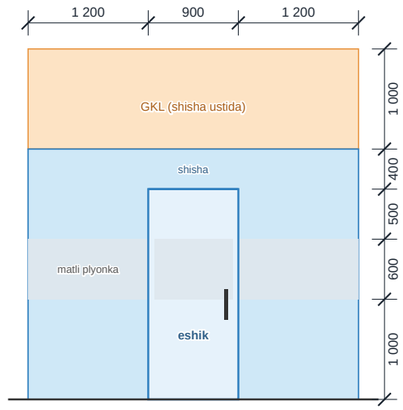

- Zanjirlar koridor ichida, koworking devori yuzasidan (x = 5 950) boshlanadi; o'qlar 2, 3, 4 — ustunlar markazi.
- XZ xonalari ichki eni 5 700 (XZ1, XZ2) va 5 800 (XZ3, XZ4); chuqurligi K1 tomonda 2 600, K2 tomonda 2 600 (o'rta devor 200 mm).

PDP Academy · Xadra filiali			
Chizma	**Koridorlar va xizmat xonalari — shisha, eshiklar**		
Ish chizmasi — ustalar uchun. Toshkent sh., Xadra — 2-qavat			
Masshtab 1:50	Sana 14.10.2026	Versiya v1.2	Varaq 2 / 2
Bajardi: _____	Tekshirdi: _____		