1-varaq · Yong'in signalizatsiyasi va ogohlantirish — 2-qavat, 1:100



YONG'IN SIGNALIZATSIYASI — ADRESSIZ, 53 DATCHIK

- tutun datchigi (adressiz), raqam — shleyf.tartib
- ovozli-yorug'lik sirenasi, 2.3 m
- avariya chirog'i (akkumulyatorli, 3 soat)
- IPR / sirena / tablo liniyalari
- qo'lda ishga tushirish tugmasi (IPR), 1.5 m
- «CHIQISH» tablosi / yo'nalish ko'rsatkichi
- shleyf kabeli (lotokda — bir marta)
- S1, S2 — stoyak

2-qavat shleyflari (pult — 1-qavat resepshnda, S1 orqali)

Shleyf	Xonalar	Datchik	Kabel, m
Sh1	2-qavat g'arbiy qismi: zina ZN1, WC, 6-xona, koworking, kirish, CEO	12	104
Sh2	2-qavat K1 tomoni: 1–3-xona, K1, KL1, XZ4, XZ3	13	129
Sh3	2-qavat K2 tomoni: 4–7-xona, K2, KL2, XZ1, XZ2	15	148


2-qavat: qo'shimcha (me'yor bo'yicha)

Qurilma	Joyi	Soni
IPR (qo'lda)	Q1 — ZN2 zinasiga chiqishda; Q2 — ZN1 zinasiga chiqishda; Q3 — K1 o'rtasida (1–2-xona orasidagi ustunda); Q4 — K2 o'rtasida (7–6-xona orasidagi ustunda)	4
Sirena	O1 — koworking shimoliy devori; O2 — K1, XZ3 devori; O3 — K2, XZ2 devori; O4 — kirish zali	4
«CHIQISH» / ko'rsatkich	T1 — ZN2 zinasiga chiqish; T2 — 6-xona (ZN1 ga) eshigi ustida; T3 — ZN1 zina eshigi ustida; T4 — yo'nalish ko'rsatkichi (koworking tomonga); T5 — yo'nalish ko'rsatkichi (koworking tomonga)	5
Avariya chirog'i	koridorlar, koworking, kirish zali, 6-xona, zinalar	10


- Datchiklar shiftda, devordan ≥ 0.5 m, diffuzor va panjaradan ≥ 1 m (joyida suriladi); kladovkalarda (KL1, KL2) ham — konditsioner bloklari ustida.
- Shleyf — 2 simli, oxirida rezistor; bir shleyfda ≤ 10 xona. Kabel olovga chidamli, kuch kabellaridan alohida (gofra quvurda, lotokda ≥ 0.5 m oraliq).

PDP Academy · Xadra filiali			
Chizma	**Yong'in signalizatsiyasi — 2-qavat**		
Ish chizmasi — ustalar uchun. Qurilmalar joyi — buyurtmachi belgilagan (18.10). Toshkent sh., Xadra — 2-qavat			
Masshtab 1:100	Sana 18.10.2026	Versiya v1.2	Varaq 1 / 2
Bajardi: _____	Tekshirdi: _____		


3-QAVAT

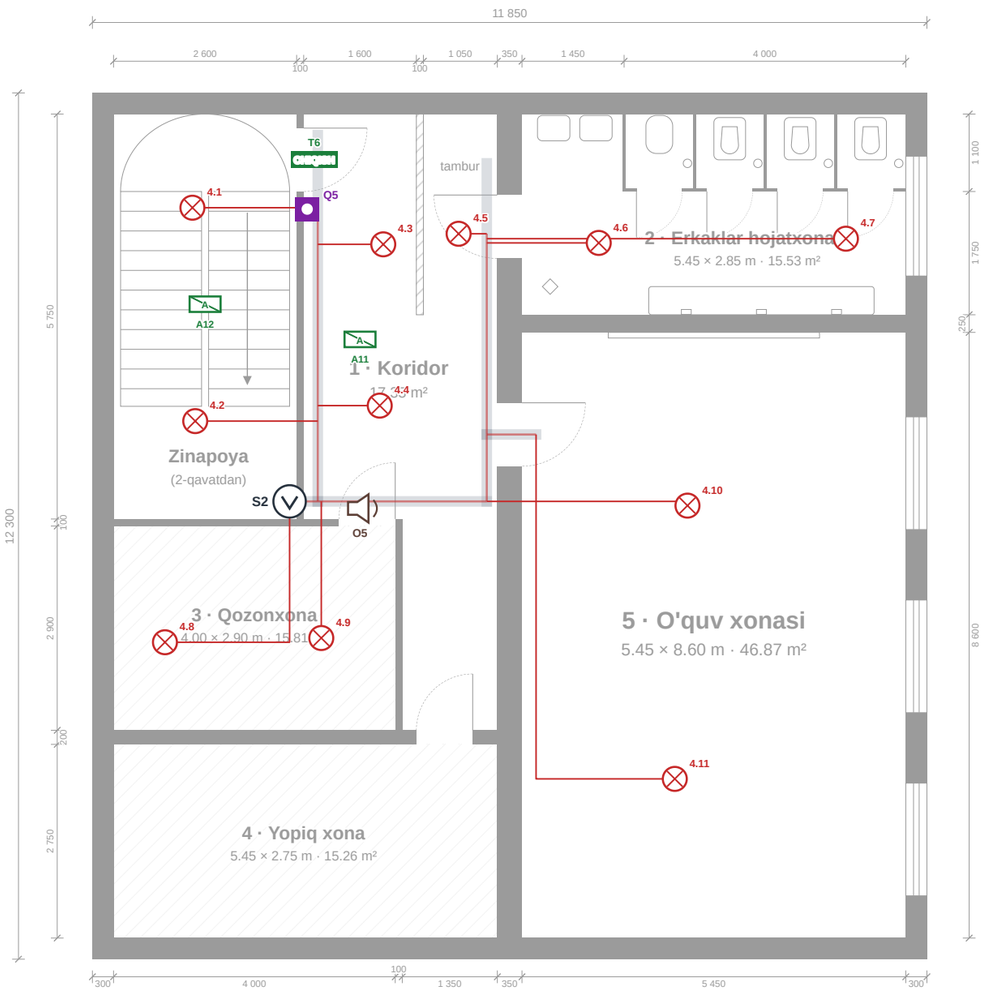

1-QAVAT (kirish zali)

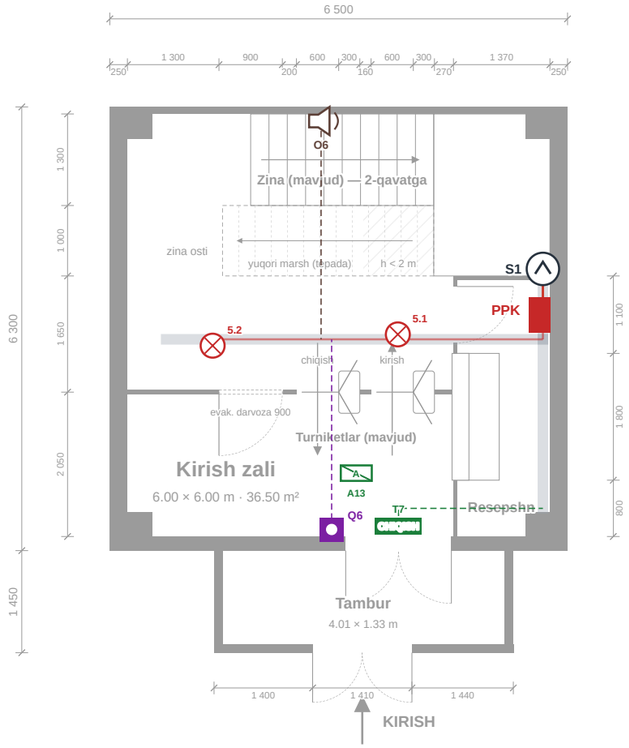

TUZILMA SXEMASI

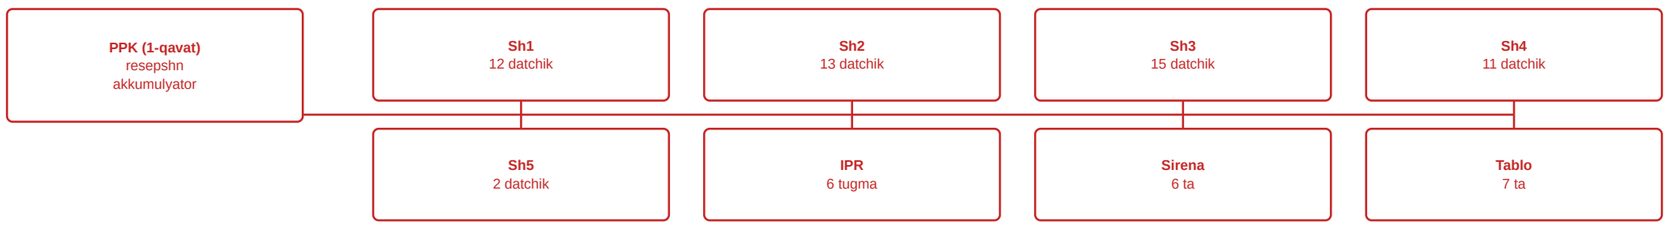

YONG'IN — 3- VA 1-QAVAT, PULT

- tutun datchigi (adressiz), raqam — shleyf.tartib
- ovozli-yorug'lik sirenasi, 2.3 m
- avariya chirog'i (akkumulyatorli, 3 soat)
- IPR / sirena / tablo liniyalari
- qo'lda ishga tushirish tugmasi (IPR), 1.5 m
- «CHIQISH» tablosi / yo'nalish ko'rsatkichi
- shleyf kabeli (lotokda — bir marta)
- S1, S2 — stoyak

3- va 1-qavat shleyflari

Shleyf	Xonalar	Datchik	Kabel, m
Sh4	3-qavat: zina, koridor, tambur, WC, qozonxona, 5-xona	11	101
Sh5	1-qavat: zal	2	8

Jami (1–3-qavat)

Qurilma	Soni
Pult PPK (adressiz, ≥ 8 shleyf, akkumulyatorli; 1-qavat resepshn, sharqiy devor)	1
Tutun datchigi (buyurtmachi belgilagan 50 + kladovkalar 2 + 3-qavat tamburi 1)	53
IPR — qo'lda ishga tushirish tugmasi	6
Ovozli-yorug'lik sirenasi	6
«CHIQISH» tablosi va yo'nalish ko'rsatkichi	7
Avariya chirog'i (220 V, akkumulyatorli; yaqin yoritish guruhidan)	13
Kabel olovga chidamli 1×2×0.75 (shleyflar, IPR)	**577 m**
Kabel olovga chidamli 1×2×1.0 (sirena, tablo)	**154 m**

- Uzunlik: lotokdagi qismi bir marta, datchikka tarmoq ikki marta (kirish va chiqish) × 1.1, tushishlar va pultda 1.5 m.
- 3-qavat shleyfi ZN1 (S2) va ZN2 (S1) orqali pultga; 3-qavat tamburiga (yangi devor ortida) 1 datchik qo'shildi.
- Narx — buyurtmachi summasi (Excel, «Yong'in xavfsizligi»); chizmadagi miqdorlar pudratchi smetasini tekshirish uchun.

PDP Academy · Xadra filiali

Chizma	**Yong'in signalizatsiyasi — 3- va 1-qavat**

Ish chizmasi — ustalar uchun. Qurilmalar joyi — buyurtmachi belgilagan (18.10). Toshkent sh., Xadra — 3- va 1-qavat

Masshtab	Sana	Versiya	Varaq
~1:90	18.10.2026	v1.2	2 / 2

Bajardi: _____ Tekshirdi: _____