
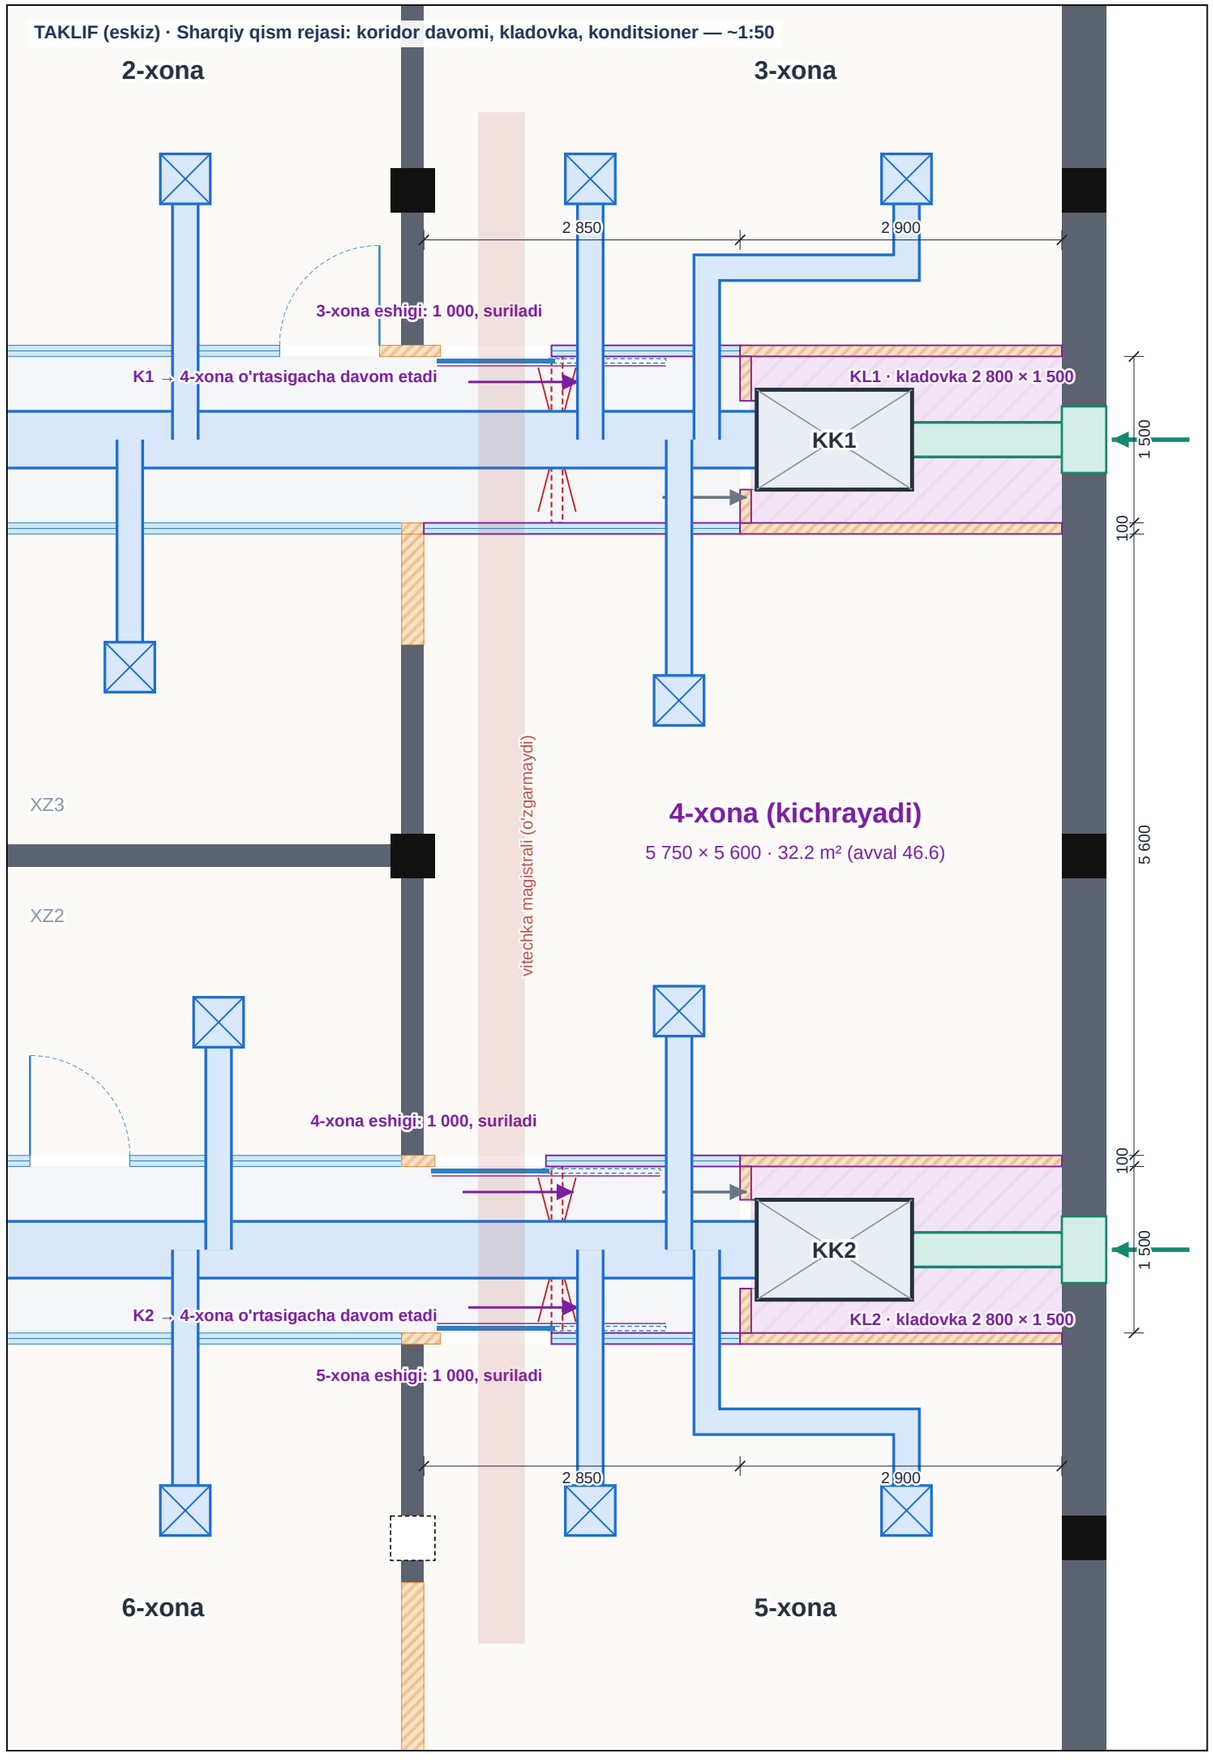


Koridorlar 4-xona orqali davom etadi — tushunganim (tasdiq uchun)


PDP Academy · Xadra filiali · 2-qavat · 16.10.2026 · model hali o'zgartirilmagan — tasdiqdan keyin chizmalar, 3D, xarajat qayta tayyorlanadi

yangi shisha devor · yangi GKL · olib tashlanadi (logotip devori) · kladovka · konditsioner kanali, diffuzor · tashqi havo 30%

Kesim A–A: K1 koridori o'qi bo'ylab (3-xona devoriga qarab), ~1:50

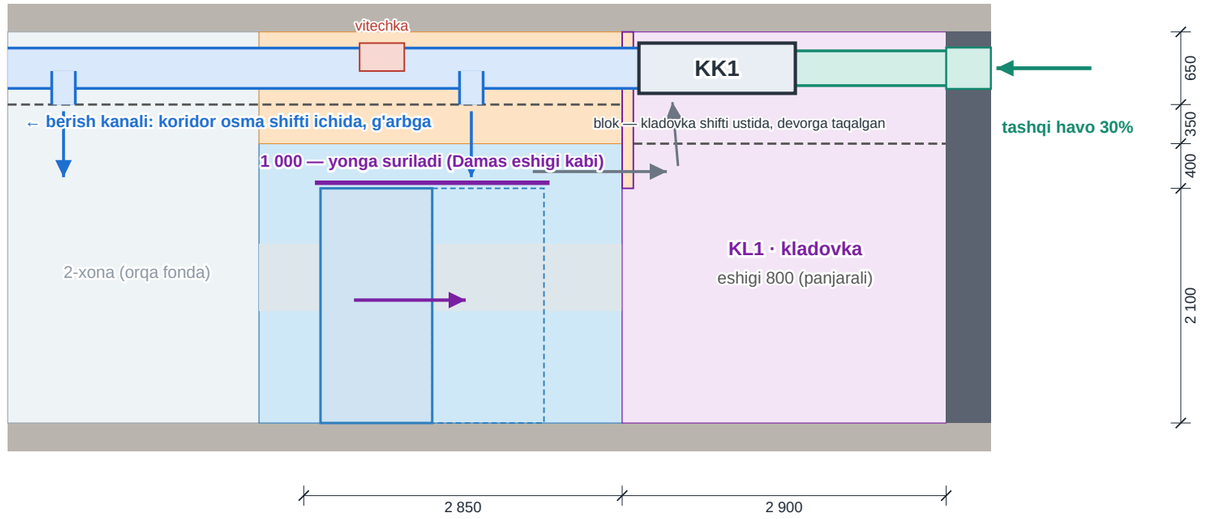

Eshik: 1 m, yonga suriladi (Damas eshigi kabi)

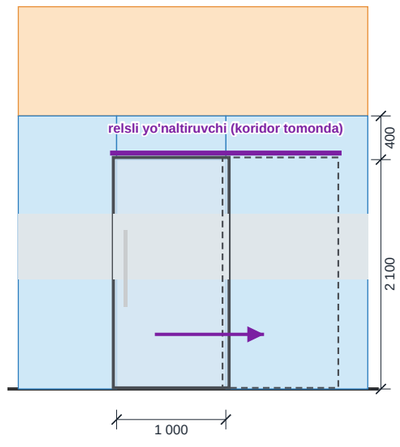

Barg devor bo'ylab suriladi, ochilganda yonidagi shisha oldida turadi — koridorga ham, xonaga ham ochilmaydi.

Tushunganim

1. **K1 va K2 koridorlari** 4-xona orqali davom etadi; koridor oxiridagi logotip devorlari (hozir 19.3 m da) olib tashlanadi.
2. **4-xonaning o'rtasida** (x ≈ 21 000) koridor ko'ndalang devor bilan yopiladi, eshigi bor — orqasi **kladovka** (KL1, KL2, ~2 800 × 1 500, 4.2 m²).
3. **4-xona kichrayadi:** 5 750 × 5 600 = 32.2 m² (avval 46.6). 24 o'rin sig'ishi tekshiriladi.
4. **3-, 4-, 5-xonaning** koridorga qaragan devori kladovkagacha **shisha**; kladovka qismi — GKL.
5. **Eshiklar 1 m, yonga suriladigan** (founder taklifi) — rasmda 3-, 4-, 5-xona eshiklari.
6. **Konditsioner:** har kladovka ustida, devorga taqalgan kanalli blok (KK1, KK2); havo koridor bo'ylab to'g'ri kanal bilan, xonalarga avvalgi chizmadagidek (sinfga 2, XZ ga 1 diffuzor). Qaytish havosi — kladovka eshigidagi panjara orqali.
7. **Tashqi havo 30%** — kladovka orqasidagi tashqi devordan (derazasiz), panjara orqali blokka. 3-xona fasadidan olish endi kerak emas.
8. **Vitechka** o'zgarmaydi (magistral koridorlarni kesib o'tadi — kanallar balandlik bo'yicha ajratiladi).

Diqqat: 30% tashqi havoda har blok ~1 500 m³/soat oladi — sinfga ~400 m³/soat (me'yor 600): to'la sinfda CO_2 ~1 400–1 500 ppm, havo biroz og'irlashadi. Shuning uchun vitechka ham shunga moslab (~3 000 m³/soat) kamaytiriladi, aks holda qavat manfiy bosimda qoladi. Blok quvvati masalasi (96k yetmasligi) hali ochiq.