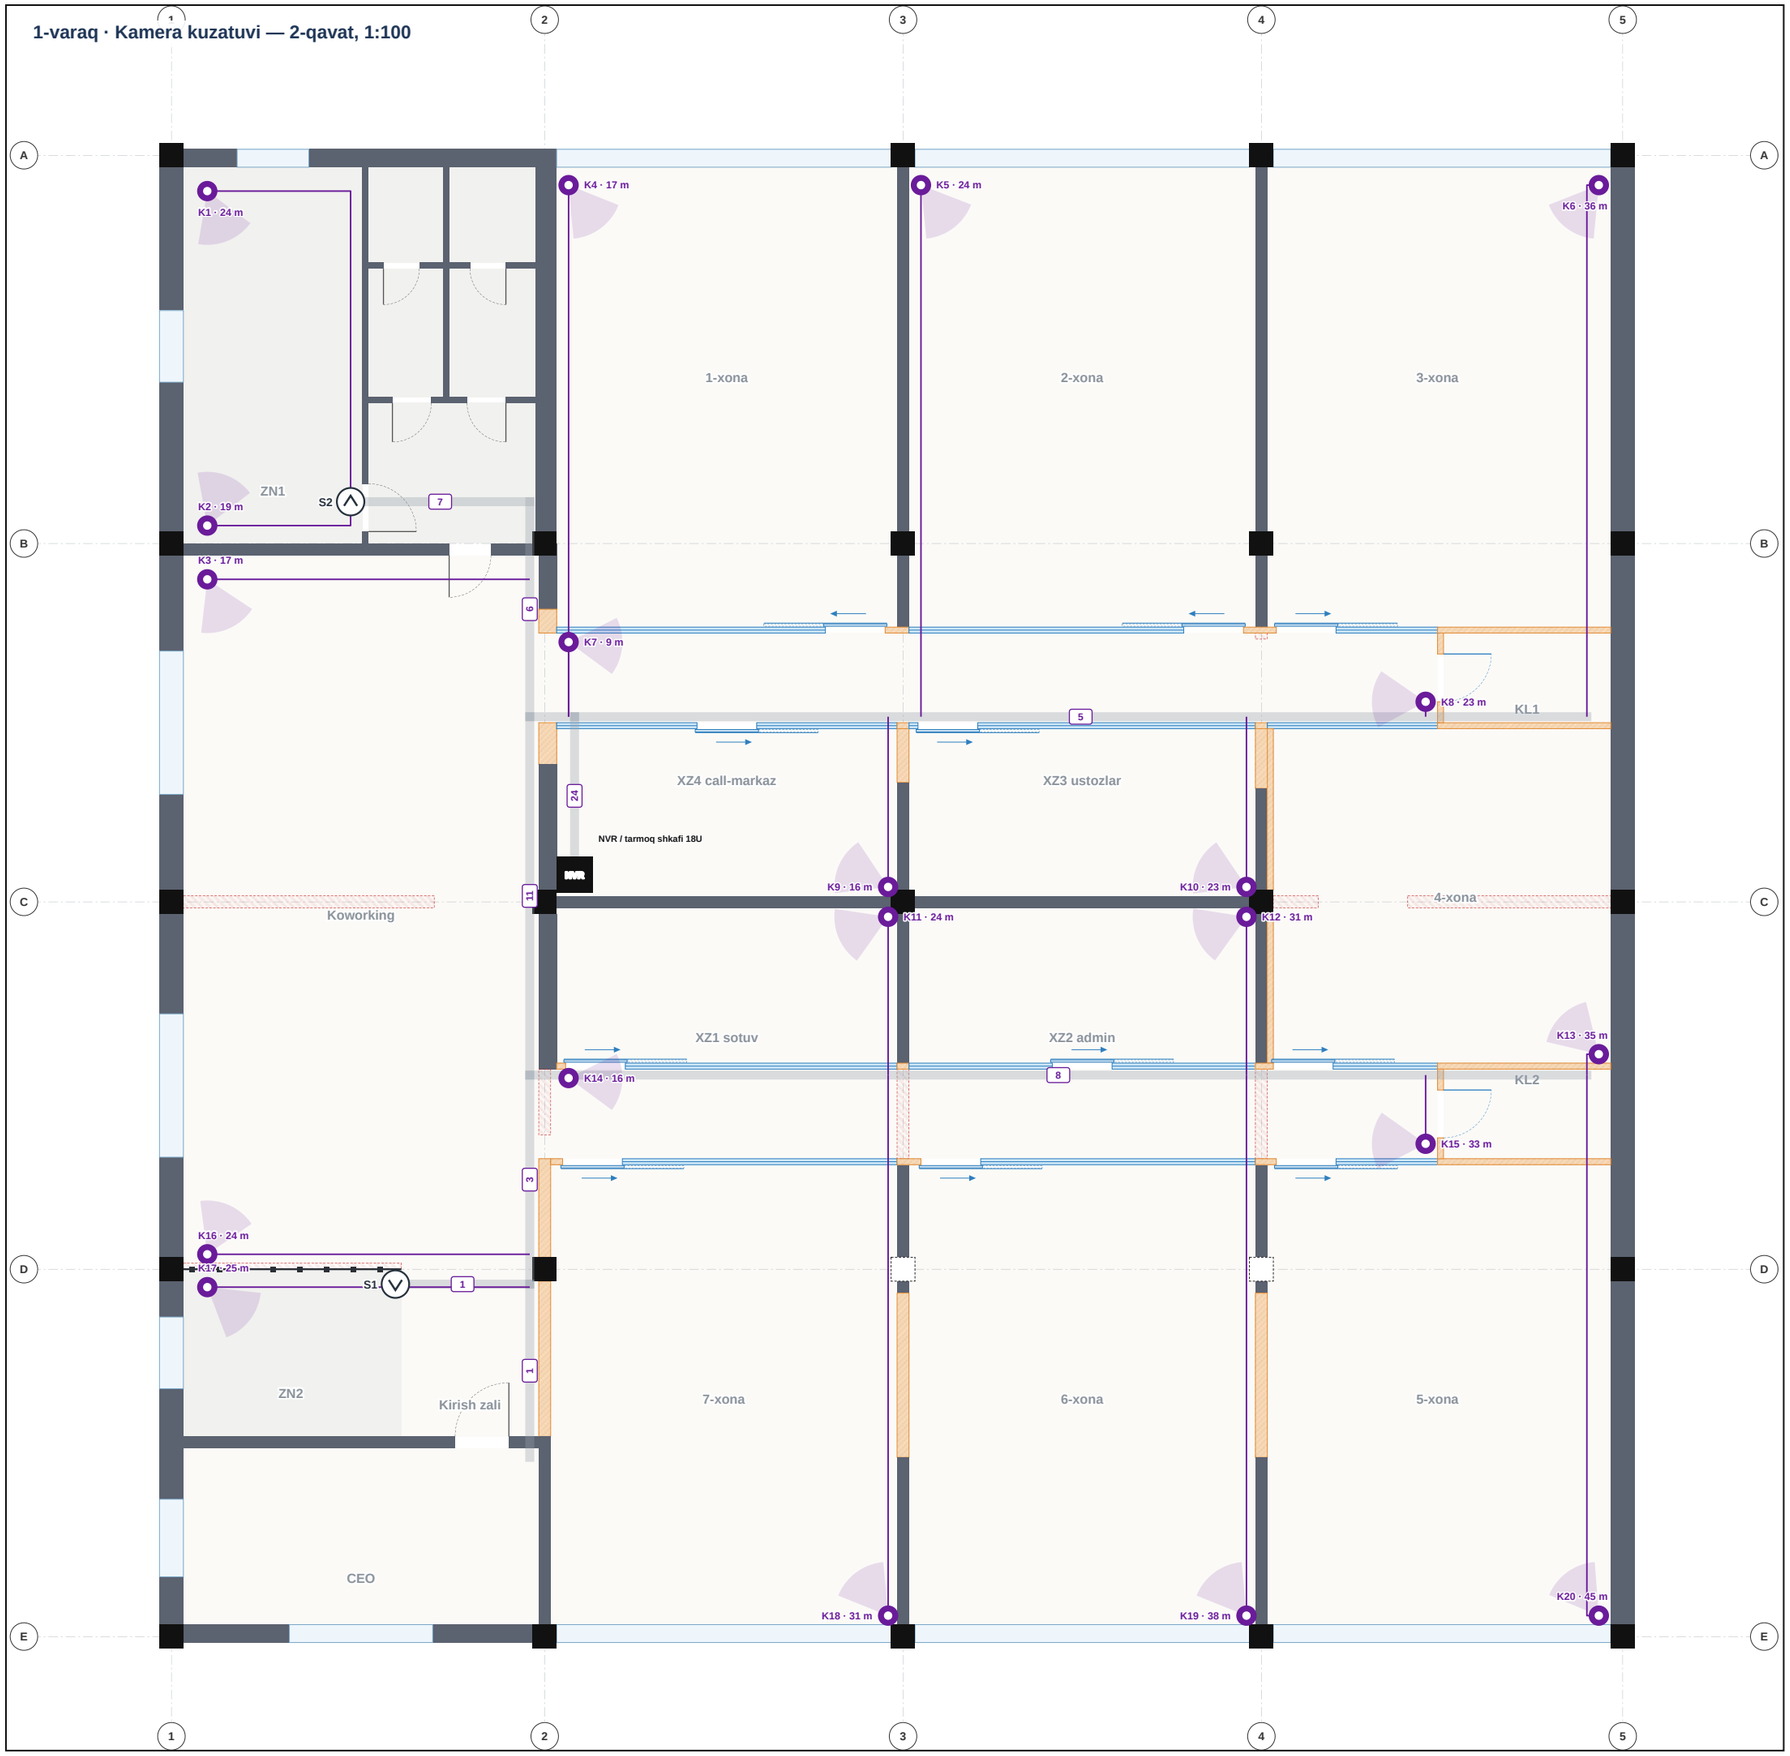


KAMERA KUZATUVI — 24 ta IP kamera (PoE)

- IP kamera (PoE), shiftda yoki devor tepasida; ko'rish yo'nalishi
- Cat6 kabeli (har kameraga alohida)
- past tokli lotok (shift ostida); raqam — kabellar soni
- NVR / tarmoq shkafi (XZ4)
- S1, S2 — qavatlararo stoyak

2-qavat — 20 ta

Kod	Joy	Xona	Cat6, m
K1	zina — shimoli-g'arbiy burchak	ZN1	24
K2	zina — janubi-g'arbiy burchak	ZN1	19
K3	koworking — shimoli-g'arbiy burchak	Koworking	17
K4	shimoli-g'arbiy burchak	1-xona	17
K5	shimoli-g'arbiy burchak	2-xona	24
K6	shimoli-sharqiy burchak	3-xona	36
K7	g'arbiy boshi	K1	9
K8	sharqiy oxiri, kladovka oldida	K1	23
K9	janubi-sharqiy burchak	XZ4 call-markaz	16
K10	janubi-sharqiy burchak	XZ3 ustozlar	23
K11	shimoli-sharqiy burchak	XZ1 sotuv	24
K12	shimoli-sharqiy burchak	XZ2 admin	31
K13	janubi-sharqiy burchak	4-xona	35
K14	g'arbiy boshi	K2	16
K15	sharqiy oxiri, kladovka oldida	K2	33
K16	koworking — janubi-g'arbiy burchak, panjara oldida	Koworking	24
K17	kirish zinasi — g'arbiy devorda	ZN2	25
K18	janubi-sharqiy burchak	7-xona	31
K19	janubi-sharqiy burchak	6-xona	38
K20	janubi-sharqiy burchak	5-xona	45

Uzunlik: kameradan lotokkacha va lotok bo'ylab shkafgacha × 1.1 (burilish va aylanib o'tish) + kamerada 0.3 m tushish, shkafda 2.3 m + zaxira 2 m. Lotokdagi raqam — shu bo'lakdagi kabellar soni (lotok eni tanlash uchun).

- Har kamera o'z Cat6 (U/UTP, 4×2×0.5, LSZH) kabeli bilan shkafdagi PoE switchga; kabel uzunligi ≤ 90 m.
- Koridor va xonalarda kabel shift ostidagi lotokda / shift bo'shlig'ida, devorda — gofra quvurda (Ø20); GKL va mavjud devordan teshik orqali.
- Kamera balandligi ~2.8–3.2 m; ko'rish burchagi joyida sozlanadi (sxemadagi sektor — taxminiy).

PDP Academy · Xadra filiali


Chizma	**Kamera kuzatuvi — 2-qavat**

Ish chizmasi — ustalar uchun. Qurilmalar joyi — buyurtmachi belgilagan (18.10). Toshkent sh., Xadra — 2-qavat


Masshtab	Sana	Versiya	Varaq
1:100	18.10.2026	v1.2	1 / 2

Bajardi: _____ Tekshirdi: _____


3-QAVAT

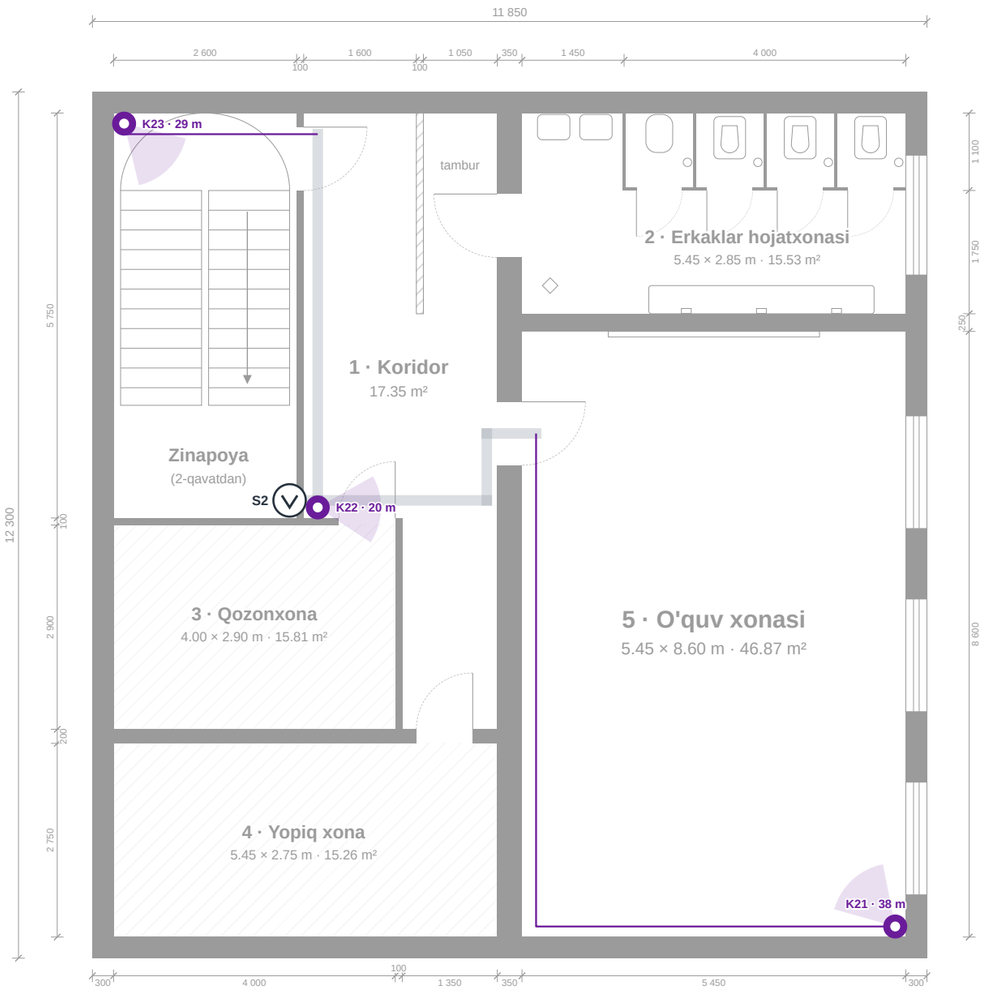

1-QAVAT (kirish zali)

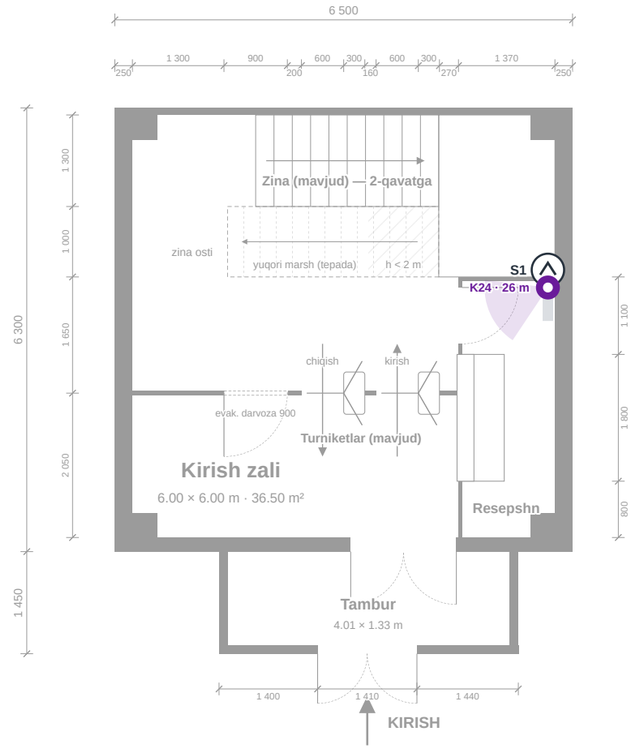

TUZILMA SXEMASI

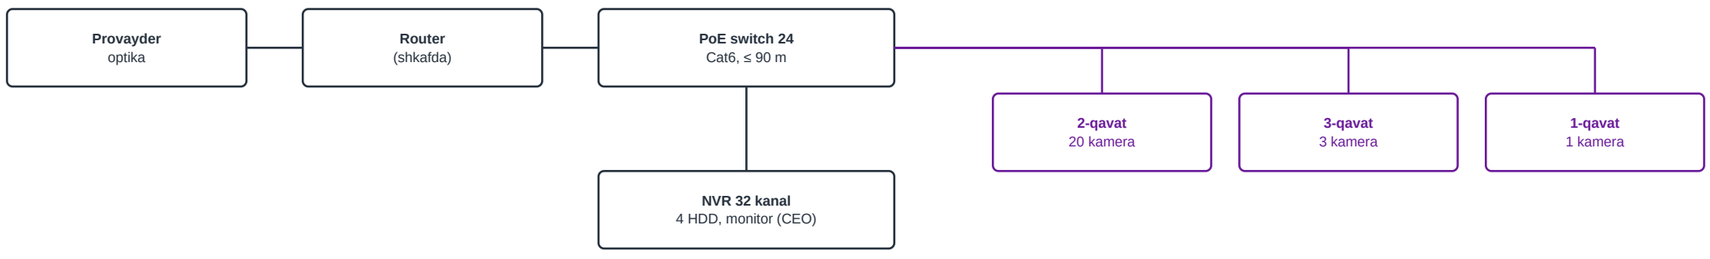

KAMERA — 3- VA 1-QAVAT, SHKAF

- IP kamera (PoE), shiftda yoki devor tepasida; ko'rish yo'nalishi
- past tokli lotok (shift ostida); raqam — kabellar soni
- S1, S2 — qavatlararo stoyak
- Cat6 kabeli (har kameraga alohida)
- NVR / tarmoq shkafi (XZ4)

3-qavat va 1-qavat — 4 ta

Kod	Joy	Xona	Cat6, m
K21	o'quv xonasi — janubi-sharqiy burchak	3-q. 5-xona (o'quv)	38
K22	koridor — zina va qozonxona devori burchagi	3-q. koridor	20
K23	zina — shimoli-g'arbiy burchak	3-q. zina	29
K24	resepshn — sharqiy devor, zal va eshikka qaragan	1-q. zal	26

Shkaf (XZ4, g'arbiy burchak, pol shkafi 600 × 600, 18U)

Jihoz	Soni
NVR 32 kanal, 4 HDD (jami ~16 TB — ~30 kun, 4 MP H.265+)	1
PoE switch 24 port (kameralar uchun, ≥ 370 W)	1
Patch-panel 24 port Cat6 (kameralar)	1
UPS 1.5 kVA (shkaf uchun umumiy), PDU, organayzerlar	1

Kabel

Nomi	m
Cat6 U/UTP LSZH — 24 ta kamera (+ ~10% zaxira — Excel)	**623**
shundan 2-qavat / 3-qavat / 1-qavat	511 / 87 / 26

- 3-qavat kabellari ZN1 zinasi bo'ylab (S2), 1-qavatniki — asosiy zina (ZN2) bo'ylab (S1) gofra quvurda 2-qavat lotokiga.
- Shkafga provayder kirishi (optika) — tashqi devordan, shkaf yonida; shkafga alohida rozetka (R8 guruhi, XZ4 g'arbiy devor).

PDP Academy · Xadra filiali

Chizma	**Kamera kuzatuvi — 3- va 1-qavat**

Ish chizmasi — ustalar uchun. Qurilmalar joyi — buyurtmachi belgilagan (18.10). Toshkent sh., Xadra — 3- va 1-qavat

Masshtab	Sana	Versiya	Varaq
~1:90	18.10.2026	v1.2	2 / 2

Bajardi: _____ Tekshirdi: _____