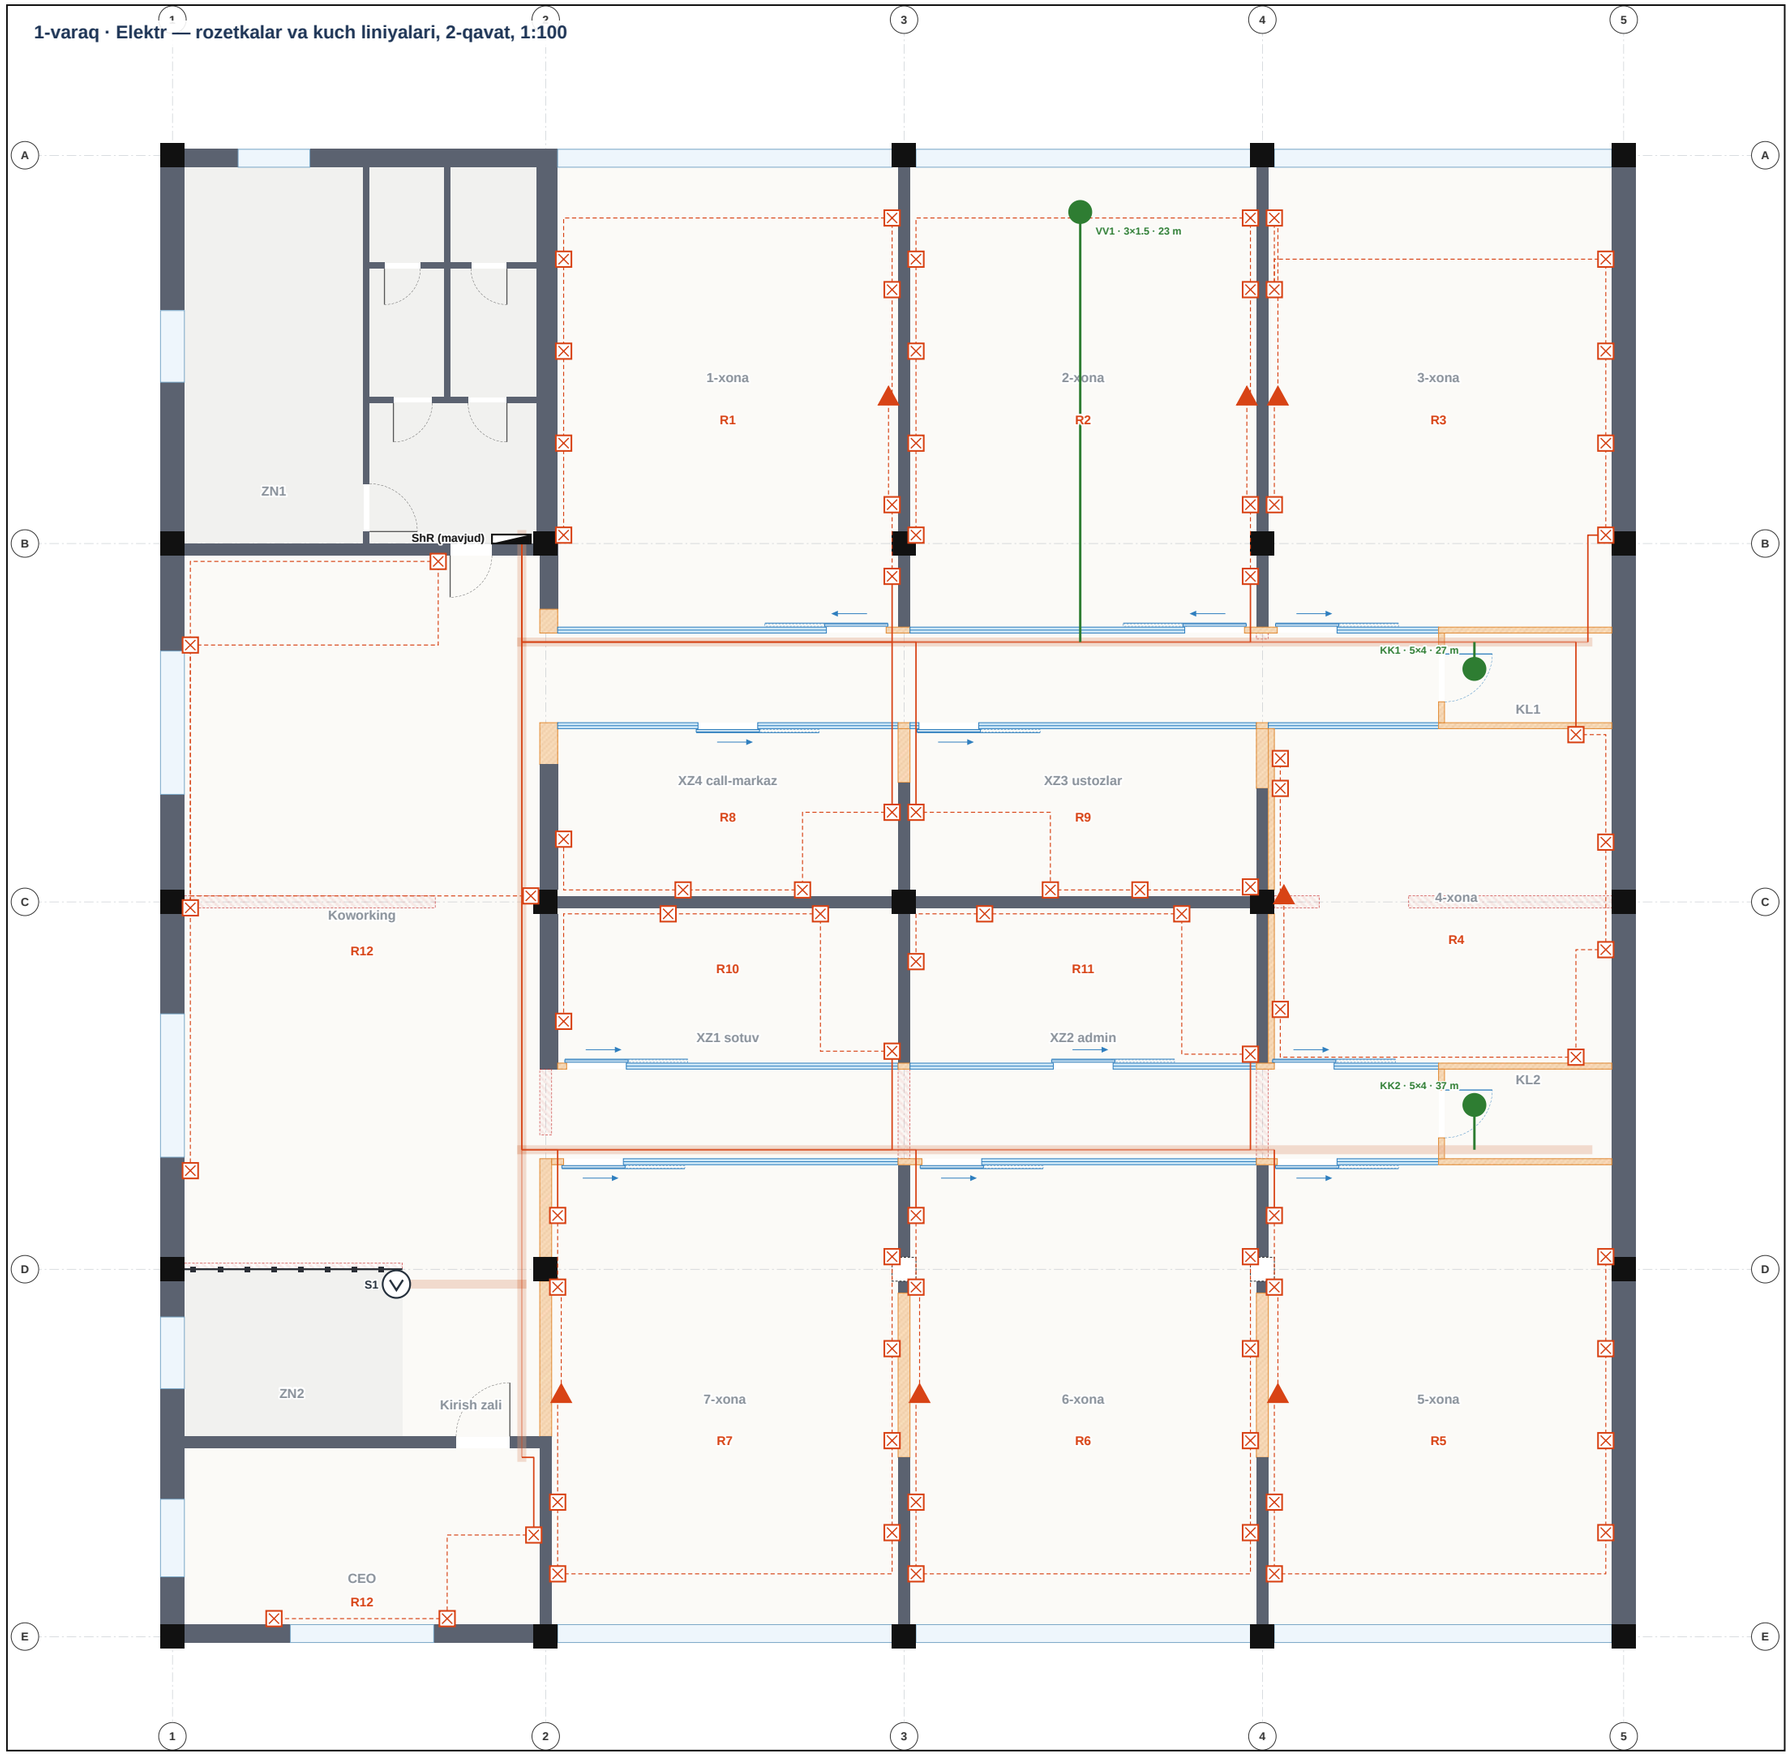


ELEKTR — ROZETKALAR, KUCH LINIYALARI (2-qavat)

- rozetka (poldan 30 sm), 2P+E
- interaktiv doska rozetkasi, 1.6 m
- guruh kabeli 3×2.5 (shitdan xonagacha)
- xona ichida — devorda gofra quvurda
- kuch liniyasi (KK1, KK2, VV1)
- kuch lotogi (shift ostida)

Rozetka guruhlari — har sinfga alohida avtomat

Guruh	Xona	Roz.	1.6 m	kW	3×2.5, m
R1	1-xona	8	1	2.0	36
R2	2-xona	8	1	2.0	43
R3	3-xona	7	1	2.0	50
R4	4-xona	7	1	2.0	49
R5	5-xona	8	1	2.0	53
R6	6-xona	8	1	2.0	46
R7	7-xona	8	1	2.0	40
R8	call-markaz (+ tarmoq shkafi)	4		2.0	25
R9	ustozlar	4		1.5	25
R10	sotuv	4		1.0	35
R11	admin	4		1.0	41
R12	koworking, CEO	8		2.0	66
R13	1-qavat resepshn	2		0.5	29
Jami		**80**	**7**	**22.0**	**538**

Kuch liniyalari

Liniya	Kabel	Avtomat	kW	m
KK1 — tashqi blok (tomda) + ichki blok	VVGng-LS 5×4	3P C25	10	27
KK2 — tashqi blok (tomda) + ichki blok	VVGng-LS 5×4	3P C25	10	37
VV1 — vitechka ventilyatori	VVGng-LS 3×1.5	C10	0.4	23

- Kabel shitdan xonagacha — shift ostidagi kuch lotogida (past tokli lotokdan alohida), xona ichida — devorda gofra quvurda (Ø20), rozetkadan rozetkaga.
- KK1, KK2 — 380 V, tashqi blokka (tomda) kladovkadan stoyak; ichki blok tashqi blokdan (3×1.5, konditsioner bilan birga keladi).
- Rozetkalar joyi — buyurtmachi belgilagan; 2-xonadagi qizil «+» — xato (buyurtmachi), qo'yilmaydi.

PDP Academy · Xadra filiali


Chizma	**Elektr — rozetkalar va kuch liniyalari**

Ish chizmasi — ustalar uchun. Qurilmalar joyi — buyurtmachi belgilagan (18.10). Toshkent sh., Xadra — 2-qavat

Masshtab	Sana	Versiya	Varaq
1:100	18.10.2026	v1.2	1 / 3

Bajardi: _____ Tekshirdi: _____

2-varaq · Elektr — yoritish, 2-qavat, 1:100

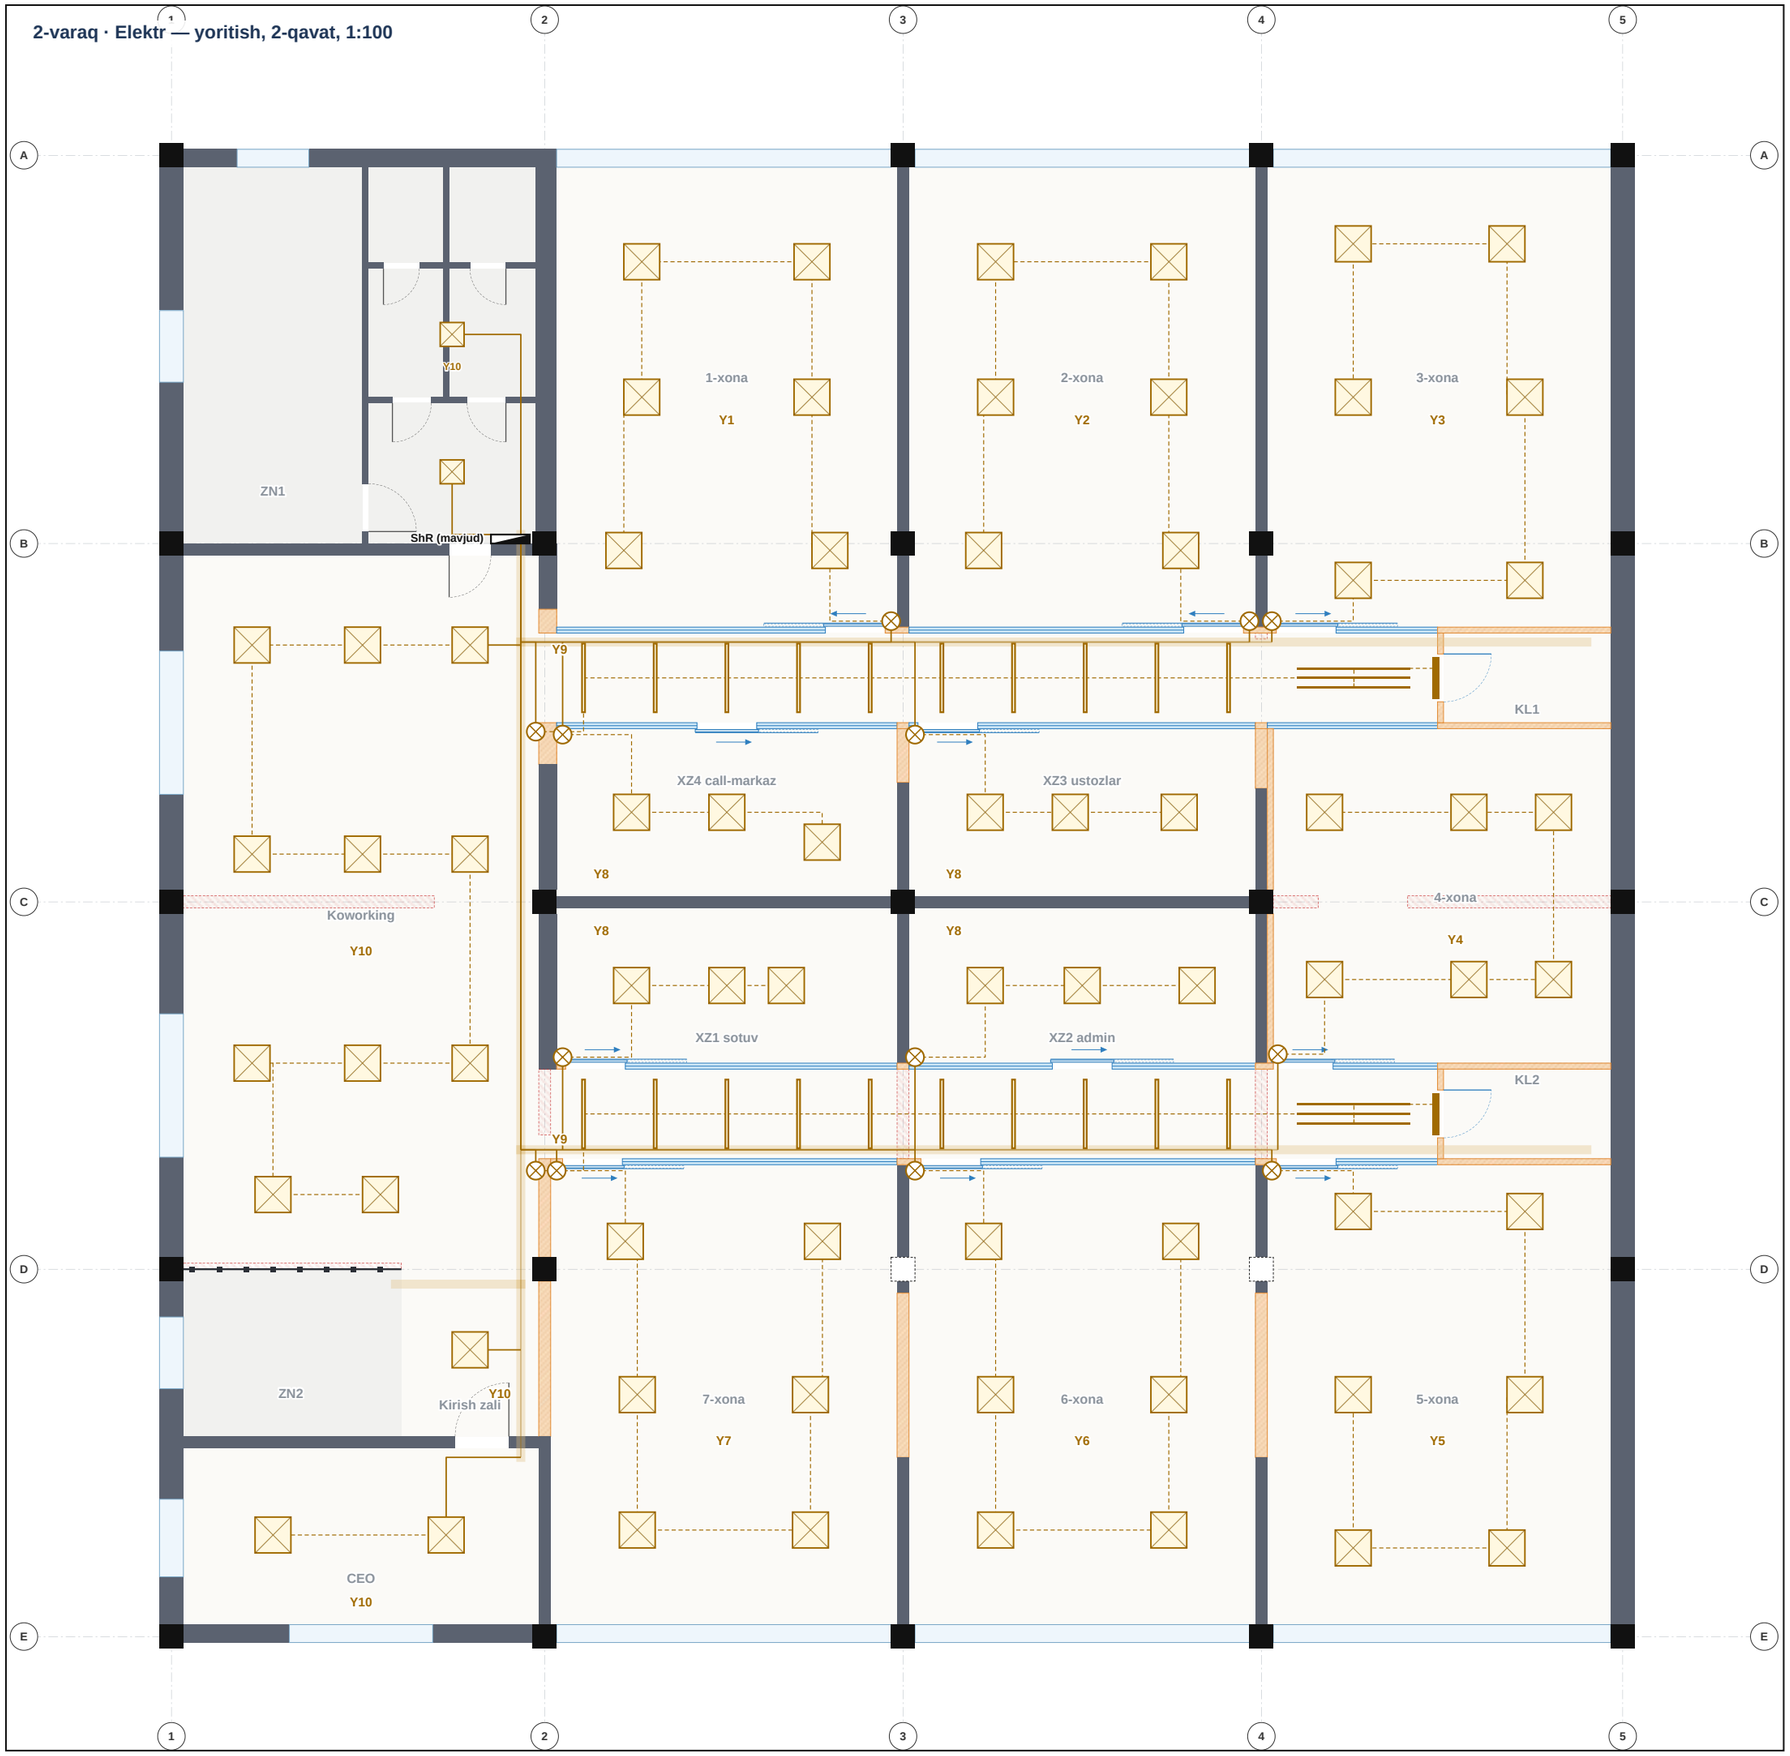

ELEKTR — YORITISH (2-qavat)

- LED panel 600×600, 36 W (3D bilan bir xil joyda)
- koridor chiziqli chirog'i 1150, 36 W
- vyklyuchatel, 0.9 m
- guruh kabeli 3×1.5
- chiroqdan chiroqqa (shiftda)

Yoritish guruhlari

Guruh	Xonalar	Chiroq	Vykl.	kW	3×1.5, m
Y1	1-xona	6	1	0.22	33
Y2	2-xona	6	1	0.22	39
Y3	3-xona	6	1	0.22	41
Y4	4-xona	6	1	0.22	48
Y5	5-xona	6	1	0.22	50
Y6	6-xona	6	1	0.22	43
Y7	7-xona	6	1	0.22	36
Y8	xizmat xonalari (XZ1–XZ4)	12	4	0.43	80
Y9	koridorlar, kanopi, logotiplar, yashil LED	28	2	1.51	63
Y10	koworking, kirish zali, CEO, WC tamburi, 6-xona	16	—	0.55	62
Jami		**98**	**13**	**4.01**	**494**


- Chiroqlar joyi 3D bilan bir xil (diffuzor va panjaralardan suriladi). Vyklyuchatel — buyurtmachi belgilagan 13 ta: 7 sinf, 4 xizmat xonasi, K1 va K2 (koworking tomonda).
- Koworking, kirish zali, CEO, WC tamburi va 6-xonada vyklyuchatel qo'shilmaydi (buyurtmachi) — Y10 guruh avtomatidan yoki mavjud vyklyuchateldan.
- Y9: koridor chiroqlari, kanopi LED, yoritilgan logotiplar (2) va yashil LED tasma (2 × 12.6 m, 24 V blok bilan).
- Avariya chiroqlari — yong'in chizmasida (akkumulyatorli, yaqin guruhdan).

PDP Academy · Xadra filiali

Chizma	**Elektr — yoritish**
Ish chizmasi — ustalar uchun. Qurilmalar joyi — buyurtmachi belgilagan (18.10). Toshkent sh., Xadra — 2-qavat	
Masshtab: 1:100	Sana: 18.10.2026
Versiya: v1.2	Varaq: 2 / 3


Bajardi: _____ Tekshirdi: _____

3-QAVAT

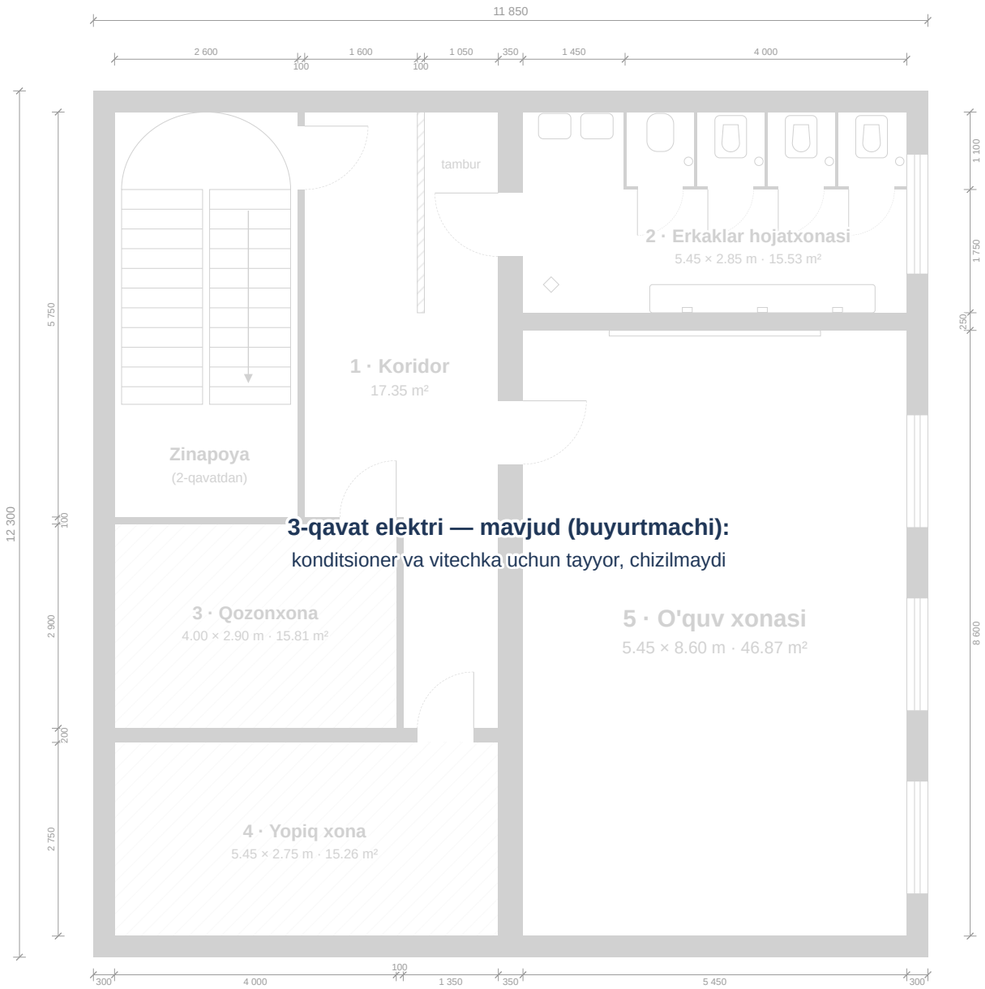

3-qavat elektri — mavjud (buyurtmachi):
konditsioner va vitechka uchun tayyor, chizilmaydi

1-QAVAT (kirish zali)

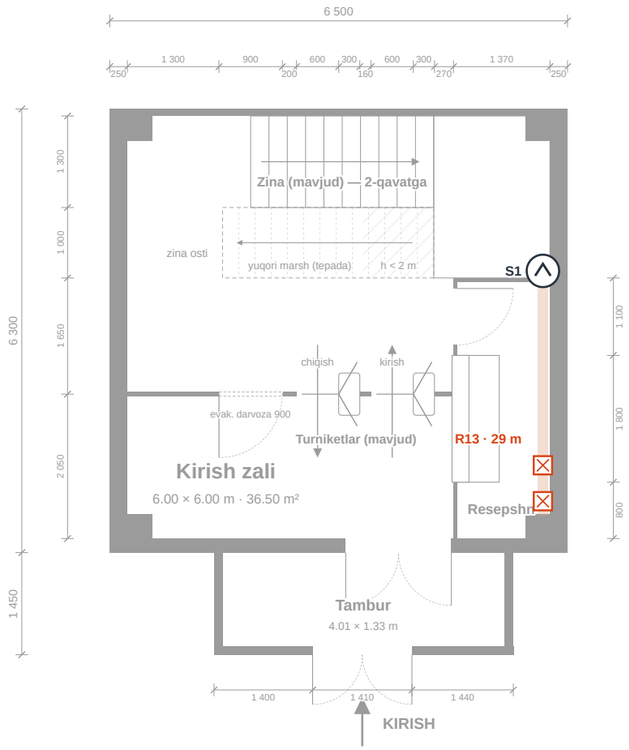

SHIT ShR — BIR CHIZIQLI SXEMA (mavjud shit, 6-xona)

kirish 3F ~380 V (mavjud), bosh avtomat ≥ 63 A



ELEKTR — SHIT GURUHLARI (mavjud ShR, 6-xona)

Guruh	Iste'molchi	Avtomat	Kabel	kW	m
R1	1-xona	C16, 30 mA (difavtomat)	3×2.5	2.0	36
R2	2-xona	C16, 30 mA (difavtomat)	3×2.5	2.0	43
R3	3-xona	C16, 30 mA (difavtomat)	3×2.5	2.0	50
R4	4-xona	C16, 30 mA (difavtomat)	3×2.5	2.0	49
R5	5-xona	C16, 30 mA (difavtomat)	3×2.5	2.0	53
R6	6-xona	C16, 30 mA (difavtomat)	3×2.5	2.0	46
R7	7-xona	C16, 30 mA (difavtomat)	3×2.5	2.0	40
R8	call-markaz (+ tarmoq shkafi)	C16, 30 mA (difavtomat)	3×2.5	2.0	25
R9	ustozlar	C16, 30 mA (difavtomat)	3×2.5	1.5	25
R10	sotuv	C16, 30 mA (difavtomat)	3×2.5	1.0	35
R11	admin	C16, 30 mA (difavtomat)	3×2.5	1.0	41
R12	koworking, CEO	C16, 30 mA (difavtomat)	3×2.5	2.0	66
R13	1-qavat resepshn	C16, 30 mA (difavtomat)	3×2.5	0.5	29
Y1	1-xona	C10	3×1.5	0.2	33
Y2	2-xona	C10	3×1.5	0.2	39
Y3	3-xona	C10	3×1.5	0.2	41
Y4	4-xona	C10	3×1.5	0.2	48
Y5	5-xona	C10	3×1.5	0.2	50
Y6	6-xona	C10	3×1.5	0.2	43
Y7	7-xona	C10	3×1.5	0.2	36
Y8	xizmat xonalari (XZ1–XZ4)	C10	3×1.5	0.4	80
Y9	koridorlar, kanopi, logotiplar, yashil LED	C10	3×1.5	1.5	63
Y10	koworking, kirish zali, CEO, WC tamburi, 6-xona	C10	3×1.5	0.6	62
KK1	tashqi blok (tomda) + ichki blok	3P C25	5×4	10	27
KK2	tashqi blok (tomda) + ichki blok	3P C25	5×4	10	37
VV1	vitechka ventilyatori	C10	3×1.5	0.4	23
—	zaxira (2 ta)	C16			
Jami	**o'rnatilgan quvvat**			**46.4**	

Kabel va materiallar (2- va 1-qavat)

Nomi	m
VVGng-LS 3×2.5 (rozetkalar)	**538**
VVGng-LS 3×1.5 (yoritish, VV1)	**517**
VVGng-LS 5×4 (KK1, KK2)	**64**
Kuch lotogi (shift ostida, 100 mm) — koridorlar va koworking	53

Diqqat: o'rnatilgan quvvat ~46 kW (shundan konditsionerlar 20 kW) — mavjud shit va kirish kabelining quvvati (3 faza, avtomat ≥ 63 A) tekshirilsin; shitda 28 ta guruh uchun joy bo'lmasa, yoniga 36 modulli qo'shimcha quti. Har sinf rozetkasi — alohida difavtomat (30 mA).

- 1-qavat resepshn: 2 rozetka (R13) — 2-qavat shitidan, asosiy zina bo'ylab (S1).
- 3-qavat elektri mavjud (buyurtmachi) — chizilmaydi.

PDP Academy · Xadra filiali	
Chizma	**Elektr — shit guruhlari, 1-qavat**
Ish chizmasi — ustalar uchun. Qurilmalar joyi — buyurtmachi belgilagan (18.10). Toshkent sh., Xadra — 1- va 2-qavat	
Masshtab: ~1:90 · Sana: 18.10.2026 · Versiya: v1.2 · Varaq: 3 / 3	
Bajardi: _____ Tekshirdi: _____	