


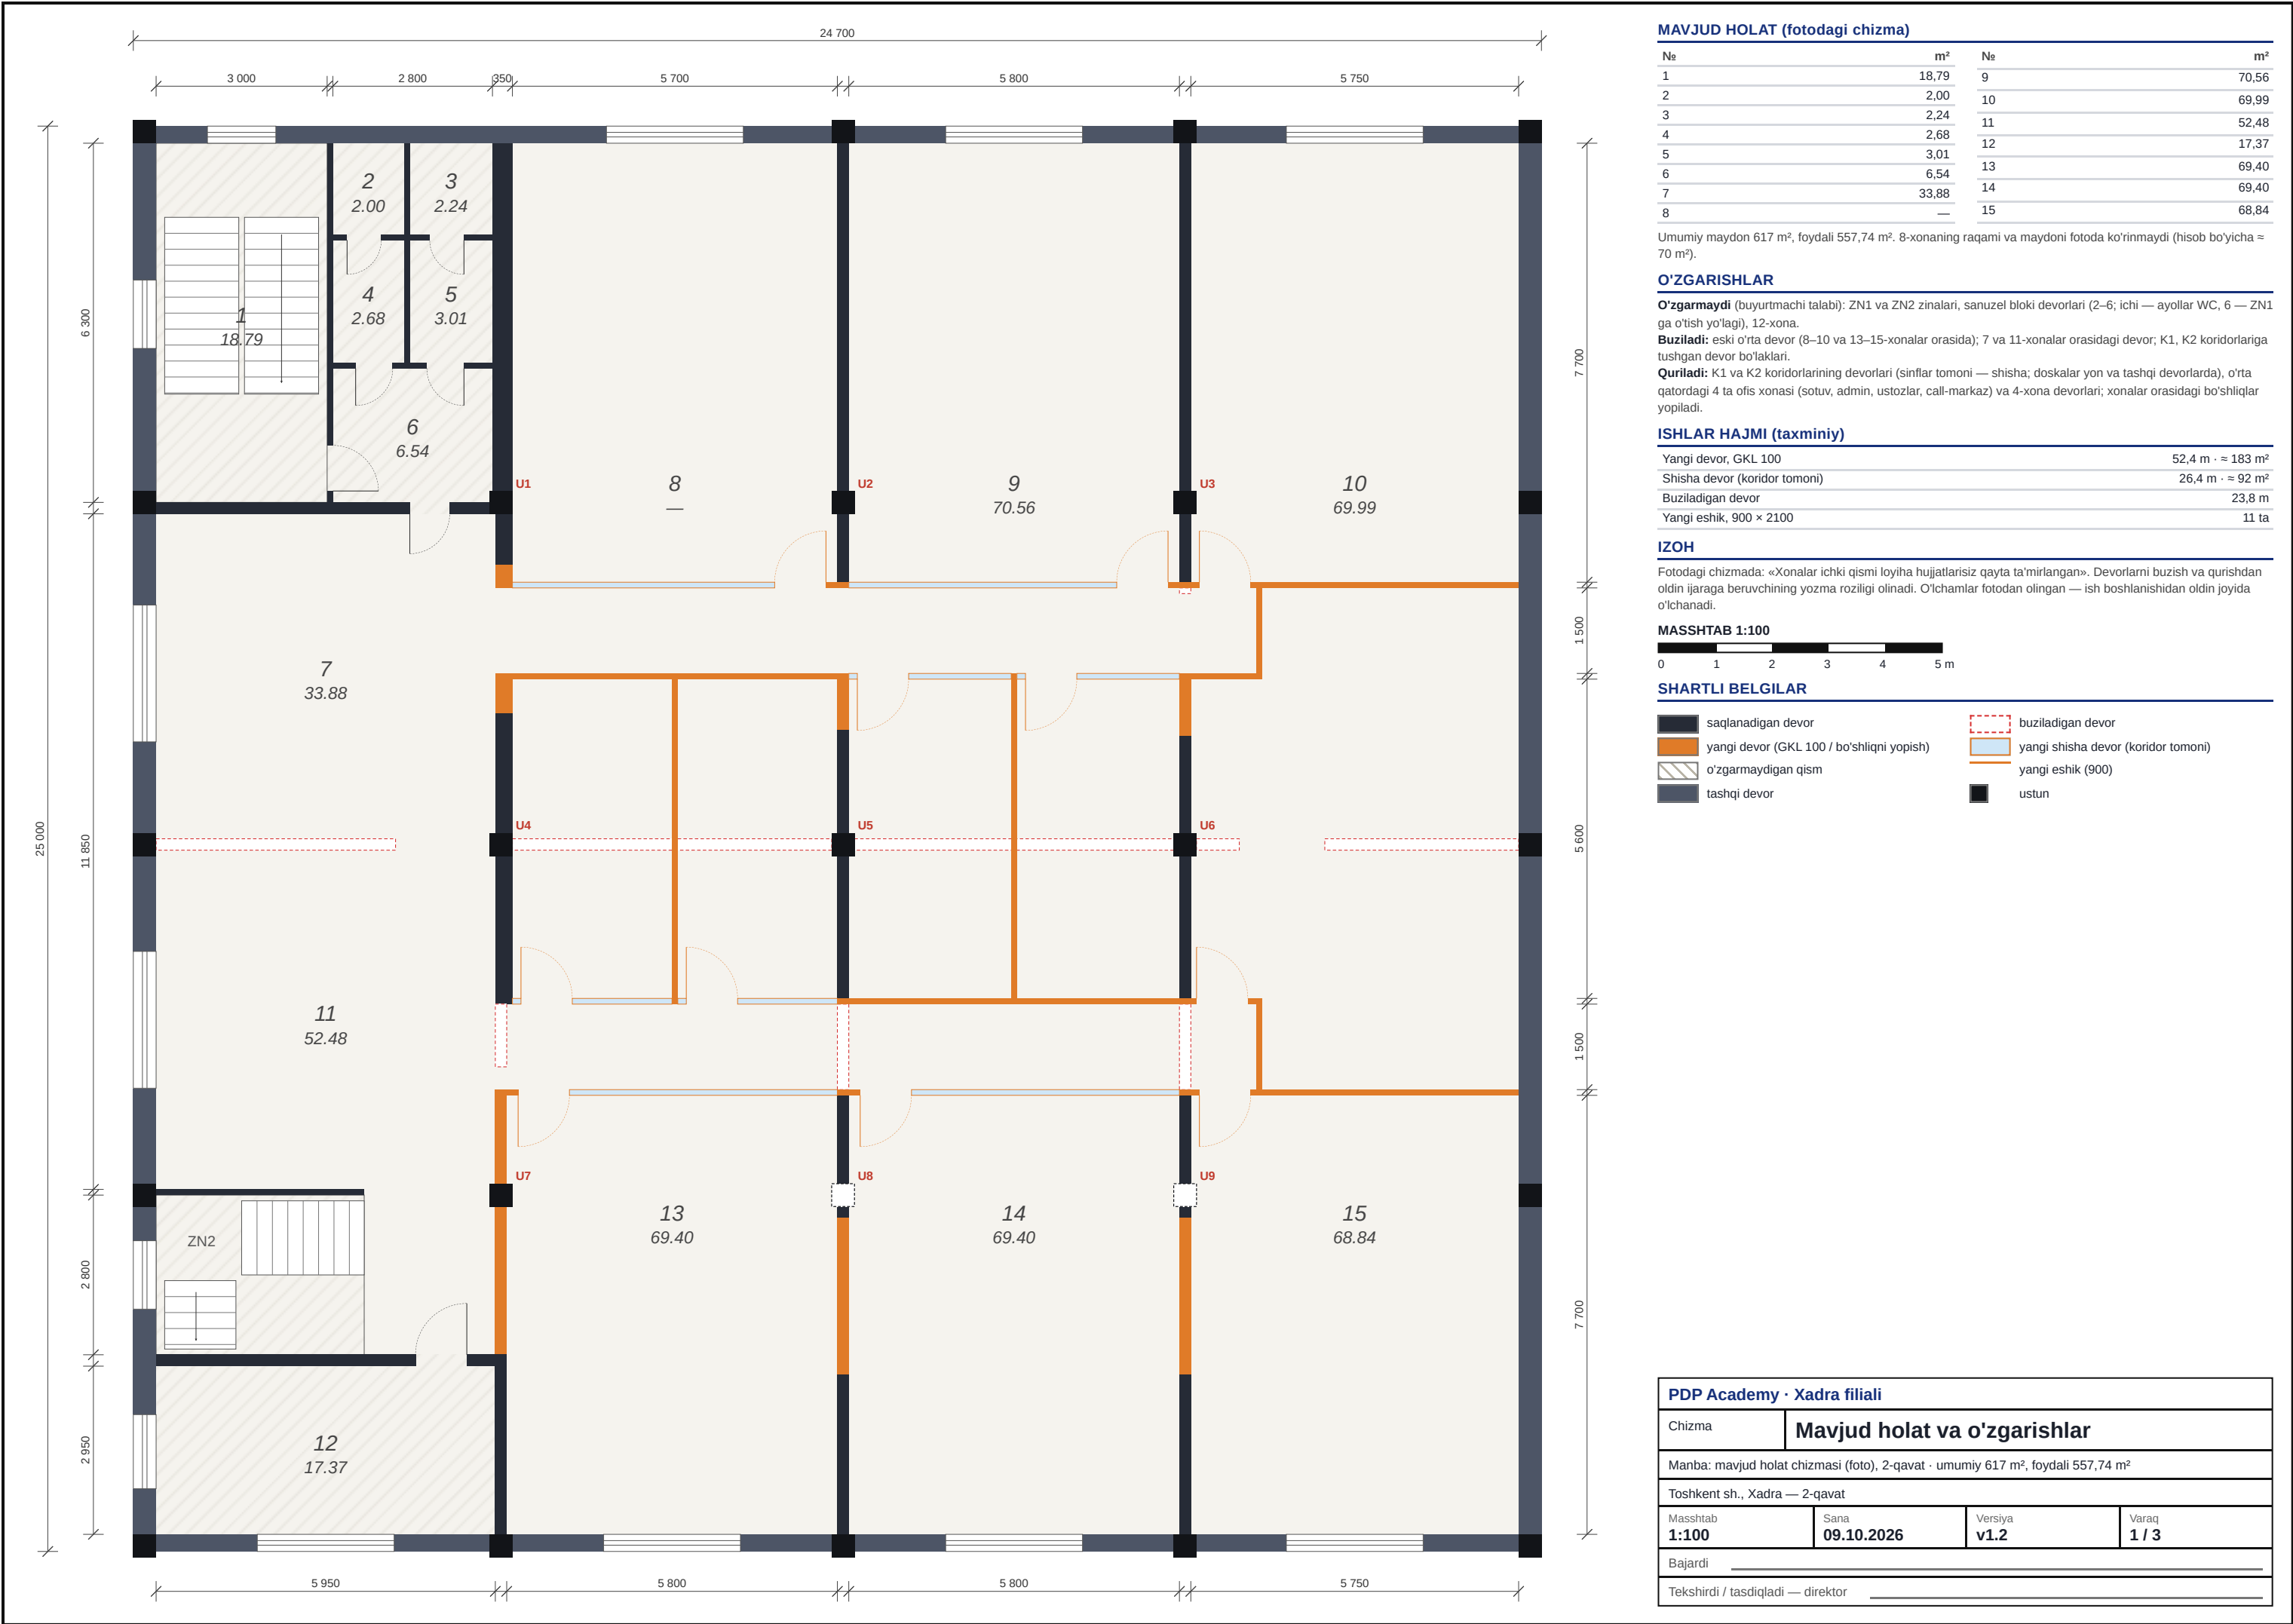

MAVJUD HOLAT (fotodagi chizma)

№	m²	№	m²
1	18,79	9	70,56
2	2,00	10	69,99
3	2,24	11	52,48
4	2,68	12	17,37
5	3,01	13	69,40
6	6,54	14	69,40
7	33,88	15	68,84
8	—		

Umumiy maydon 617 m², foydali 557,74 m². 8-xonaning raqami va maydoni fotoda koʻrinmaydi (hisob boʻyicha ≈ 70 m²).

OʻZGARISHLAR

Oʻzgarmaydi (buyurtmachi talabi): ZN1 va ZN2 zinalari, sanuzel bloki devorlari (2–6; ichi — ayollar WC, 6 — ZN1 ga oʻtish yoʻlagi), 12-xona.

Buziladi: eski oʻrta devor (8–10 va 13–15-xonalar orasida); 7 va 11-xonalar orasidagi devor; K1, K2 koridorlariga tushgan devor boʻlaklari.

Quriladi: K1 va K2 koridorlarining devorlari (sinflar tomoni — shisha; doskalar yon va tashqi devorlarda), oʻrta qatordagi 4 ta ofis xonasi (sotuv, admin, ustozlar, call-markaz) va 4-xona devorlari; xonalar orasidagi boʻshliqlar yopiladi.


ISHLAR HAJMI (taxminiy)

Yangi devor, GKL 100	52,4 m · ≈ 183 m²
Shisha devor (koridor tomoni)	26,4 m · ≈ 92 m²
Buziladigan devor	23,8 m
Yangi eshik, 900 × 2100	11 ta

IZOH

Fotodagi chizmada: «Xonalar ichki qismi loyiha hujjatlarisiz qayta taʼmirlangan». Devorlarni buzish va qurishdan oldin ijaraga beruvchining yozma roziligi olinadi. Oʻlchamlar fotodan olingan — ish boshlanishidan oldin joyida oʻlchanadi.

MASSHTAB 1:100

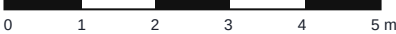

SHARTLI BELGILAR

	saqlanadigan devor		buziladigan devor
	yangi devor (GKL 100 / boʻshliqni yopish)		yangi shisha devor (koridor tomoni)
	oʻzgarmaydigan qism		yangi eshik (900)
	tashqi devor		ustun

PDP Academy · Xadra filiali

Chizma Mavjud holat va oʻzgarishlar

Manba: mavjud holat chizmasi (foto), 2-qavat · umumiy 617 m², foydali 557,74 m²

Toshkent sh., Xadra — 2-qavat

Mashtab 1:100	Sana 09.10.2026	Versiya v1.2	Varaq 1 / 3
------------------	--------------------	-----------------	----------------

Bajardi

Tekshirdi / tasdiqladi — direktor



MAYDON	
Ichki gabarit	23 900 × 24 400
Umumiy maydon (hujjat)	617 m²
Foydali maydon (hujjat)	557,74 m²
O'quv xonalari, 7 ta · 164 o'rin	312,6 m²
Offline sotuv (XZ1) va admin (XZ2)	31,3 m²
Ustozlar (XZ3), call-markaz (XZ4)	31,8 m²
Koworking / tadbirlar zali (KW)	70,5 m²
CEO xonasi (12-xona, o'zgarmaydi)	17,6 m²
Koridorlar K1, K2 va kirish zali ZL	46,7 m²
Zinalar, ayollar WC va o'tish yo'lagi (devorlari o'zgarmaydi)	45,8 m²
Balandlik (poldan shiftgacha)	3500 mm (buyurtmachi)


XONALAR					
Xona	O'lcham, m	m²	O'rin	m²/kishi	Partalar
SR1 · 1-xona	7.70 × 5.70	43,9	24	1,8	4+4+4
SR2 · 2-xona	7.70 × 5.80	44,6	24	1,9	4+4+4
SR3 · 3-xona	7.70 × 5.75	44,2	24	1,8	4+4+4
SR4 · 4-xona	8.80 × 5.75 (L)	46,6	20	2,3	4+4+2
SR5 · 5-xona	7.70 × 5.75	44,2	24	1,8	4+4+4
SR6 · 6-xona	7.70 × 5.80	44,6	24	1,9	4+4+4
SR7 · 7-xona	7.70 × 5.80	44,6	24	1,9	4+4+4
XZ1 · sotuv	2.80 × 5.60	15,7	2	—	2 stol + 4 mijoz stuli, shisha devor
XZ2 · admin	2.80 × 5.60	15,6	2	—	2 stol + 2 mehmon stuli, shisha devor
XZ3 · ustozlar	2.85 × 5.60	15,9	9	—	umumiy stol, lokerlar
XZ4 · call-markaz	2.85 × 5.60	15,9	6	—	devor bo'ylab 6 ish o'rni
CEO (12-xona)	5.95 × 2.95	17,6	1	—	ish stoli + 4 kishilik stol, derazali
KW	5.95 × 11.85	70,5	~35	—	koworking; sahna — XZ1 devori, tadbirda 68 o'rin
Jami		312,6	164		6 × 24 + 1 × 20

USTUNLAR — MAVJUD				
Kod	O'q	X	Y	O'lcham
U1	2-B	6 050	6 300	400 × 400
U2	3-B	12 050	6 300	400 × 400
U3	4-B	18 050	6 300	400 × 400
U4	2-C	6 050	12 300	400 × 400
U5	3-C	12 050	12 300	400 × 400
U6	4-C	18 050	12 300	400 × 400
U7	2-D	6 050	18 450	400 × 400
U8	3-D	12 050	18 450	400 × 400 *
U9	4-D	18 050	18 450	400 × 400 *

Koordinata — ichki yuzaning yuqori-chap burchagidan, ustun markazi bo'yicha; o'qlar taxmini. * U8, U9 fotoda ko'rinmaydi — to'r bo'yicha qo'yilgan (devor ichida), joyida tekshirilsin.

PARTA TO'RI (Xadra filiali)

parta 1400 × 600 (2 kishiilik) · stul 380 × 420
qatorda 4 parta (8 o'rin) · yo'lak 600 · deraza tomondagi devorgacha 200
3 qator · oldid 1 300 (parta 600 × stul va o'tish 700)
doskadan 1-partagacha 1 850 · oxirgi parta 5 050 · sig'im 24
ISTISNO: SR3 — doska va ustoz joyi kirish tomonida (buyurtmachi), deraza o'quvchilarning o'ng tomonida; SR4 — 4 + 4 + 2 parta, 20 o'rin (doska o'ng tashqi devorda)
Beruniy standart: parta 690 × 500 (1 kishiilik), 2 + 2 + 2 × 4 qator, qadam 1 300, doskadan 2 440, oxirgi 6 840
ustundan: oldid/orqa 500 · yon 0. Doska 3000 yon (kar) devorda, deraza o'quvchilarning chap tomonida (SR3 dan tashqari); eshiklar 900.
K1, K2 koridorlar 1500. Yangi devorlar — GKL 100; sinflarning koridor tomoni — akustik shisha.
KW: o'ng tomonda —1,6 m o'tish yo'lagi bo'sh (6-xona — ZN1 ga o'tish, K1, K2, kirish zali); sahna — XZ1 devorda, podiumsiz.
Ayollar WC: 2 kabina eng ichkarida (2, 3 — unitaz), oldida tambur (4, 5 — rakovina); ikki eshik orqali kiriladi.
Ofis xonalari (XZ1—XZ4): eshik tomoni shisha devor; barcha yangi eshiklar shisha.
XZ3 — ustozlar xonasi, XZ4 — call-markaz va online sotuv; 12-xona — CEO (majbud holicha).
Zinalar mavjud holicha; 1-qavatda zina oldida respohn va turniket.

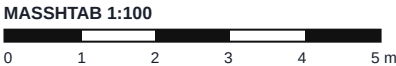

SHARTLI BELGILAR

	kesilgan ichki devor		kesilgan tashqi devor
	mavjud ustun 400 × 400		taxminiy ustun (fotoda yo'q)
	deraza (joiyi taxminiyy)		parta 1400 × 600 (2 kishilik)
	stul 380 × 420		doska (kar devorda)
	o'qituvchi / xodim stoli		shisha devor (koridor tomoni)
	yorituvchi logotip (koridor oxiri, GKL devor)		e'lonlar doskasi
	e'tirof doskasi (faxriylar, oy o'quvchisi)		koworking sahnsi (XZ1 devori): logotip, ekran, reyka

PDP Academy · Xadra filiali			
Chizma	Jihozlash rejası		
Manba: mavjud holat chizması (foto), 2-qavat · umumiy 617 m², foydali 557,74 m²			
Toshkent sh., Xadra — 2-qavat			
Mashtab	Sana	Versiya	Varag
1:100	09.10.2026	v1.2	2 / 3

PDP Academy · Xadra filiali			
Chizma	Havo almashinuvi sxemasi		
Manba: mavjud holat chizmasi (foto), 2-qavat · umumiy 617 m², foydali 557,74 m²			
Toshkent sh., Xadra — 2-qavat			
Masstab 1:100	Sana 09.10.2026	Versiya v1.2	Varaq 3 / 3
Bajardi _____			
Tekshirdi / tasdiqladi — direktor _____			