


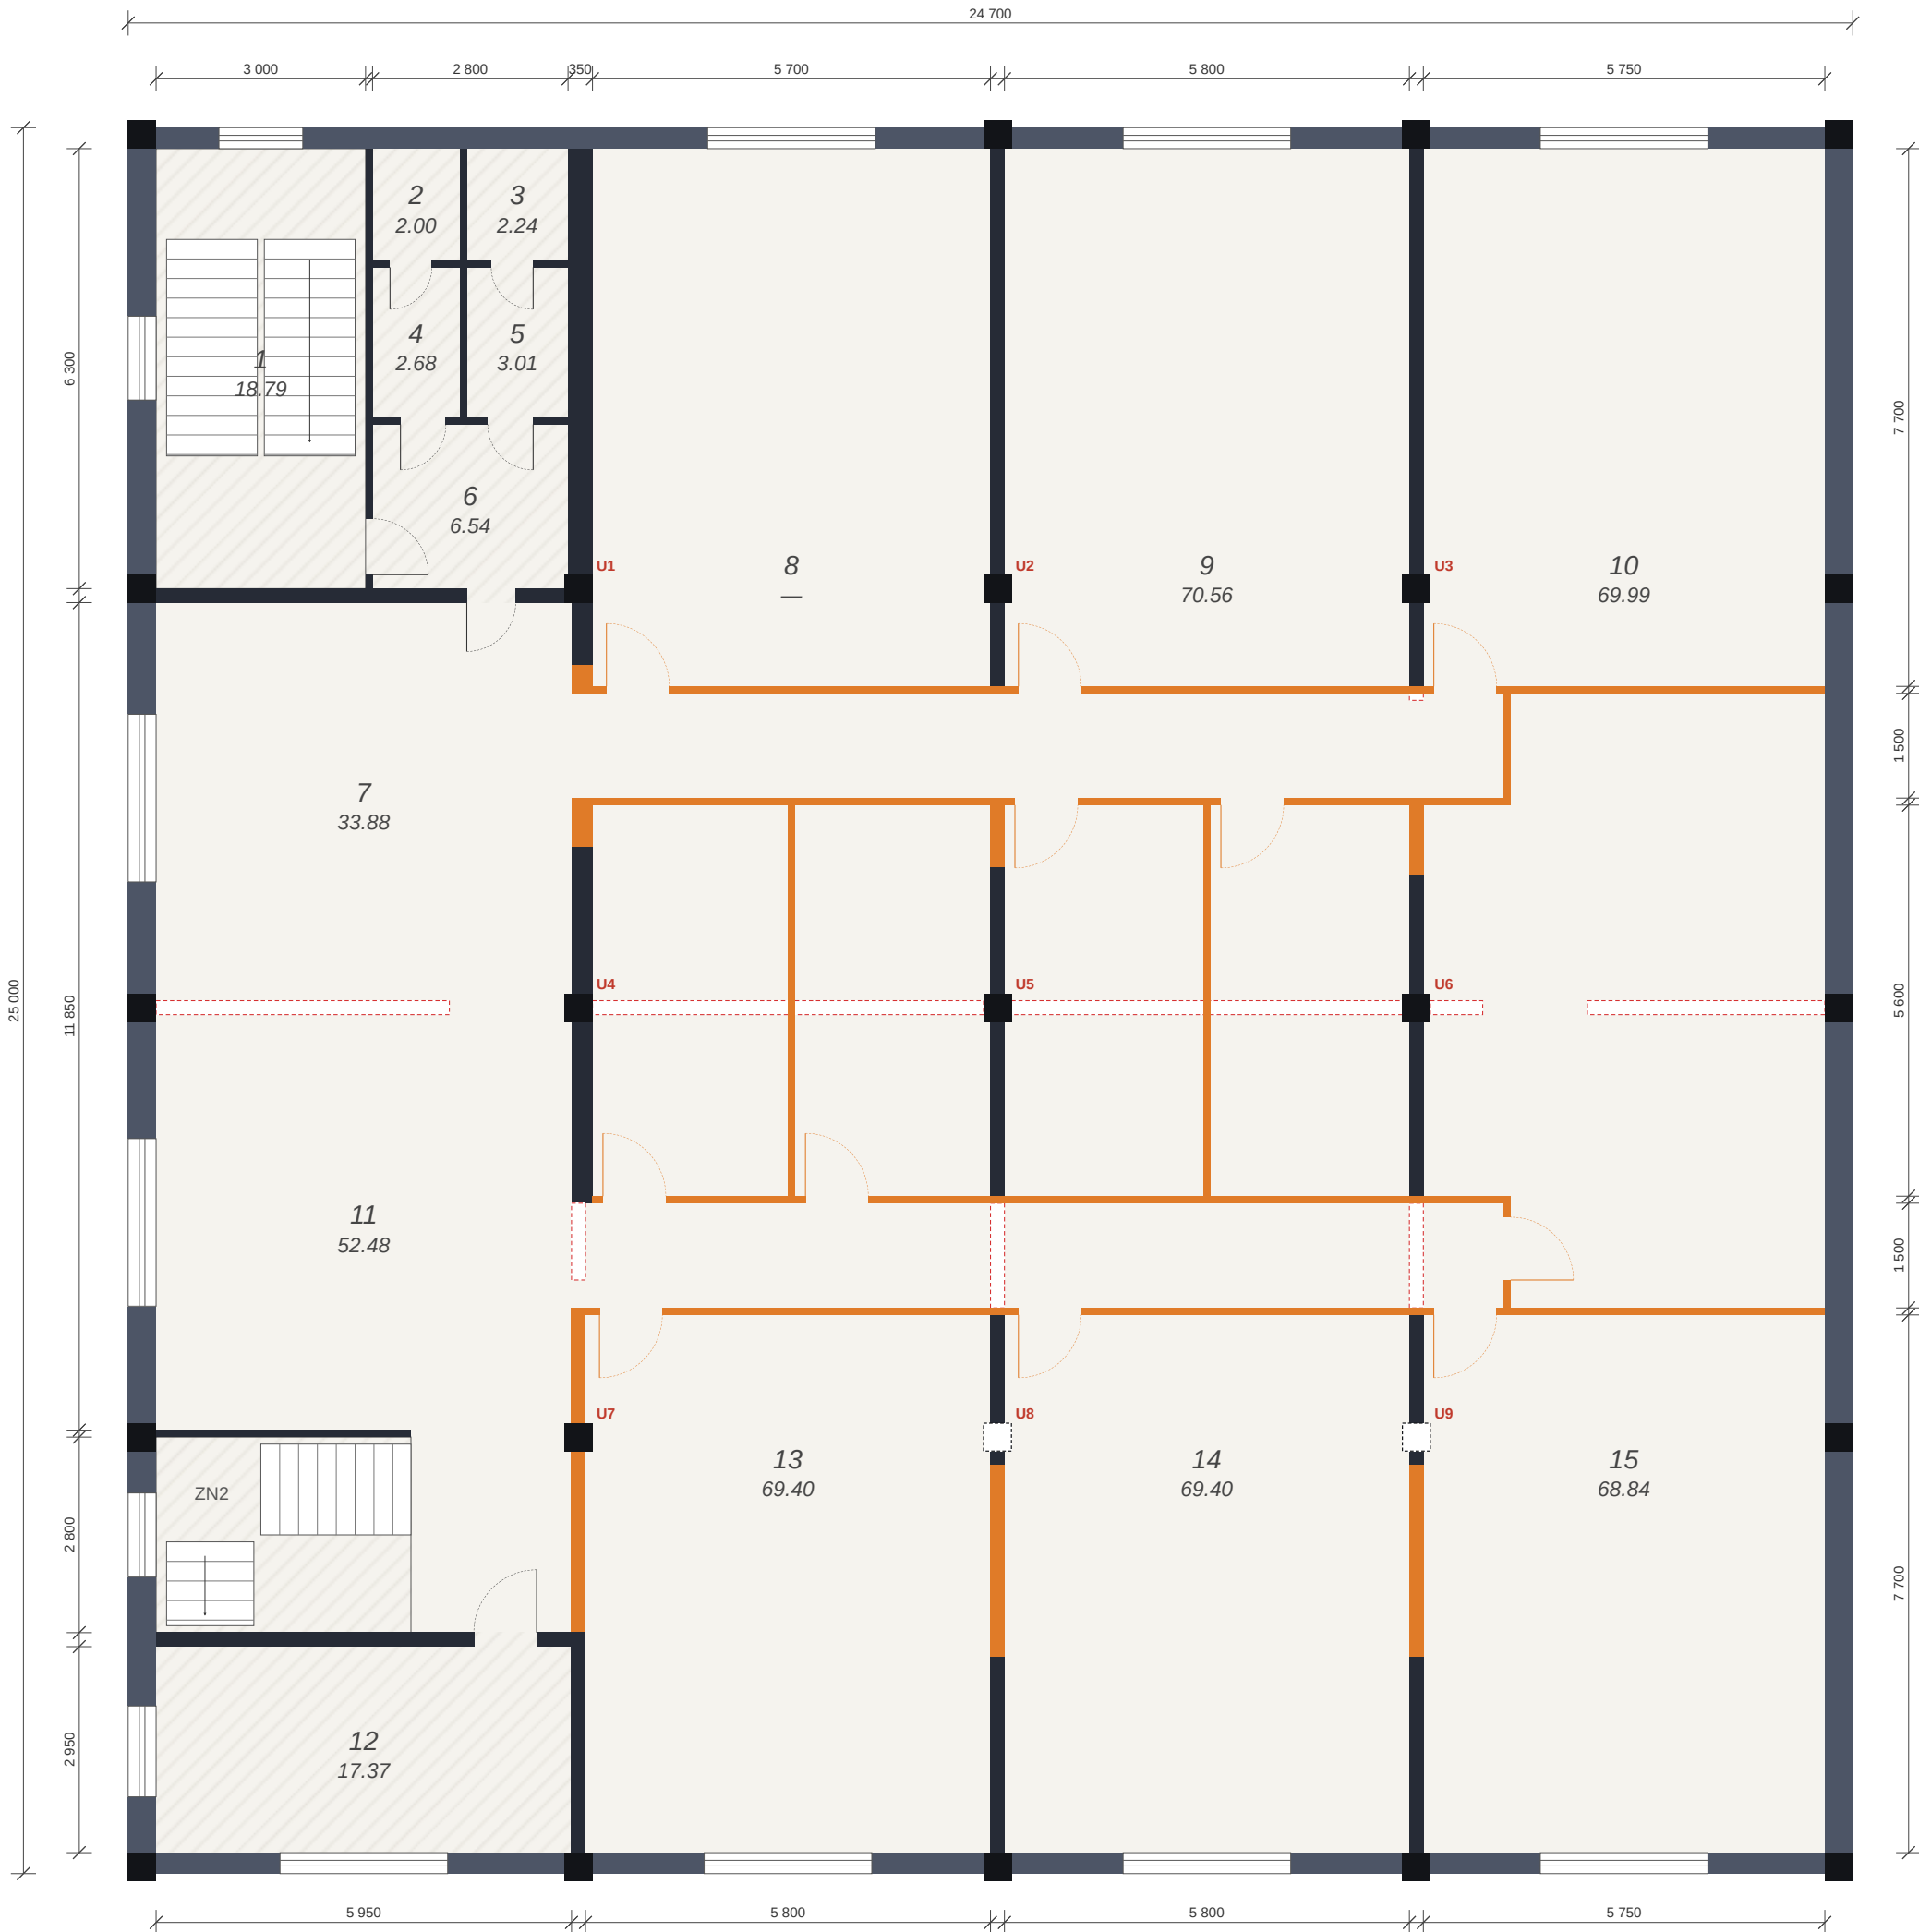

MAVJUD HOLAT (fotodagi chizma)			
№	m²	№	m²
1	18,79	9	70,56
2	2,00	10	69,99
3	2,24	11	52,48
4	2,68	12	17,37
5	3,01	13	69,40
6	6,54	14	69,40
7	33,88	15	68,84
8	—		

Umumiy maydon 617 m², foydali 557,74 m². 8-xonaning raqami va maydoni fotoda koʻrinmaydi (hisob boʻyicha ≈ 70 m²).

O'ZGARISHLAR

O'zgarmaydi (buyurtmachi talabi): ZN1 va ZN2 zinalari, sanuzel bloki (2–6), 12-xona.
Buziladi: eski o'rta devor (8–10 va 13–15-xonalar orasida); 7 va 11-xonalar orasidagi devor; K1, K2 koridorlariga tushgan devor bo'laklari.
Quriladi: K1 va K2 koridorlarining devorlari (1–3 va 5–7-xonalarining doskalari shu devorlarda), 4 ta xizmat xonasi va 4-xona devorlari; xonalar orasidagi bo'shliqlar yopiladi.

ISHLAR HAJMI (taxminiy)

Yangi devor, GKL 100	78,8 m · ≈ 236 m²
Buziladigan devor	23,8 m
Yangi eshik, 900 × 2100	11 ta

IZOH

Fotodagi chizmada: «Xonalar ichki qismi loyiha hujjatlarisiz qayta ta'mirlangan». Devorlarni buzish va qurishdan oldin ijaraga beruvchining yozma roziligi olinadi. O'lchamlar fotodan olingan — ish boshlanishidan oldin joyida o'lchanadi.

MASSHTAB 1:100



SHARTLI BELGILAR

- saqlanadigan devor
- yangi devor (GKL 100 / bo'shliqni yopish)
- yangi eshik (900)
- ustun
- buziladigan devor
- o'zgarmaydigan qism
- tashqi devor

PDP Academy · Xadra filiali			
Chizma	Mavjud holat va o'zgarishlar		
Manba: mavjud holat chizmasi (foto), 2-qavat · umumiy 617 m², foydali 557,74 m²			
Toshkent sh., Xadra — 2-qavat			
Masshtab 1:100	Sana 25.09.2026	Versiya v1.0	Varaq 1 / 3
Bajardi _____			
Tekshirdi / tasdiqladi — direktor _____			





Havo almashinuvi — XONALAR BO'YICHA						
Xona	Odam	Havo, m³/soat	Hajm, m³	Marta / soat	Sovutish, kVt	Qurilma
SR1	25	750	132	5,7	8,0	PV-1
SR2	25	750	134	5,6	8,0	PV-2
SR3	25	750	133	5,7	8,0	PV-3
SR4	21	630	140	4,5	6,0	PV-4
SR5	25	750	133	5,7	8,0	PV-5
SR6	25	750	134	5,6	8,0	PV-6
SR7	25	750	134	5,6	8,0	PV-7
XZ1–XZ4	16	480	189	2,5	6,5	PV-9
KW (tadbir)	70	2 100	211	9,9	17,0	PV-8
Jami		7 710			77,5	

HISOB ASOSI

30 m³/soat har bir kishiga (o'quvchilar + o'qituvchi). Bir kishi soatiga ~18 l CO₂ chiqaradi: 18 l ÷ (1000 – 420) ppm ≈ 31 m³/soat — xonada CO₂ 1000 ppm dan oshmaydi.

Hajm — toza balandlik 3000 mm (taxmin) bo'yicha. Sovutish — odamlar, noutbuklar, proyektor, yoritish, derazadan quyosh va toza havo (rekuperator FIK 60%) yig'indisi, Toshkent yozi (+40 °C) uchun dastlabki baho.

YECHIM

1–3 va 5–7-xonalar 7,7 m chuqur, deraza orqa devorda: tabiiy shamollatish (~2,5 × H ≈ 7,5 m) deyarli butun xonaga yetadi, lekin qish va yozda derazalar yopiq — har sinfga alohida **PV qurilma** (rekuperatorli, ~750 m³/soat, shovqin ≤ 35 dB(A)), deraza devori yonida shift ichida.

4-xona va xizmat xonalarida deraza yo'q — mexanik ventilyatsiya va konditsioner majburiy. O'ng devor qo'shni bino bilan umumiy, orqasida tor oraliq bor: PV-4 panjaralari shu oraliqqa chiqariladi — kirish va chiqish bir-biridan uzoq (7 m), oraliq eni joyida o'lchanadi; havo turg'un bo'lsa, kanal K2 shifti orqali fasadga. PV-9 koworking chap devoridan olib, K1 shifti orqali XZ1–XZ4 ga beradi.

KW: derazalar chap devorda; tadbirida ~70 kishi — PV-8 ~2 100 m³/soat.

Toza havo doska tomonga beriladi, orqa tomondan so'riladi. CO₂ datchigi bilan boshqariladi; bo'sh xona o'chadi. Har sinfga 2 ta KD (kasseta yoki kanalli).

V-1: sanuzel chiqarish ventilyatsiyasi 4 × 50 = 200 m³/soat — mavjud shaxtani tekshirish. Tutun chiqarish talabini yong'in xavfsizligi mutaxassisi belgilaydi.



- SHARTLI BELGILAR**
- PV — rekuperatorli kiritish-chiqarish qurilmasi (shift ichida)
 - toza havo diffuzori
 - fasad panjarasi: toza havo kirishi
 - KD — konditsioner ichki bloki
 - CO₂ datchigi
 - toza havo kanali
 - so'rish panjarasi
 - fasad panjarasi: iflos havo chiqishi
 - xonadagi havo oqimi

PDP Academy · Xadra filiali			
Chizma	Havo almashinuvi sxemasi		
Manba: mavjud holat chizmasi (foto), 2-qavat · umumiy 617 m², foydali 557,74 m²			
Toshkent sh., Xadra — 2-qavat			
Masshtab 1:100	Sana 25.09.2026	Versiya v1.0	Varaq 3 / 3
Bajardi _____			
Tekshirdi / tasdiqladi — direktor _____			