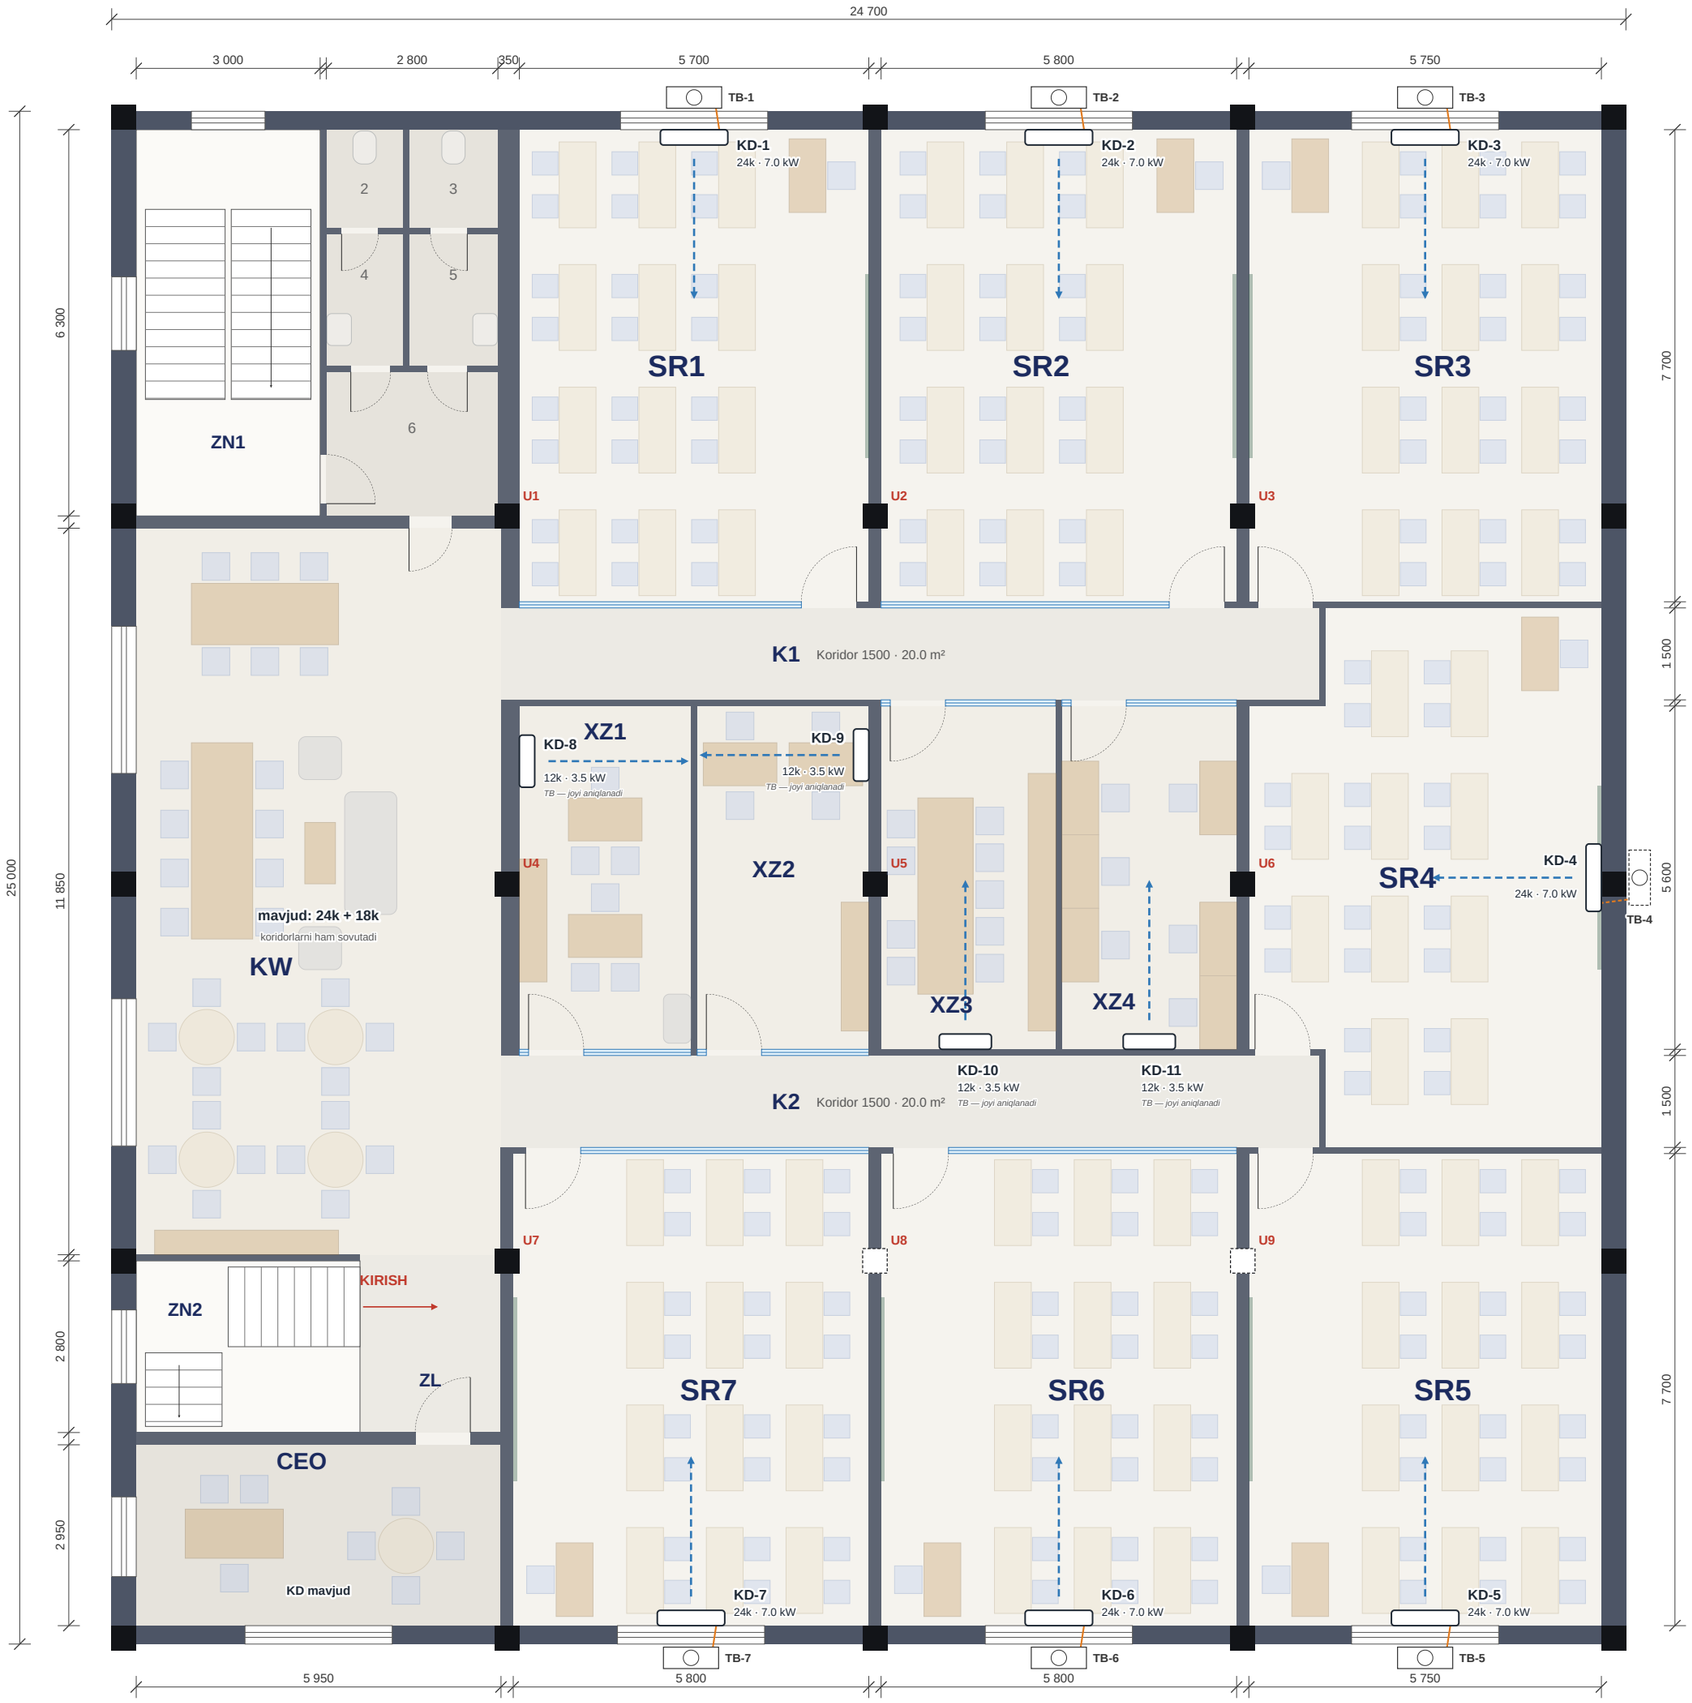


KONDITSIONERLAR (SPLIT, DEVORGA)

Kod	Xona	BTU	Ichki blok	Tashqi blok (TB)	Trassa	Elektr
KD-1	SR1	24k	deraza ustida, tashqi devorda	fasadda, deraza tokchasi ostida	3–4 m	3×2.5 mm², 20 A
KD-2	SR2	24k	deraza ustida, tashqi devorda	fasadda, deraza tokchasi ostida	3–4 m	3×2.5 mm², 20 A
KD-3	SR3	24k	deraza ustida, tashqi devorda	fasadda, deraza tokchasi ostida	3–4 m	3×2.5 mm², 20 A
KD-4	SR4	24k	o'ng devorda, doska ustida	o'ng devor ortidagi oraliqda yoki tomda	3–8 m	3×2.5 mm², 20 A
KD-5	SR5	24k	deraza ustida, tashqi devorda	fasadda, deraza tokchasi ostida	3–4 m	3×2.5 mm², 20 A
KD-6	SR6	24k	deraza ustida, tashqi devorda	fasadda, deraza tokchasi ostida	3–4 m	3×2.5 mm², 20 A
KD-7	SR7	24k	deraza ustida, tashqi devorda	fasadda, deraza tokchasi ostida	3–4 m	3×2.5 mm², 20 A
KD-8	XZ1	12k	ichki devorda	tomda (xona ustida) yoki koworking fasadida	4–6 m (tom) / 10–20 m (fasad)	3×1.5 mm², 16 A
KD-9	XZ2	12k	ichki devorda	tomda (xona ustida) yoki koworking fasadida	4–6 m (tom) / 10–20 m (fasad)	3×1.5 mm², 16 A
KD-10	XZ3	12k	ichki devorda	tomda (xona ustida) yoki koworking fasadida	4–6 m (tom) / 10–20 m (fasad)	3×1.5 mm², 16 A
KD-11	XZ4	12k	ichki devorda	tomda (xona ustida) yoki koworking fasadida	4–6 m (tom) / 10–20 m (fasad)	3×1.5 mm², 16 A
—	KW	24k + 18k	mavjud, joyi o'zgarmaydi; koridorlarni ham sovutadi			
—	CEO	—	mavjud			

O'RNATISH

Sinflar: ichki blok deraza ustida, o'rtada: pastki qirrasi 2.75 m da (deraza tepasi ~2.6 m, shiftgacha ≥ 0.15 m) — havo deraza tomondan koridor tomonga, o'quvchilar ustidan. Tashqi blok fasadda, deraza tokchasi ostida, kronshteynda — xizmat derazadan. Trassa va drenaj blok yonidagi teshikdan (Ø 70) chiqib, fasad bo'ylab qutida pastga tushadi.
SR4: ichki blok o'ng devorda, doska ustida; tashqi blok o'ng devor ortidagi oraliqda (eni yetarli bo'lsa) yoki tomda.
XZ1–XZ4: ichki blok ichki devorda; tashqi blok tomda (xona ustida 3-qavat bo'lmasa) yoki koridor shifti orqali koworking fasadiga — tashqi havo olish panjaralaridan ≥ 3 m uzoqda; drenaj — nishab bilan stoyakka yoki nasos.
Elektr: har bir split — shitdan alohida liniya. Jami ~20 kW (to'liq yuklamada). Detallar — 2-varaq (o'rnatish detallari).

MASSHTAB 1:100

0 1 2 3 4 5 m

SHARTLI BELGILAR

- KD — split ichki bloki (devorda, 2.75 m dan yuqori)
- TB — joyi aniqlanadi (tom yoki oraliq)
- TB — tashqi blok (fasadda, kronshteynda)
- freon trassasi va drenaj (punktir — aniqlanadi)
- sovuq havo oqimi yo'nalishi

PDP Academy · Xadra filiali

Chizma	**Konditsionerlar joylashuvi**
Manba: mavjud holat chizmasi (foto), 2-qavat · umumiy 617 m², foydali 557,74 m²	
Toshkent sh., Xadra — 2-qavat	

Masshtab	Sana	Versiya	Varaq
1:100	**09.10.2026**	**v1.2**	**4 / 4**


Bajardi _____

Tekshirdi / tasdiqladi — direktor _____

Split konditsionerlar — qanday o'rnatiladi (sinf, 24 000 BTU)


v1.2 · 09.10.2026
Joylashuv rejasi — chizmalar to'plamining 4-varag'i

1. Sinf deraza devori — ichkaridan ko'rinish (SR2 misolida, 1:40)

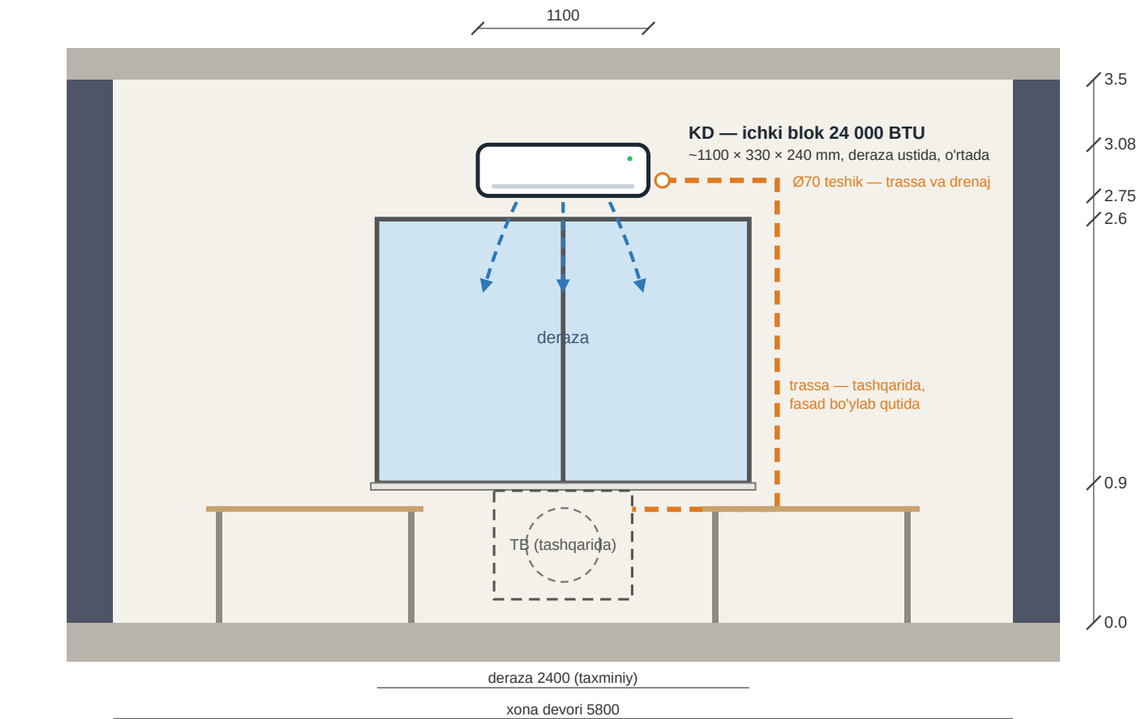

Ichki blok deraza ustida, o'rtada: pastki qirrasi 2.75 m, ustki 3.08 m, shiftgacha ~0.42 m. Deraza tokchasi 0.9 m va tepasi 2.6 m — taxminiy, joyida o'lchanadi; deraza baland bo'lsa, blok deraza yoniga (tashqi devorda) qo'yiladi. Punktir — devor ortida (tashqarida).

2. Kesim: tashqi devor — sinf (1:40)

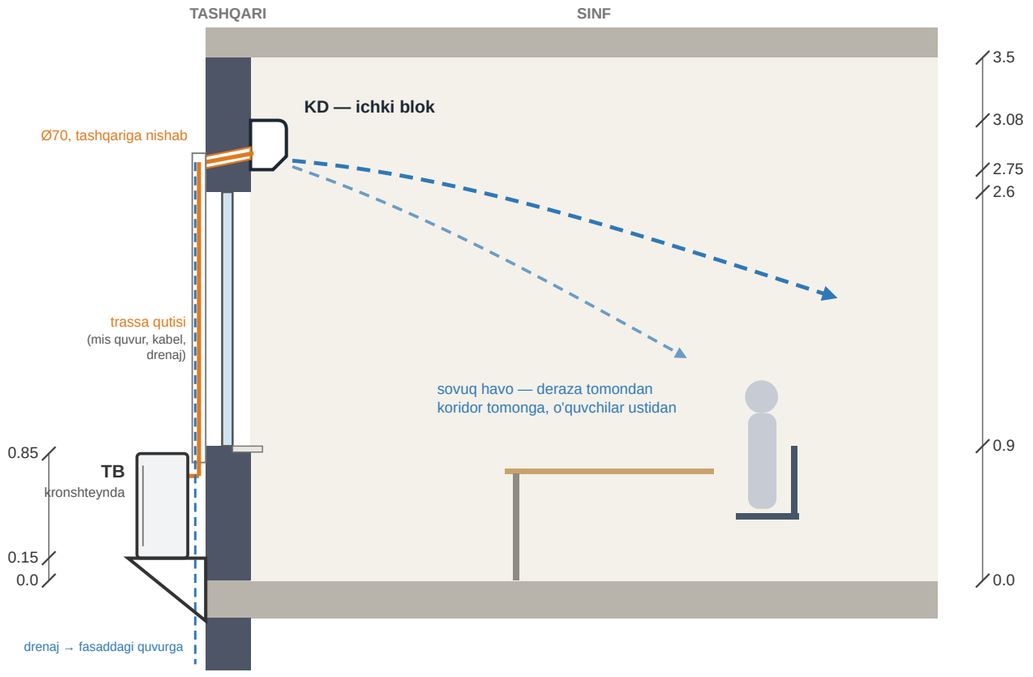

Trassa (mis quvurlar izolyatsiyada, aloqa kabeli) va drenaj blok yonidagi Ø70 teshikdan tashqariga nishab bilan chiqadi, fasad bo'ylab dekorativ qutida pastga tushadi. Tashqi blok deraza tokchasi ostida, kronshteynda — xizmat derazadan. Drenaj fasaddagi umumiy quvurga ulanadi (trotuarga tomizmaydi).

3. 3D: sinf ichidan (SR2) va fasaddan





Chapda — 24 000 BTU ichki blok deraza ustida; o'ngda — tashqi bloklar deraza ostida kronshteynda, trassa deraza yonidagi oq qutida. 1-qavat fasadi shartli.

Qayerda nima turadi (qisqacha)

Xonalar	Ichki blok	Tashqi blok
SR1–SR3, SR5–SR7	deraza ustida, o'rtada, 2.75 m	fasadda, shu deraza ostida (kronshteyn)
SR4	o'ng (sharqiy) devorda, doska ustida	devor ortidagi oraliqda yoki tomda — aniqlanadi
XZ1–XZ4	ichki devorda, 12 000 BTU	tomda yoki koworking fasadida — aniqlanadi
Koworking, CEO	mavjud konditsionerlar, joyi o'zgarmaydi	

Bloklar (taxminiy o'lchamlar — model pasportidan aniqlanadi)

Split	Soni	Ichki blok, mm	Tashqi blok, mm	TB, kg	Elektr liniyasi
24 000 BTU	7	1100 × 330 × 240	890 × 700 × 340	~45	3×2.5 mm², avtomat 20 A
12 000 BTU	4	850 × 290 × 210	780 × 550 × 290	~30	3×1.5 mm², avtomat 16 A

O'rnatish talablari

- **Ichki blok:** shiftgacha ≥ 150 mm, yon devorgacha ≥ 150 mm; havo deraza tomondan koridor tomonga — doska va ustozga to'g'ridan emas, jalyuzi pastga 20–30°. Bitta 24k: 7.0 kW (42–43 °C da ~6.1 kW), sinf yuki 5.1–7.6 kW.
- **Trassa:** sinflarda 3–4 m (ko'pchilik modellar uchun minimum ~3 m); mis quvurlar diametri — pasport bo'yicha, butun uzunligi izolyatsiyada. SR4 va xizmat xonalarida trassa uzunligi tashqi blok joyiga bog'liq (4–20 m), uzun bo'lsa freon qo'shiladi.
- **Drenaj:** Ø16–20 mm, nishab ≥ 1–2%; xizmat xonalarida — shift ichida stoyakka yoki drenaj nasosi bilan.
- **Tashqi blok:** ankerli kronshteyn (≥ 100 kg yuk), devordan 100–150 mm (havo aylanishi uchun); hamma sinflarda bir xil balandlikda va bir xil qutilar bilan — fasad toza ko'rinadi. Koworking fasadidagi rekuperator tashqi havo panjaralaridan ≥ 3 m uzoqda.
- **Elektr:** har bir split — shitdan alohida liniya (jadvaldagi kabel va avtomat), tashqi blokka aloqa kabeli — pasport bo'yicha. 11 ta split to'liq yuklamada ~20 kW.
- **Ruxsat:** fasadga tashqi blok osish — ijaraga beruvchi bilan kelishiladi.