

PDP Academy · Xadra filiali

# 2-qavat rejasi — xonalarga bo'linishi

Masshtab 1:100 (A3) · v1.2 · 17.10.2026

0 1 2 3 4 5 m

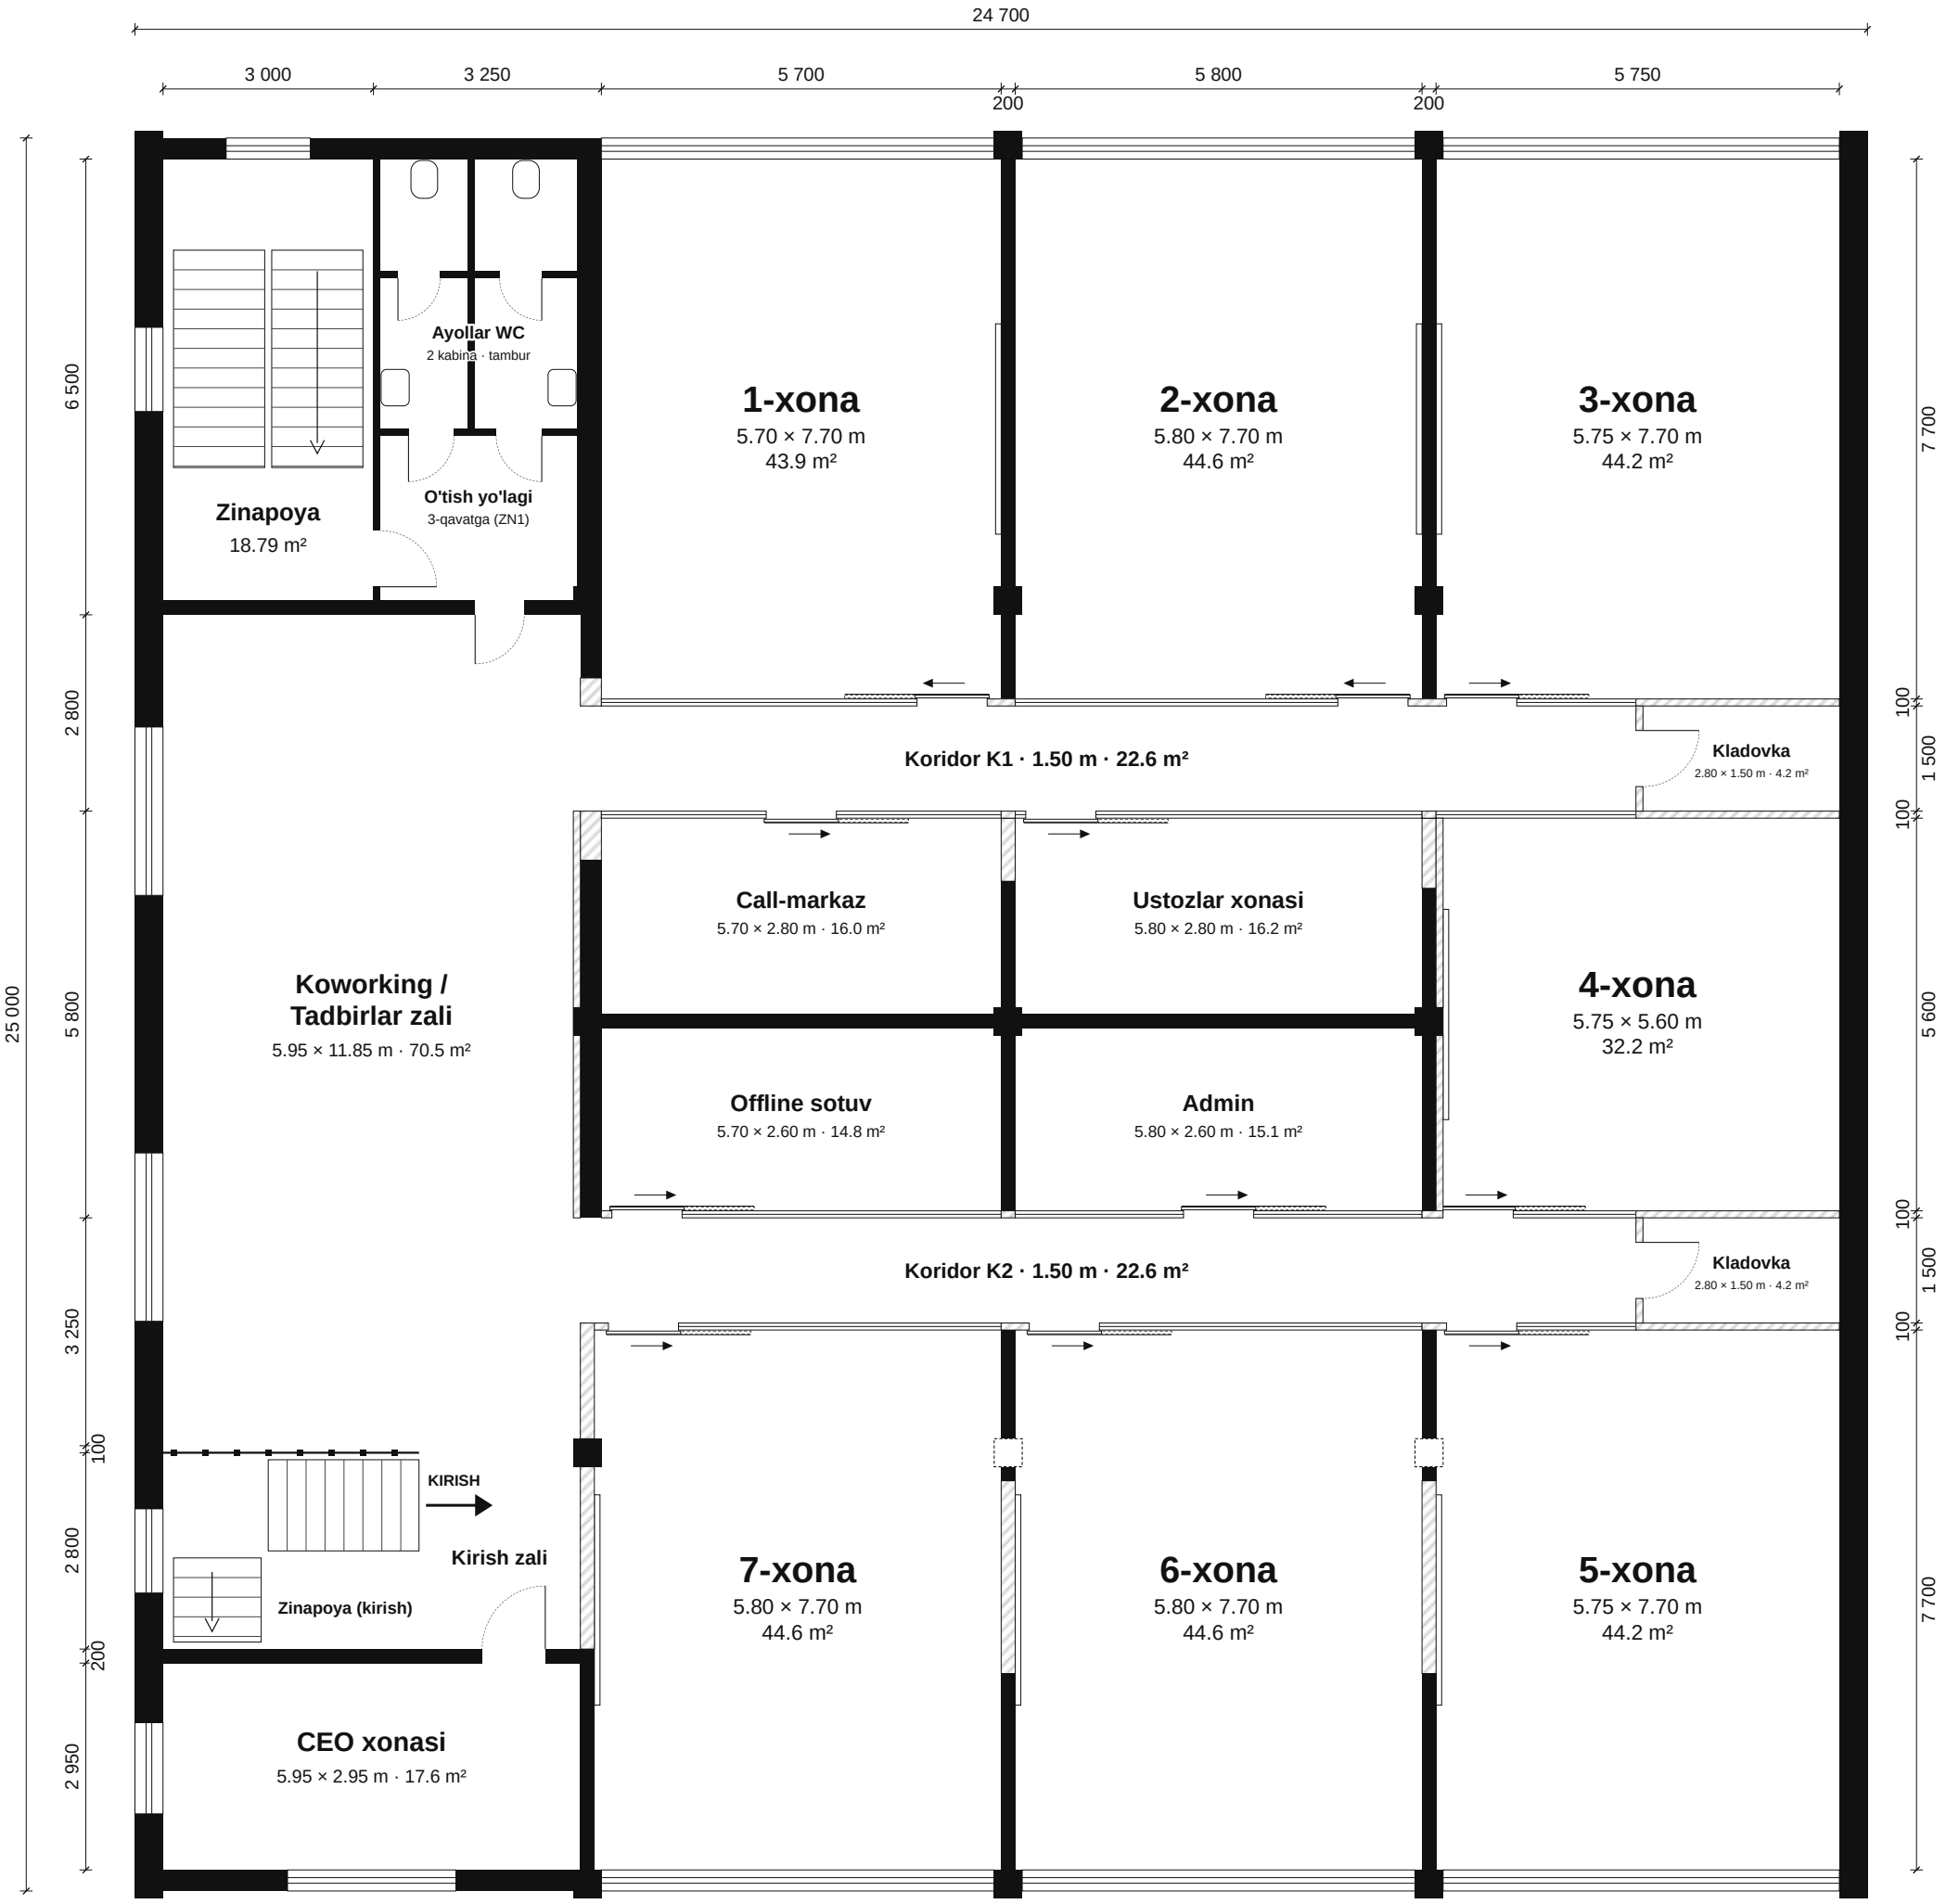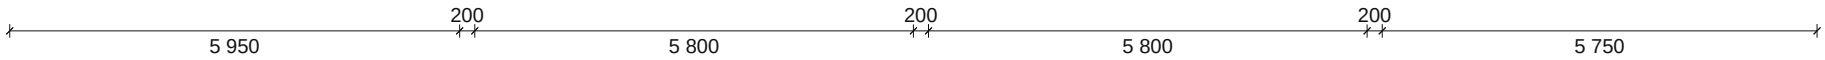


| Xona | Ichki o'lcham | Maydon |
|---|---|---|
| 1-xona | 5.70 × 7.70 m | 43.9 m² |
| 2-xona | 5.80 × 7.70 m | 44.6 m² |
| 3-xona | 5.75 × 7.70 m | 44.2 m² |
| 4-xona | 5.75 × 5.60 m | 32.2 m² |
| 5-xona | 5.75 × 7.70 m | 44.2 m² |
| 6-xona | 5.80 × 7.70 m | 44.6 m² |
| 7-xona | 5.80 × 7.70 m | 44.6 m² |
| Offline sotuv | 5.70 × 2.60 m | 14.8 m² |
| Admin | 5.80 × 2.60 m | 15.1 m² |
| Ustozlar xonasi | 5.80 × 2.80 m | 16.2 m² |
| Call-markaz | 5.70 × 2.80 m | 16.0 m² |
| **O'quv xonalari, jami** | | **298.2 m²** |

| Xona | Ichki o'lcham | Maydon |
|---|---|---|
| Koworking / Tadbirlar zali | 5.95 × 11.85 m | 70.5 m² |
| CEO xonasi | 5.95 × 2.95 m | 17.6 m² |
| K1 koridori | 15.05 × 1.50 m | 22.6 m² |
| K2 koridori | 15.05 × 1.50 m | 22.6 m² |
| Kladovka (K1 oxiri) | 2.80 × 1.50 m | 4.2 m² |
| Kladovka (K2 oxiri) | 2.80 × 1.50 m | 4.2 m² |
| Kirish zali | 2.30 × 2.90 m | 6.6 m² |
| Zinapoyalar, WC, o'tish yo'lagi | | 45.8 m² |
| **Umumiy foydali maydon (hujjat)** | | **557.74 m²** |

## Shartli belgilar va izoh

- mavjud va tashqi devor
- yangi devor — GKL 100
- shisha devor (2.5 m gacha)
- suriladigan eshik 1 m (barg xona ichida)
- ustun

- Ichki o'lcham — devor yuzidan devor yuzigacha, m; maydon ustunlarsiz. Mavjud chizmadan, joyida o'lchanadi.
- Balandlik 3.5 m. Doska — yon devorda (oq to'rtburchak); 4-xonada eshik tomonida, U6 bilan tekis GKL qoplama.
- Kladovka ustida kanalli konditsioner (KK1, KK2).