


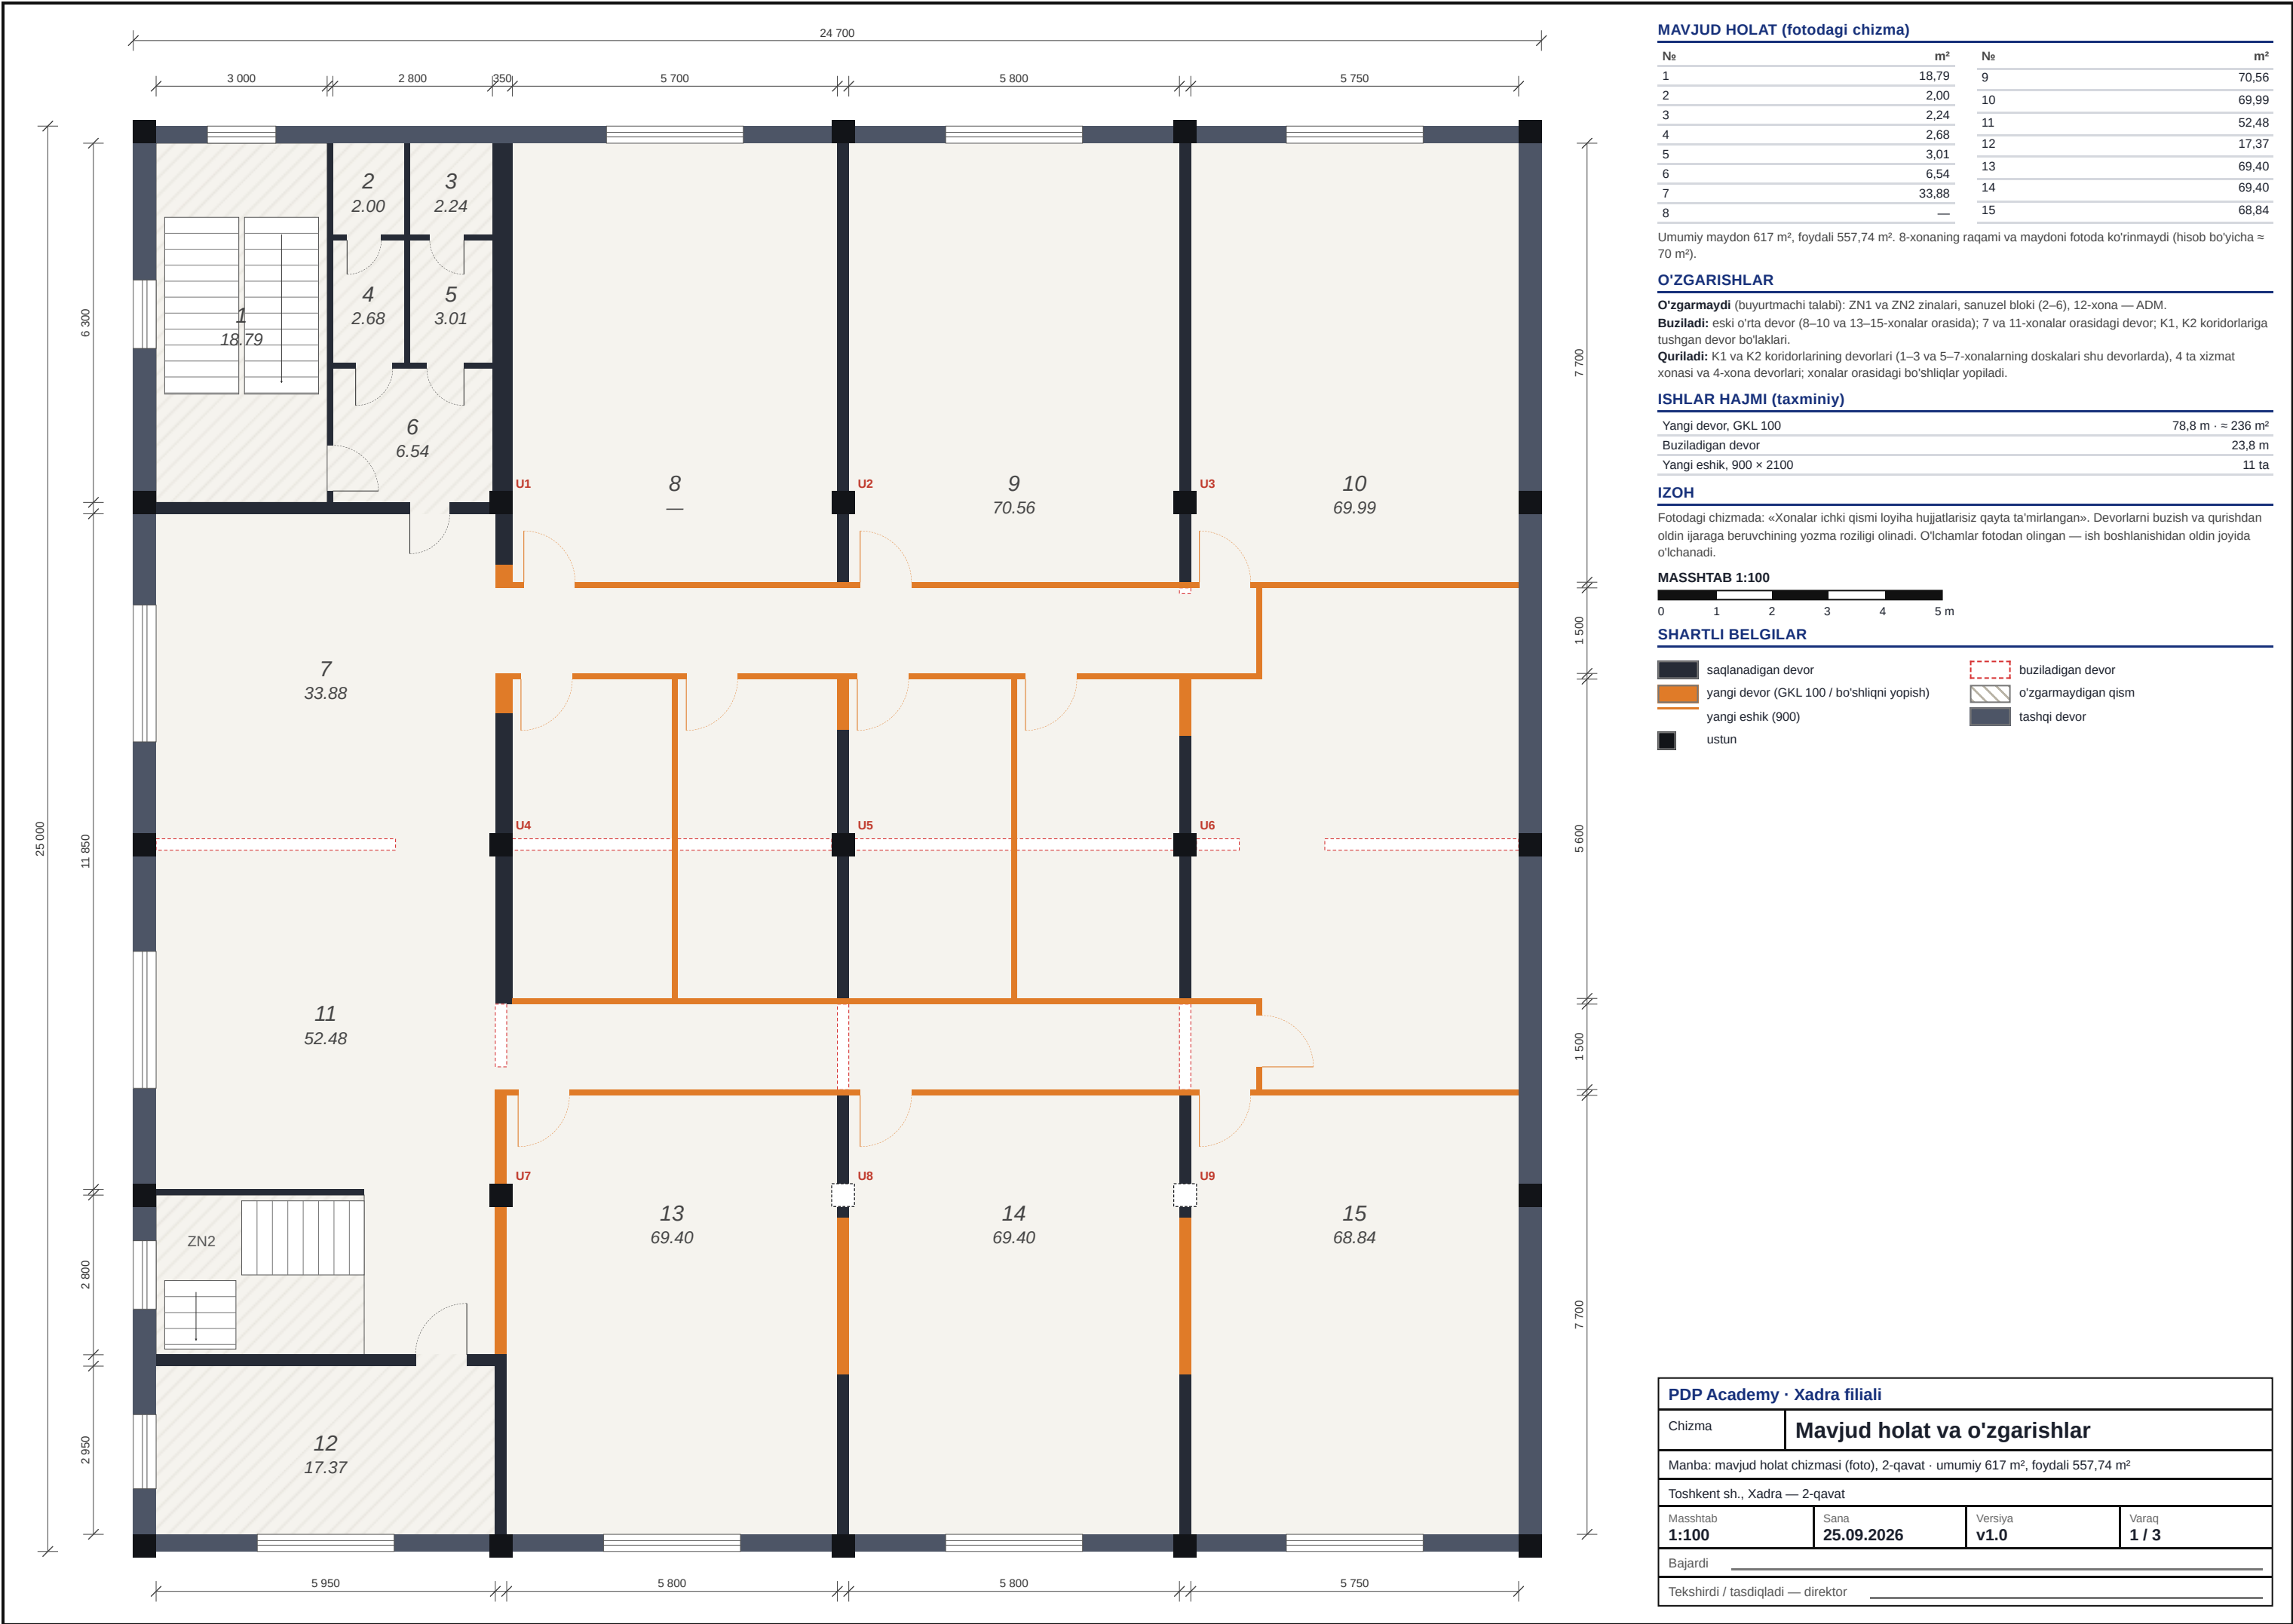

MAVJUD HOLAT (fotodagi chizma)

№	м²	№	м²
1	18,79	9	70,56
2	2,00	10	69,99
3	2,24	11	52,48
4	2,68	12	17,37
5	3,01	13	69,40
6	6,54	14	69,40
7	33,88	15	68,84
8	—		

Umumiy maydon 617 m², foydali 557,74 m². 8-xonaning raqami va maydoni fotoda koʻrinmaydi (hisob boʻyicha ≈ 70 m²).

OʻZGARISHLAR

Oʻzgarmaydi (buyurtmachi talabi): ZN1 va ZN2 zinalari, sanuzel bloki (2–6), 12-xona — ADM.
Buziladi: eski oʻrta devor (8–10 va 13–15-xonalar orasida); 7 va 11-xonalar orasidagi devor; K1, K2 koridorlariga tushgan devor boʻlaklari.
Quriladi: K1 va K2 koridorlarining devorlari (1–3 va 5–7-xonalarning doskalari shu devorlarda), 4 ta xizmat xonasi va 4-xona devorlari; xonalar orasidagi boʻshliqlar yopiladi.

ISHLAR HAJMI (taxminiy)

Yangi devor, GKL 100	78,8 m · ≈ 236 m²
Buziladigan devor	23,8 m
Yangi eshik, 900 × 2100	11 ta

IZOH

Fotodagi chizmada: «Xonalar ichki qismi loyiha hujjatlarisiz qayta taʼmirlangan». Devorlarni buzish va qurishdan oldin ijaraga beruvchining yozma roziligi olinadi. Oʻlchamlar fotodan olingan — ish boshlanishidan oldin joyida oʻlchanadi.

MASSHTAB 1:100



SHARTLI BELGILAR

	saqlanadigan devor		buziladigan devor
	yangi devor (GKL 100 / boʻshliqni yopish)		oʻzgarmaydigan qism
	yangi eshik (900)		tashqi devor
	ustun		

PDP Academy · Xadra filiali			
Chizma	Mavjud holat va o'zgarishlar		
Manba: mavjud holat chizmasi (foto), 2-qavat · umumiy 617 m², foydali 557,74 m²			
Toshkent sh., Xadra — 2-qavat			
Masshtab 1:100	Sana 25.09.2026	Versiya v1.0	Varaq 1 / 3
Bajardi _____			
Tekshirdi / tasdiqladi — direktor _____			



Ichki gabarit	23 900 × 24 400
Umumiy maydon (hujjat)	617 m ²
Foydali maydon (hujjat)	557,74 m ²
O'quv xonalari, 7 ta · 164 o'rin	312,6 m ²
Xizmat xonalari XZ1–XZ4	63,2 m ²
Koworking / tadbirlar zali (KW)	70,5 m ²
Admin va sotuv (ADM, 12-xona)	17,6 m ²
Koridorlar K1, K2 va kirish zali ZL	46,7 m ²
Zinalar va sanuzel bloki (o'zgarmaydi)	45,8 m ²
Toza balandlik	3000 mm (taxmin)

Xona	O'lcham, m	m ²	O'rin	m ² /kishi	Partalar
SR1 · 1-xona	5.70 × 7.70	43,9	24	1,8	6+6+6+6
SR2 · 2-xona	5.80 × 7.70	44,6	24	1,9	6+6+6+6
SR3 · 3-xona	5.75 × 7.70	44,2	24	1,8	6+6+6+6
SR4 · 4-xona	5.75 × 8.80 (L)	46,6	20	2,3	6+6+6+2
SR5 · 5-xona	5.75 × 7.70	44,2	24	1,8	6+6+6+6
SR6 · 6-xona	5.80 × 7.70	44,6	24	1,9	6+6+6+6
SR7 · 7-xona	5.80 × 7.70	44,6	24	1,9	6+6+6+6
ADM	5.95 × 2.95	17,6	4	—	4 stol + 4 mijoz stuli
XZ1–XZ4	2.80–2.85 × 5.60	15,7 / 15,6 / 15,9 / 15,9	—	—	xizmat, derazasiz
KW	5.95 × 11.85	70,5	~35	—	koworking; tabirda 66 o'rin
Jami		312,6	164		6 × 24 + 1 × 20

Kod	O'q	X	Y	O'lcham
U1	2-B	6 050	6 300	400 × 400
U2	3-B	12 050	6 300	400 × 400
U3	4-B	18 050	6 300	400 × 400
U4	2-C	6 050	12 300	400 × 400
U5	3-C	12 050	12 300	400 × 400
U6	4-C	18 050	12 300	400 × 400
U7	2-D	6 050	18 450	400 × 400
U8	3-D	12 050	18 450	400 × 400 *
U9	4-D	18 050	18 450	400 × 400 *


Koordinata — ichki yuzaning yuqori-chap burchagidan, ustun markazi bo'yicha; o'qlar taxminiyligi. * U8, U9 fotoda ko'rinmaydi — to'r bo'yicha qo'yilgan (devor ichida), joyida tekshirilsin.

parta 690 × 500 · stul 380 × 420
qatorda 6 parta: 2 + 2 + 2 · guruhlar orasi 600 · blok eni 5 340
qator qadami 1 300 (parta 500 + o'tish 800) · 4 qator
doskadan 1-partagacha 2 440 · oxirgi parta 6 840 · sig'im 24
ustundan: oldi/orqa 500 · yon 0
ISTISNO: SR4 (4-xona) — 6 + 6 + 6 + 2 (4-qatorda faqat o'ng blok), sig'im 20; eshik orqa tomondan
Doska 3000 kar devorda; eshiklar 900, ichkariga ochiladi.
K1, K2 koridorlari 1500. Yangi devorlar — GKL 100, ovoz izolyatsiyali.
KW: o'ng tomondan ~1,6 m o'tish yo'lagi bo'sh (sanuzel, K1, K2, kirish zali).
ADM (12-xona) va zinalar mavjud holicha; 1-qavatda zina oldida resepsn va turniket.

0 1 2 3 4 5 m

	kesilgan ichki devor		kesilgan tashqi devor
	mavjud ustun 400 × 400		taxminiy ustun (fotoda yo'q)
	deraza (joyi taxminiy)		parta 690 × 500
	stul 380 × 420		doska (kar devorda)
	o'qituvchi / xodim stoli		

PDP Academy · Xadra filiali			
Chizma	Jihozlash rejası		
Manba: mavjud holat chizmasi (foto), 2-qavat - umumiy 617 m², foydali 557,74 m²			
Toshkent sh., Xadra — 2-qavat			
Masshtab 1:100	Sana 25.09.2026	Versiya v1.0	Varaq 2 / 3
Bajardi _____			
Tekshirdi / tasdiqladi — direktor _____			

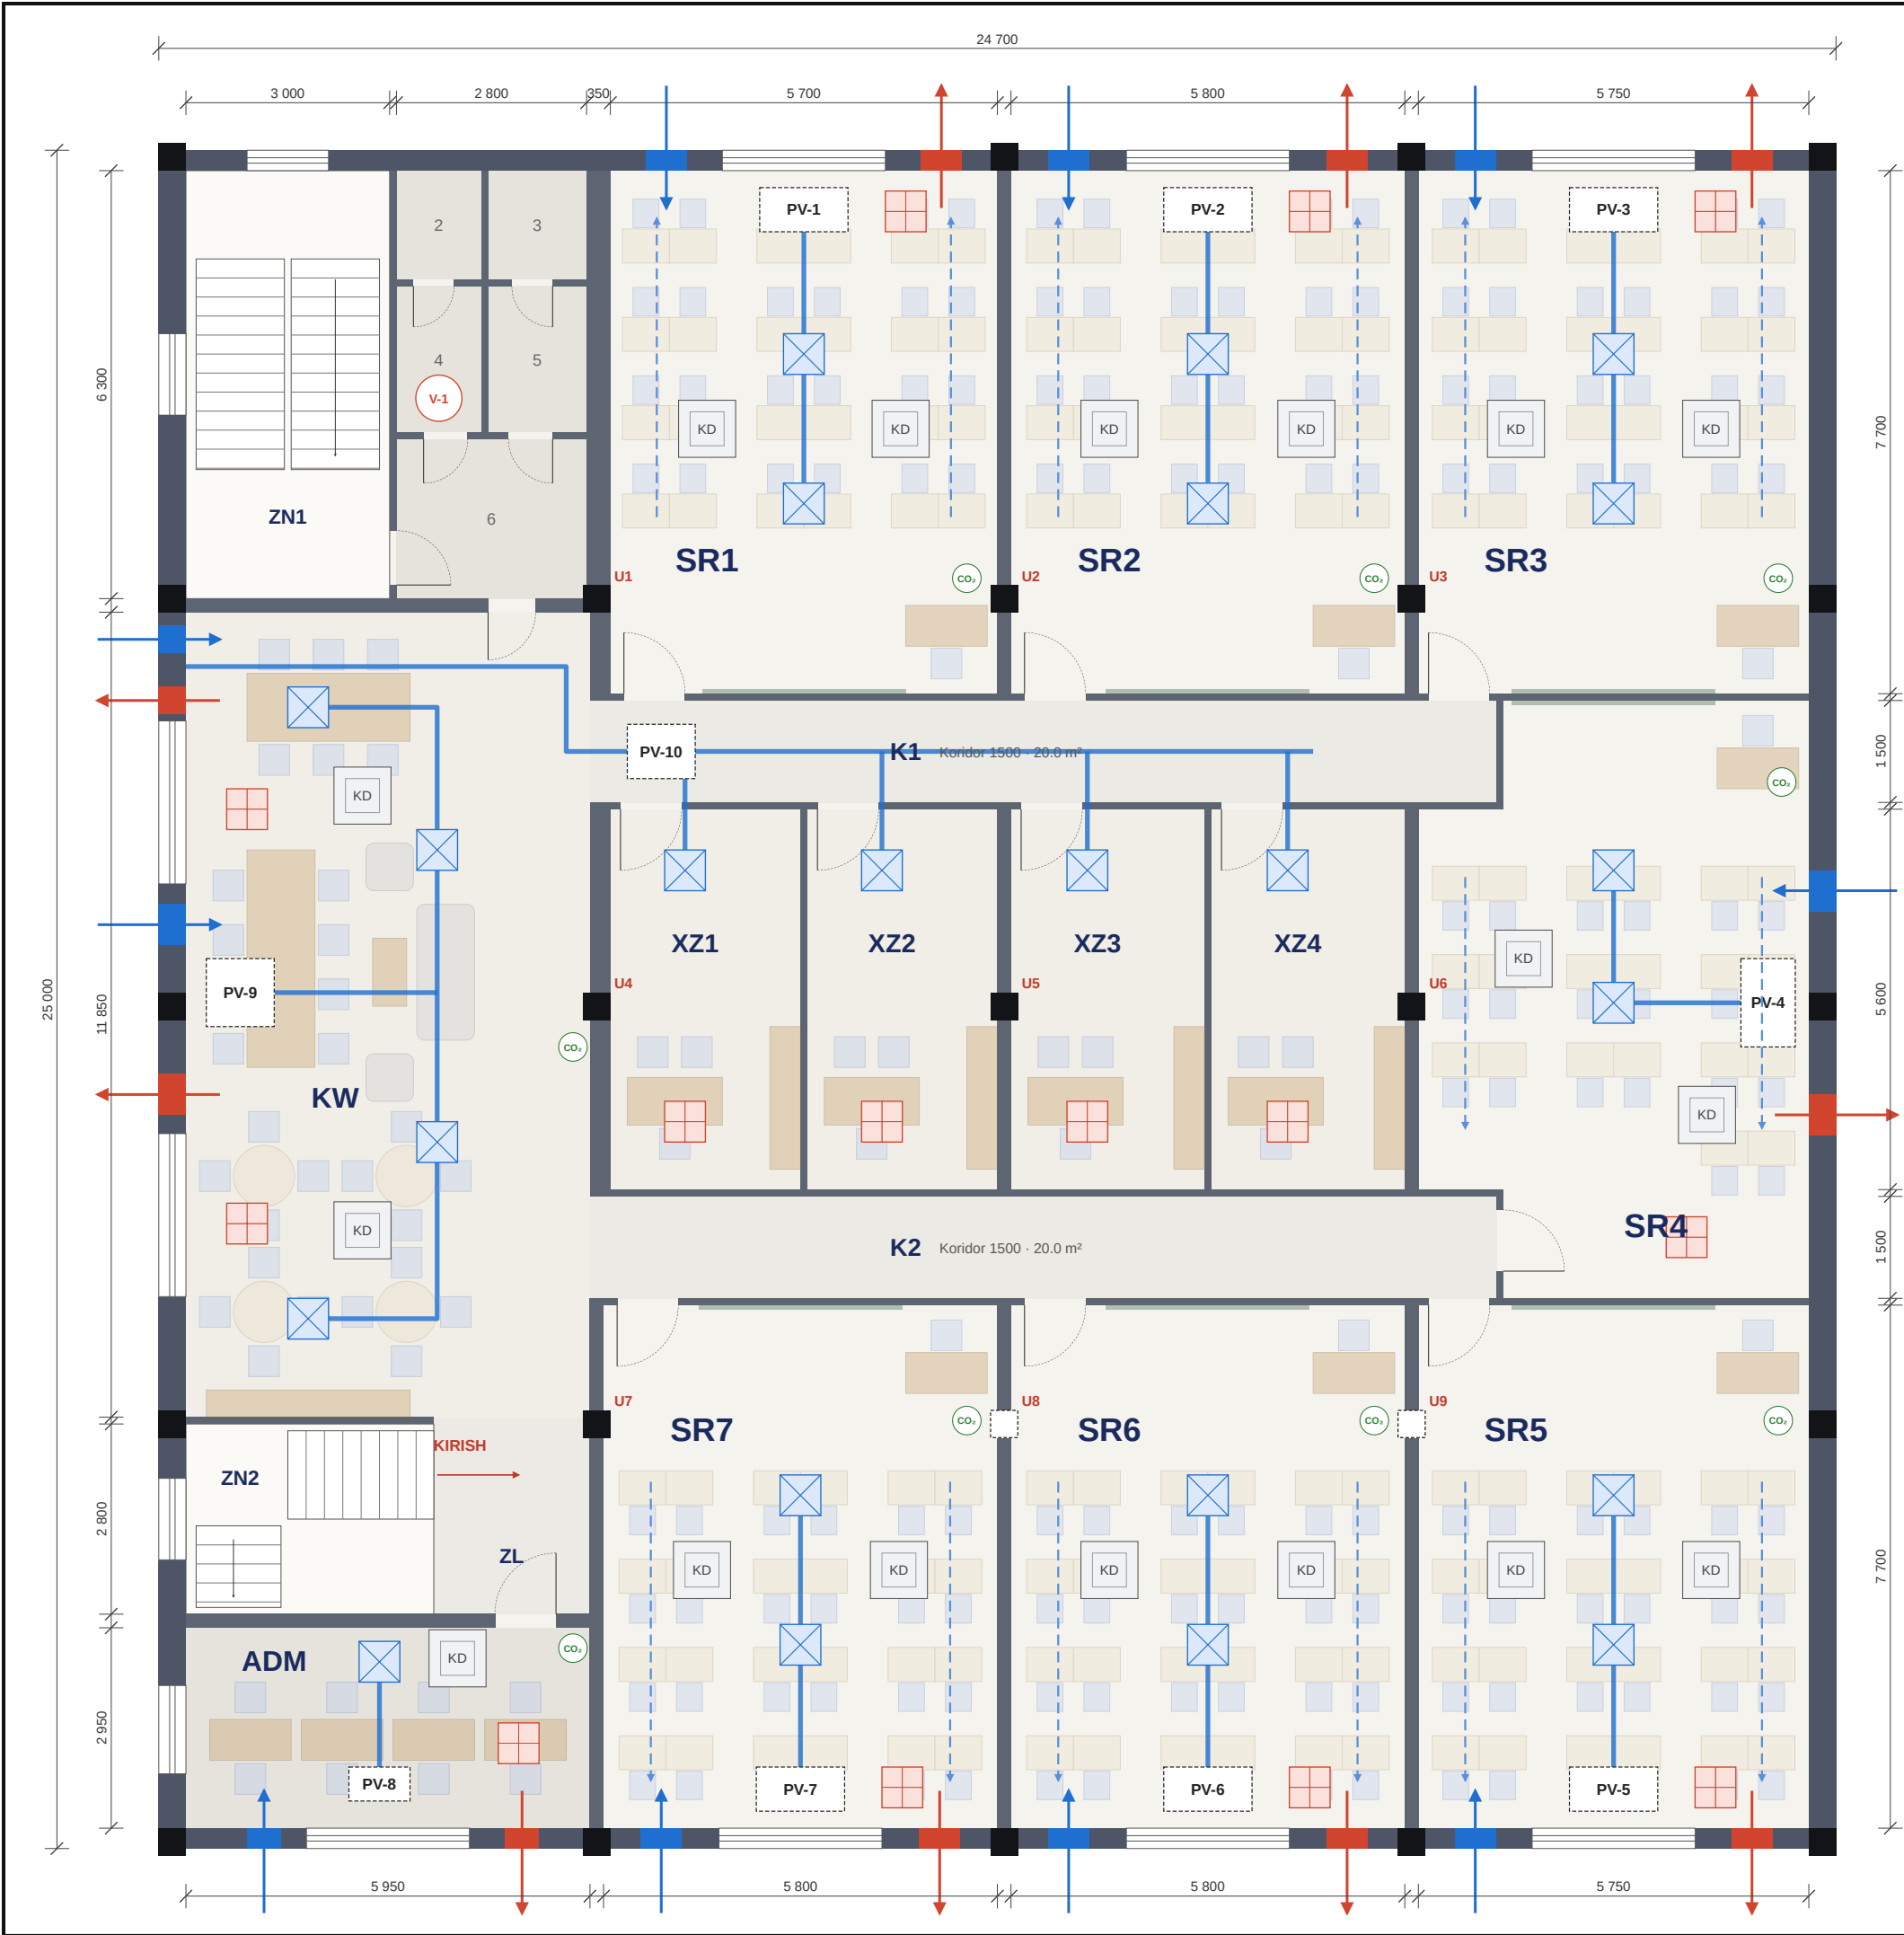

HAVO ALMASHINUVI — XONALAR BO'YICHA

Xona	Odam	Havo, m³/soat	Hajm, m³	Marta / soat	Sovutish, kVt	Qurilma
SR1	25	750	132	5,7	8,0	PV-1
SR2	25	750	134	5,6	8,0	PV-2
SR3	25	750	133	5,7	8,0	PV-3
SR4	21	630	140	4,5	6,0	PV-4
SR5	25	750	133	5,7	8,0	PV-5
SR6	25	750	134	5,6	8,0	PV-6
SR7	25	750	134	5,6	8,0	PV-7
XZ1–XZ4	12	360	189	1,9	6,0	PV-10
KW (tadbir)	70	2 100	211	9,9	17,0	PV-9
ADM	6	180	53	3,4	3,0	PV-8
Jami		7 770			80,0	

HISOB ASOSI

30 m³/soat har bir kishiga (o'quvchilar + o'qituvchi). Bir kishi soatiga ~18 l CO₂ chiqaradi: 18 l ÷ (1000 – 420) ppm ≈ 31 m³/soat — xonada CO₂ 1000 ppm dan oshmaydi.
Hajm — toza balandlik 3000 mm (taxmin) bo'yicha. Sovutish — odamlar, noutbuklar, proyektor, yoritish, derazadan quyosh va toza havo (rekuperator FIK 60%) yig'indisi, Toshkent yozi (+40 °C) uchun dastlabki baho.

YECHIM

1–3 va 5–7-xonalar 7,7 m chuqur, deraza orqa devorda: tabiiy shamollatish (~2,5 × H ≈ 7,5 m) deyarli butun xonaga yetadi, lekin qish va yozda derazalar yopiq — har sinfga alohida **PV qurilma** (rekuperatorli, ~750 m³/soat, shovqin ≤ 35 dB(A)), deraza devori yonida shift ichida.
4-xona va xizmat xonalarida deraza yo'q — mexanik ventilyatsiya va konditsioner majburiy. PV-4 havosi o'ng tashqi devor orqali (qo'shni bino bo'lsa — kanal bilan fasadga); PV-10 koworking chap devoridan olib, K1 shifti orqali XZ1–XZ4 ga beradi.
KW: derazalar chap devorda; tadbirda ~70 kishi — PV-9 ~2 100 m³/soat.
Toza havo doska tomonga beriladi, orqa tomondan so'riladi. CO₂ datchigi bilan boshqariladi; bo'sh xona o'chadi. Har sinfga 2 ta KD (kasseta yoki kanali).
V-1: sanuzel chiqarish ventilyatsiyasi 4 × 50 = 200 m³/soat — mavjud shaxtani tekshirish. Tutun chiqarish talabini yong'in xavfsizligi mutaxassisi belgilaydi.

MASSHTAB 1:100



SHARTLI BELGILAR

- PV — rekuperatorli kiritish-chiqarish qurilmasi (shift ichida)

toza havo diffuzori

fasad panjarasi: toza havo kirishi

KD — konditsioner ichki bloki

CO₂ datchigi
- toza havo kanali

so'rish panjarasi

fasad panjarasi: iflos havo chiqishi

xonadagi havo oqimi

PDP Academy · Xadra filiali			
Chizma	Havo almashinuvi sxemasi		
Manba: mavjud holat chizmasi (foto), 2-qavat · umumiy 617 m², foydali 557,74 m²			
Toshkent sh., Xadra — 2-qavat			
Masshtab 1:100	Sana 25.09.2026	Versiya v1.0	Varaq 3 / 3
Bajardi _____			
Tekshirdi / tasdiqladi — direktor _____			