



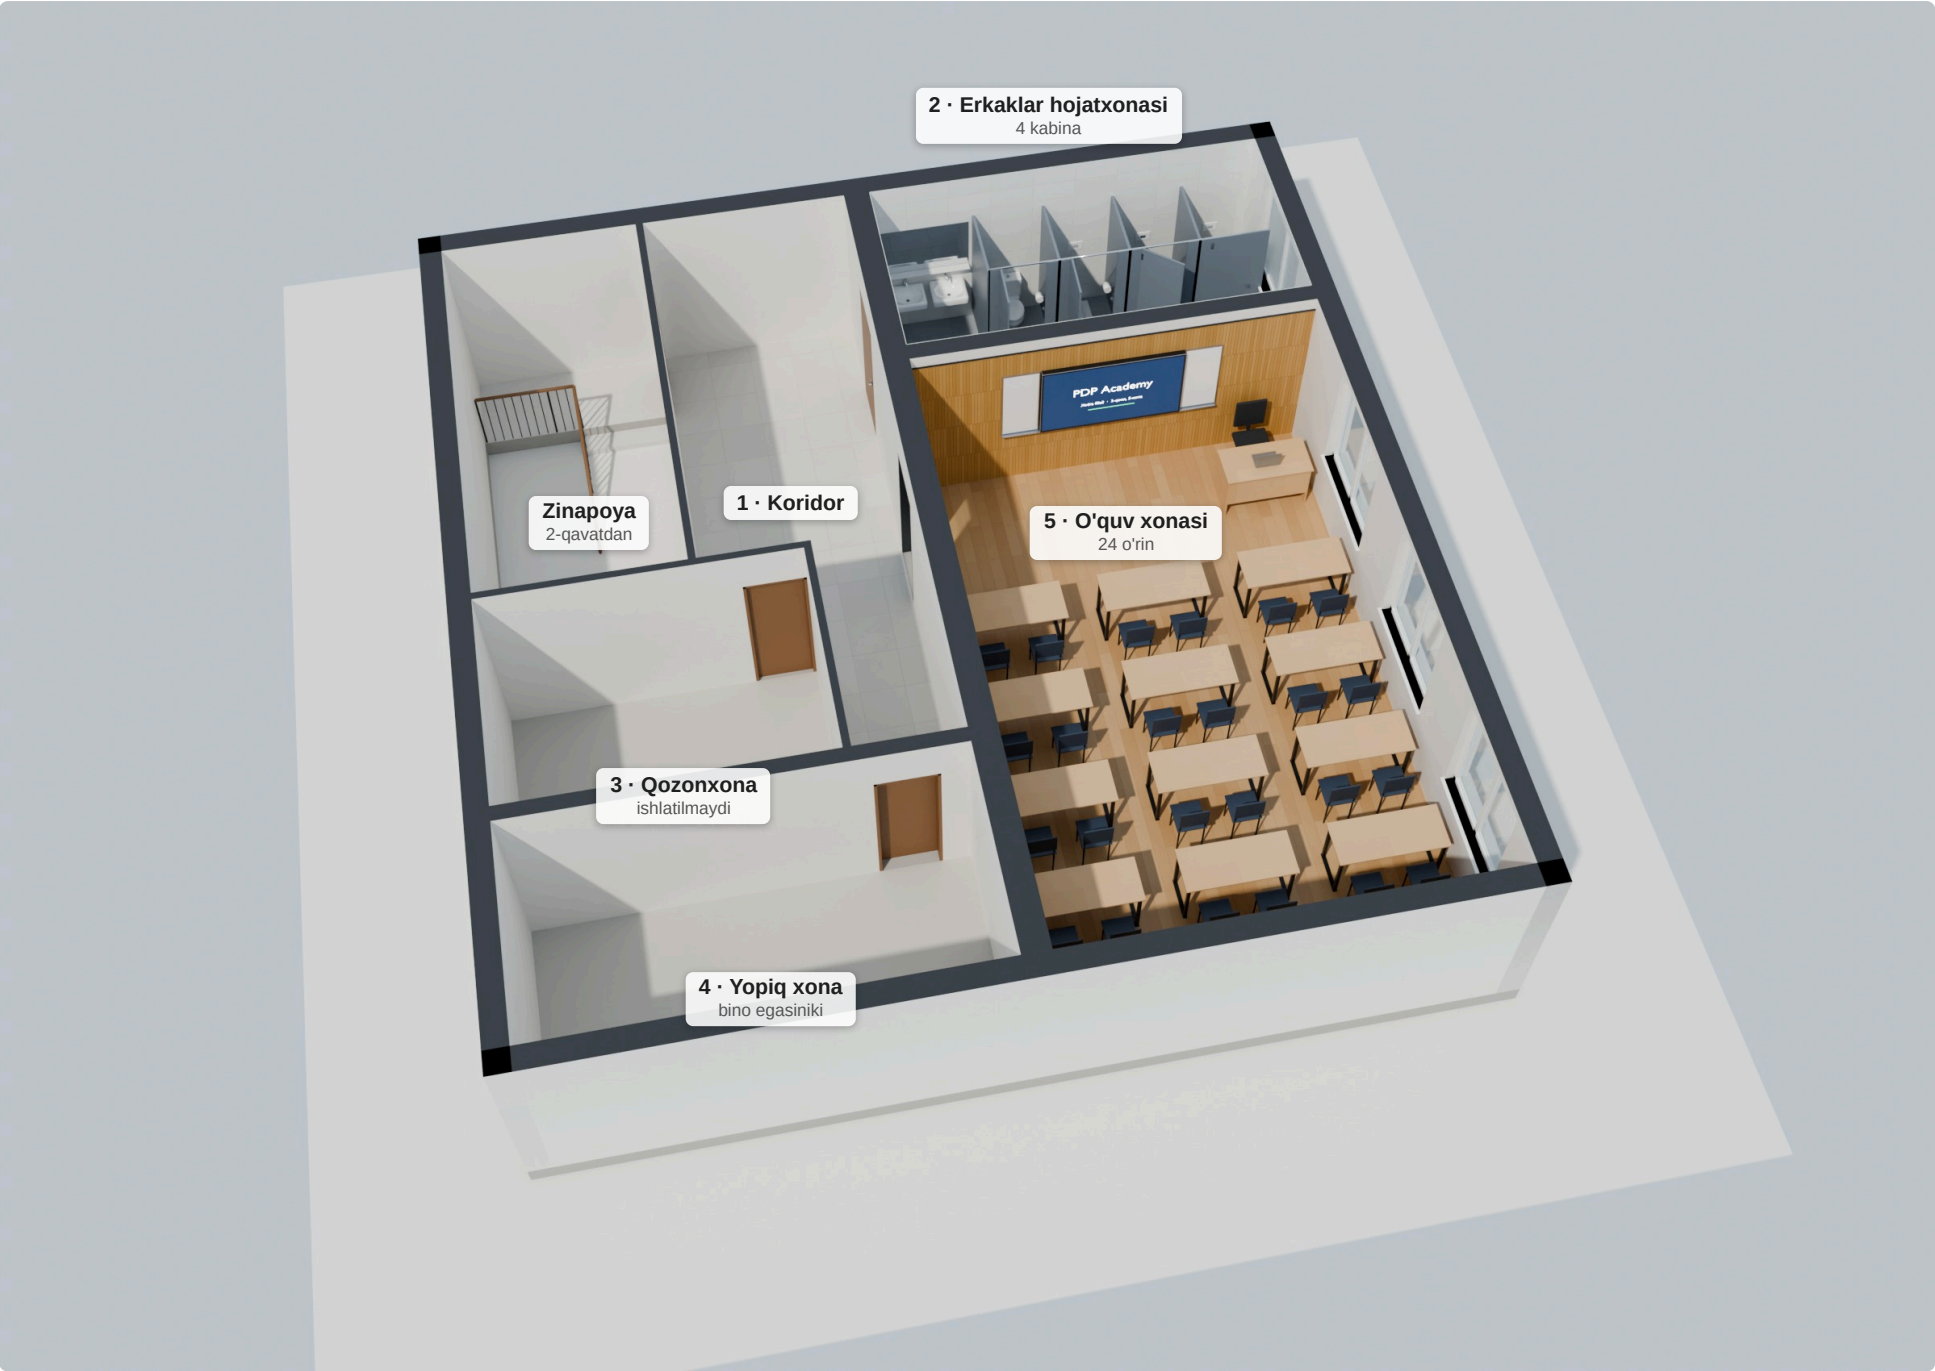

1 Umumiy ko'rinish — janubi-g'arbdan, shift olib tashlangan, devorlar 2.7 m da kesilgan. Bino 11.85 × 12.3 m, umumiy 118 m².

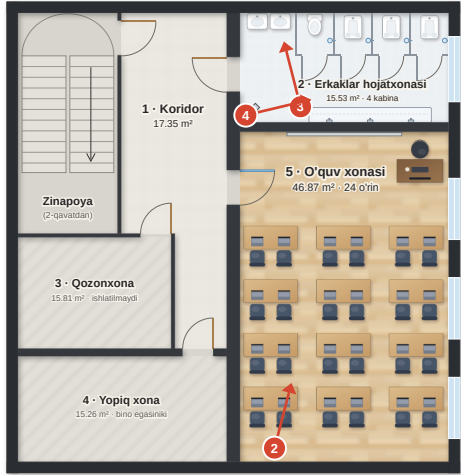

Kamera nuqtalari: 2 — sinf, 3 va 4 — hojatxona

5-xona — o'quv xonasi. 12 ta ikki kishilik parta (140 × 60 sm), 4 qator × 3, 24 o'rin. Interaktiv doska shimoliy devorda, eshikdan kirganda chapda; ikki yonida oq doska. Ustoz stoli deraza tomonda. Bambuk panel 3 devorda, 2.5 m gacha (doska devori, orqa devor, eshikli devor). Eshik shisha, matli polosa bilan. Konditsioner orqa devorda.

2-xona — erkaklar hojatxonasi. Kirganda chapda 2 ta rakovina, ko'zgu va qo'l quritgich. Shimoliy devor bo'ylab 4 ta kabina (1.00 × 1.10 m): 1-sida unitaz, 2–4-sida chashagen, har birida mustahab. Janubiy devor bo'ylab taxorat joyi (3.2 m, 3 ta jo'mrak). Devorlar shiftgacha kafel, eshik yonida trap.

Taxminlar (joyida aniqlanadi). Shift balandligi 3.5 m (bino balandligi). Derazalar joyi va o'lchami (tokcha 0.9 m, tepasi 2.6 m) chizma fotosidan taxminiy. Kabina to'siqlari HPL, 2.0 m balandlikda. Chashagenlar polga botirilgan. Pol, kafel va jihozlar rangi — namuna uchun, tanlovga qarab o'zgaradi. Ko'zgu va qo'l quritgich xarajatlar jadvalida yo'q — ko'rinish uchun qo'yilgan.

Fayllar. chizma/3d/: har bir ko'rinishning rasmi (JPG) va Xadra_3-qavat.blend (Blender 4.2, 4 ta kamera). Sahna manba/blender3.py dan qayta yig'iladi.



2 5-xona → doska. Orqa qatordan: interaktiv doska, bambuk panel, o'ngda derazalar va ustoz stoli.



3 Hojatxona ichi — rakovinalar va 1-kabina. Chapda kirish eshigi, 2 ta rakovina va ko'zgu, o'ngda unitazli kabina (mustahab bilan).



4 Hojatxona ichi — eshikdan sharqq. Chapda kabinalar, o'ngda taxorat joyi (3 ta jo'mrak), oldinda deraza (xira oyna).