
PDP Academy · Xadra filiali


# 3-qavat rejasi — o'quv xonasi (24 o'rin) va erkaklar hojatxonasi

Masshtab 1:50 (A3) · v1.2 · 09.10.2026

0 1 2 3 4 5 m (1:50)

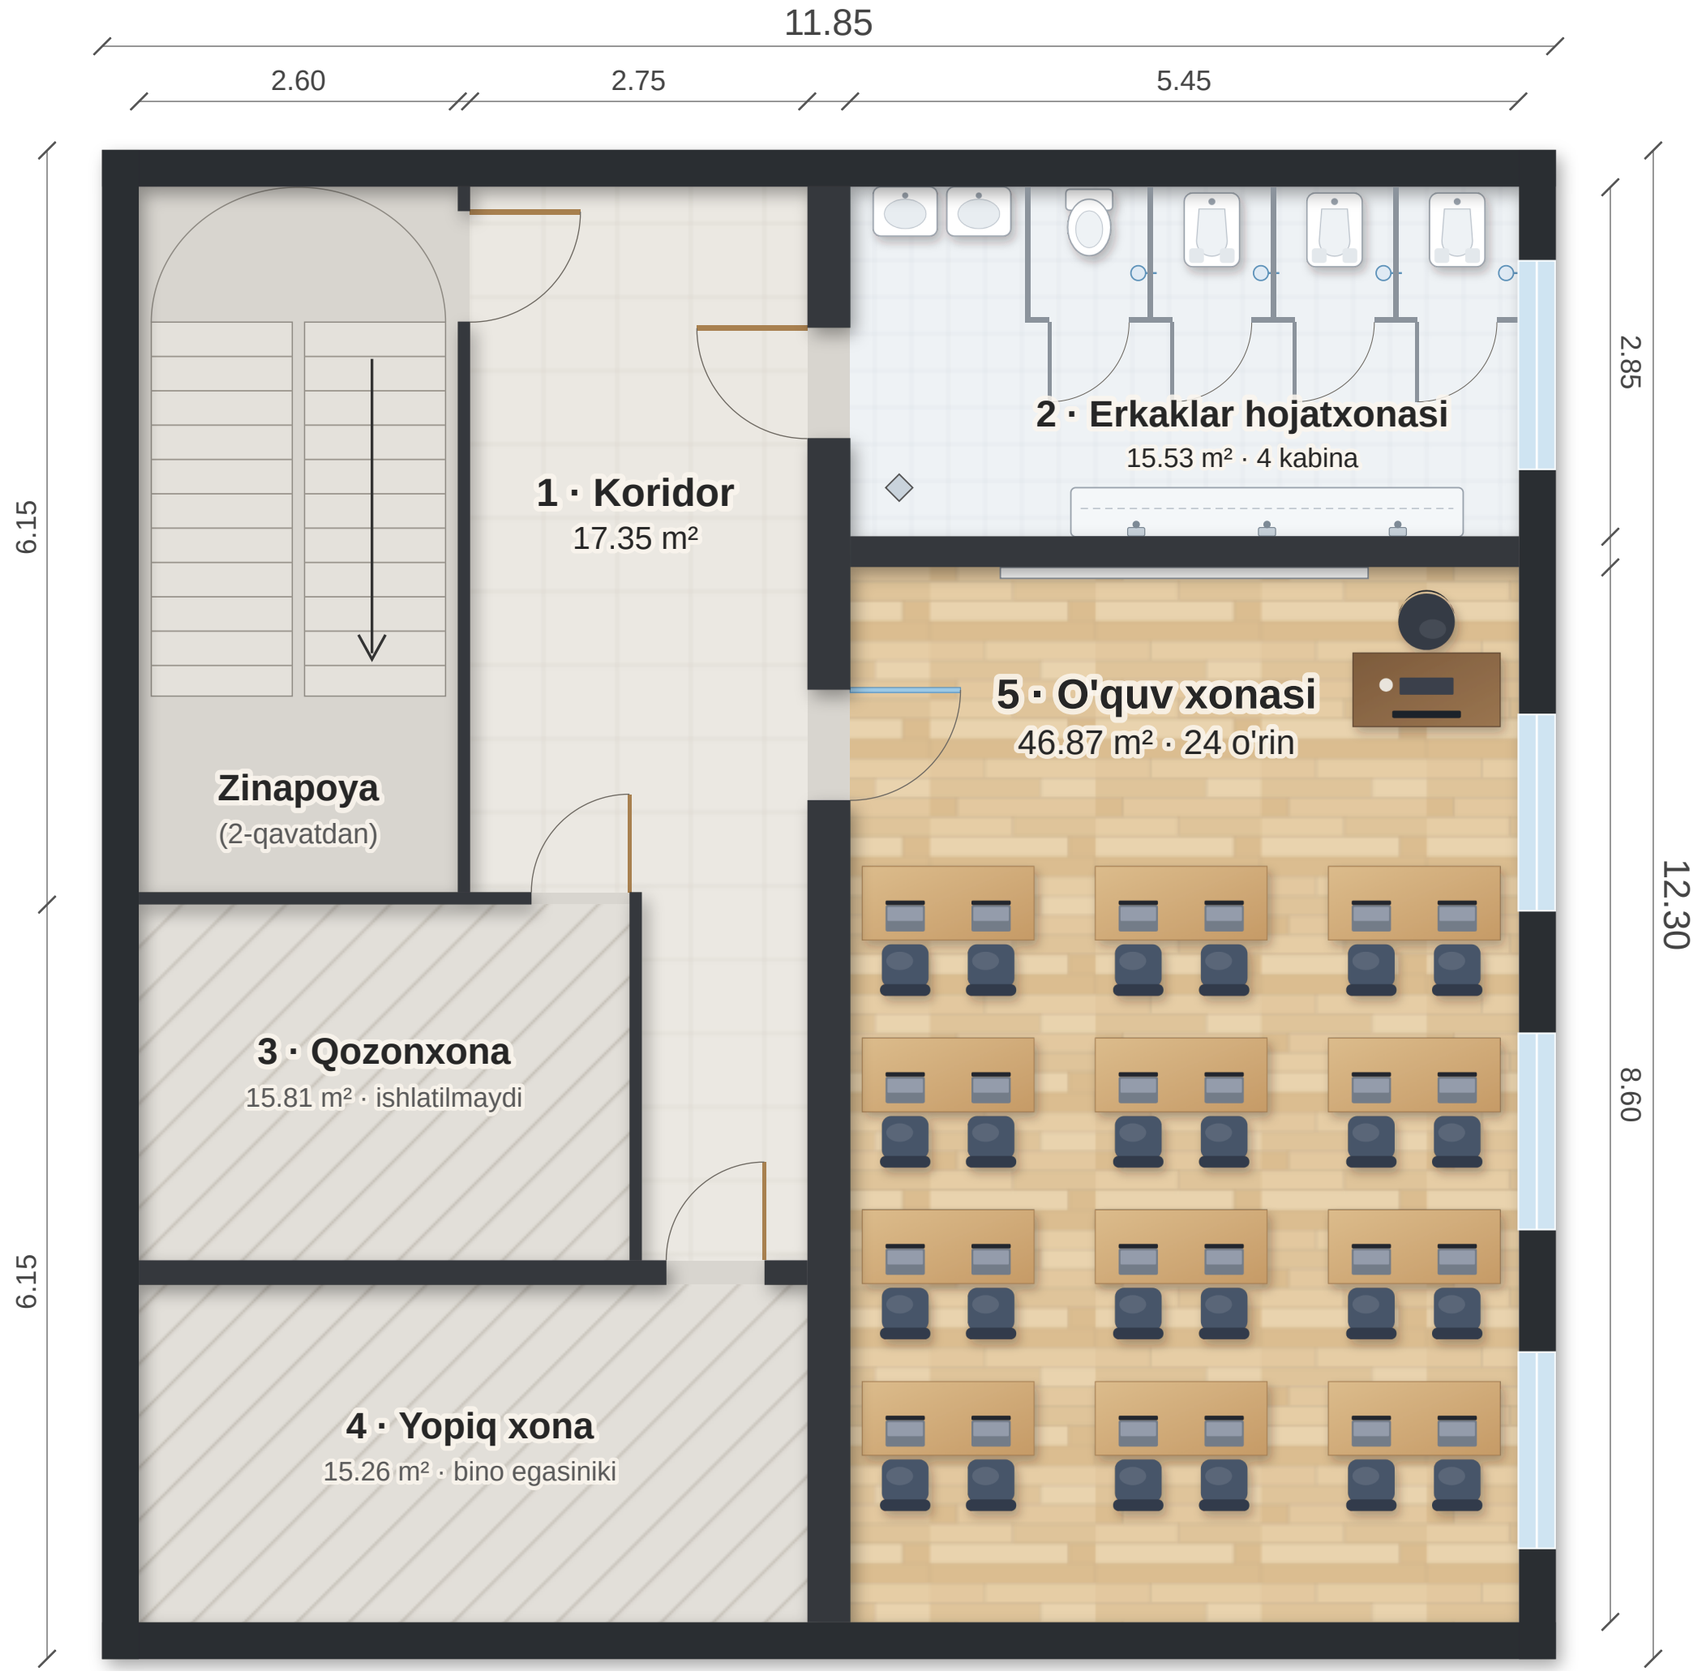


## 2-xona — erkaklar hojatxonasi (buyurtmachi chizgan ko'rinishda)

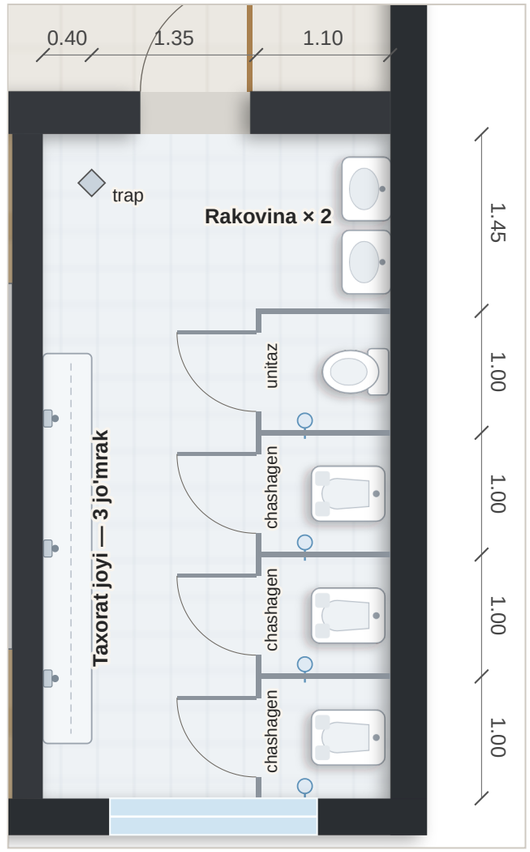


Reja 90° burilgan: eshik tepada (koridordan), deraza pastda.

**Kirganda chapda**
2 ta rakovina (jo'mrak bilan)

**Kabinalar**
4 ta, har biri 1.00 × 1.10 m: 1 ta unitazli, 3 ta chashagenli; har birida mustahab; eshiklari 65 sm, tashqariga ochiladi

**Taxorat joyi**
janubiy devor bo'ylab 3.2 m, 3 ta jo'mrak

**Pol**
eshik yonida trap (pol suvi uchun)

**Kafel**
devor 58 m², pol 16 m²

| Xona | Vazifasi | m² |
|---|---|---|
| 1 | Koridor (zinapoyadan) | 17.35 |
| 2 | Erkaklar hojatxonasi | 15.53 |
| 3 | Qozonxona — ishlatilmaydi | 15.81 |
| 4 | Yopiq xona — bino egasiniki | 15.26 |
| 5 | O'quv xonasi, 24 o'rin | 46.87 |
| **Umumiy / foydali maydon** | | **118 / 110.82** |

| **5-xona: o'quv xonasi** | |
|---|---|
| Partalar | 12 ta ikki kishilik, 140 × 60 sm — 4 qator × 3 |
| Doska | interaktiv, shimoliy devorda (kirganda chapda) |
| Doska → 1-parta / qator qadami | 2.44 m / 1.40 m |
| Yo'lak / devorgacha | 50 sm / 10–15 sm |
| Oxirgi parta (doskadan) / orqa devorgacha | 7.24 m / 1.36 m |
| Chetki o'rindan qarash burchagi | 39.2° (Beruniy — 39.8°) |
| Bambuk panel | 3 devor, 2.5 m balandlikda |

O'lchamlar 3-qavat chizmasi fotosidan olingan (11.85 × 12.30 m); derazalar joyi taxminiy — joyida o'lchanadi. 2-qavatdagi WC — ayollar hojatxonasi (2 kabina, unitazli, tambur orqali). Hojatxona ventilyatsiyasi (chiqarish) va suv/kanalizatsiya yo'li santexnik bilan aniqlanadi.