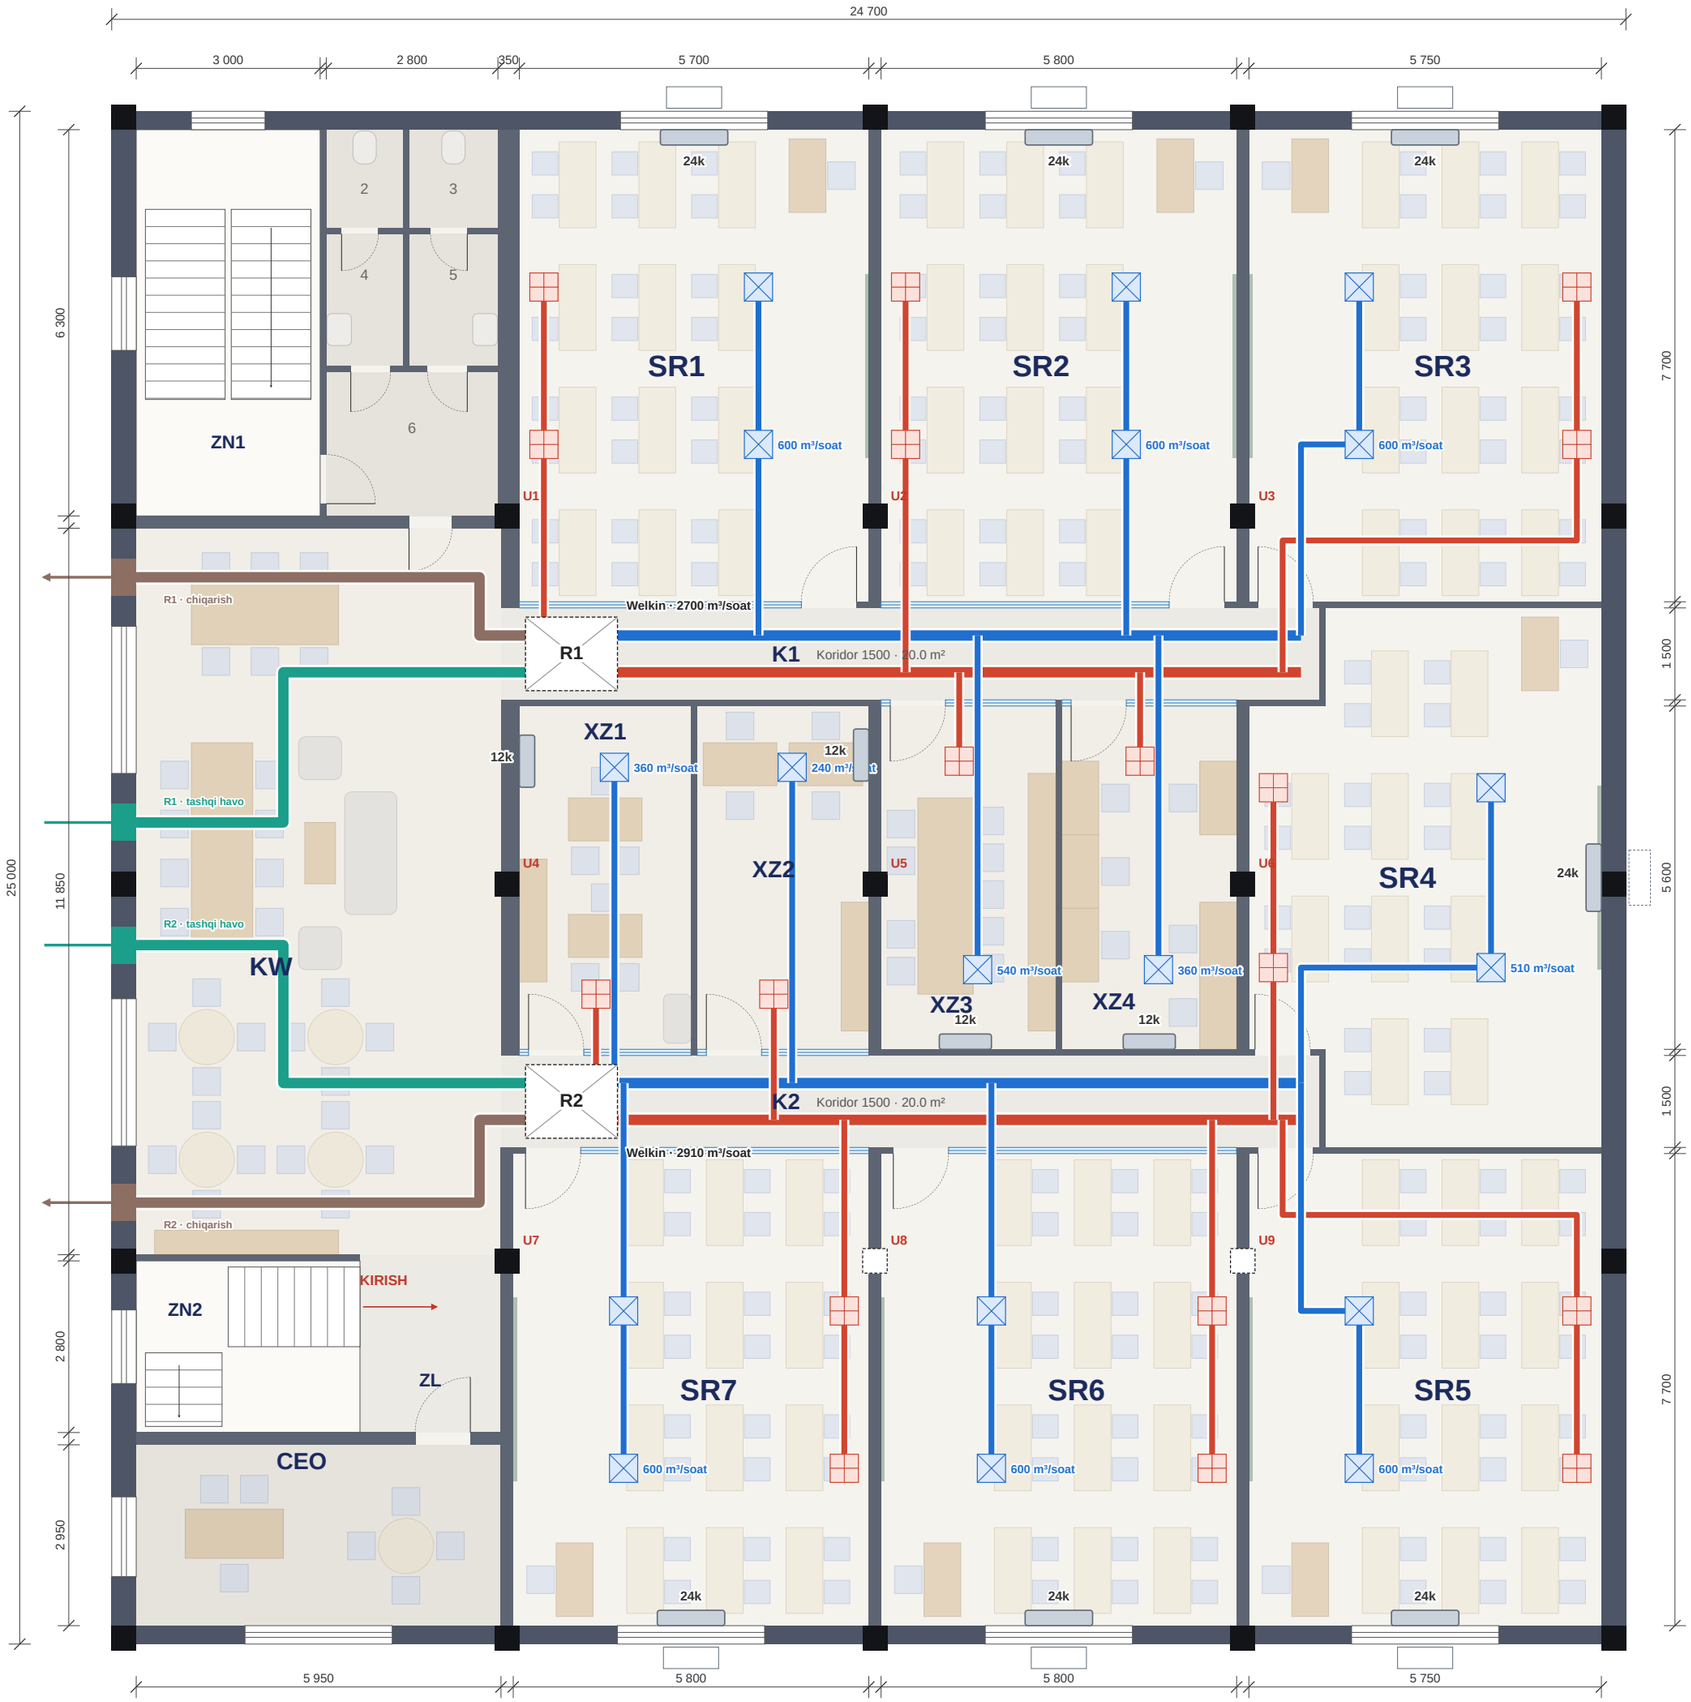


VENTILYATSIYA — 2 TA REKUPERATOR (WELKIN)

Qurilma	Xonalar	Loyiha, m³/soat	Me'yoriy min	Kanal
R1 · K1	SR1, SR2, SR3, XZ3, XZ4	2 700	2 537	600×300
R2 · K2	SR4, SR5, SR6, SR7, XZ1, XZ2	2 910	2 717	600×300
Jami	**havo kanallari ~223 m**	**5 610**	**5 253**	

XONALAR: TASHQI HAVO VA SPLIT (BUYURTMACHI TANLOVI)

Xona	Odam	Havo, m³/soat	Rek.	CO_2, ppm	Yuk, kW	Split
SR1	25	600	R1	1 170	5.1–7.6	**24k** ≈
SR2	25	600	R1	1 170	5.1–7.6	**24k** ≈
SR3	25	600	R1	1 170	5.1–7.6	**24k** ≈
SR4	21	510	R2	1 161	4.2–5.5	**24k** ✓
SR5	25	600	R2	1 170	5.1–7.6	**24k** ≈
SR6	25	600	R2	1 170	5.1–7.6	**24k** ≈
SR7	25	600	R2	1 170	5.1–7.6	**24k** ≈
XZ1	6	360	R2	720	1.9–2.3	**12k** ✓
XZ2	4	240	R2	720	1.4–1.8	**12k** ✓
XZ3	9	540	R1	720	2.3–2.7	**12k** ✓
XZ4	6	360	R1	720	2.5–2.9	**12k** ✓
KW	35/70	—	—		6.5–15.1	mavjud 24k + 18k
CEO	7	—	—			mavjud

HISOB ASOSI

Tashqi havo: sinflarda 24 m³/soat·kishi (me'yoriy ~22), derazasiz xizmat xonalarida 60 m³/soat·kishi (KMK). R2 ga 2 910 m³/soat kerak — **3000 m³/soatlik model** (kanal qarshiligi ~300 Pa da).

Split: yuk — odamlar (115 W/kishi), yoritish, panel/kompyuter, devor-oyna-tom (oraliq) va rekuperatordan keyingi tashqi havo qoldig'i. ✓ — 42–43 °C da ham yetadi; ≈ — yukning past–o'rta qismida yetadi (derazalar yo'nalishi va tomga bog'liq). Sinflarda 24k — deraza ustida, xizmat xonalarida 12k. Koworkingdagi mavjud konditsionerlar koridorlarni ham sovutadi.

Toza havo doska oldida beriladi, orqa devor yonida so'riladi. Kanallar koridorlar osma shifti ichida (~2.8 m), koworkingda — shift ostida (fasadgacha). Kanallar yo'nalishi — taklif, buyurtmachi o'zgartirishi mumkin.

MASSHTAB 1:100

0 1 2 3 4 5 m

SHARTLI BELGILAR

- R1, R2 — Welkin rekuperatori (koridor shiftida)
- so'rish kanali (xonalardan rekuperatorga)
- chiqarish kanali (fasadga)
- so'rish panjarasi
- split — tashqi blok (fasadda; punktir — joyi aniqlanadi)
- toza havo kanali (rekuperatordan xonalarga)
- tashqi havo kanali (fasaddan)
- toza havo diffuzori
- split — ichki blok (devorda), yozuv: BTU/soat

PDP Academy · Xadra filiali			
Chizma	**Ventilyatsiya va konditsionerlash**		
Manba: mavjud holat chizmasi (foto), 2-qavat · umumiy 617 m², foydali 557,74 m²			
Toshkent sh., Xadra — 2-qavat			
Masshtab **1:100**	Sana **09.10.2026**	Versiya **v1.2**	Varaq **3 / 3**
Bajardi			
Tekshirdi / tasdiqladi — direktor			