


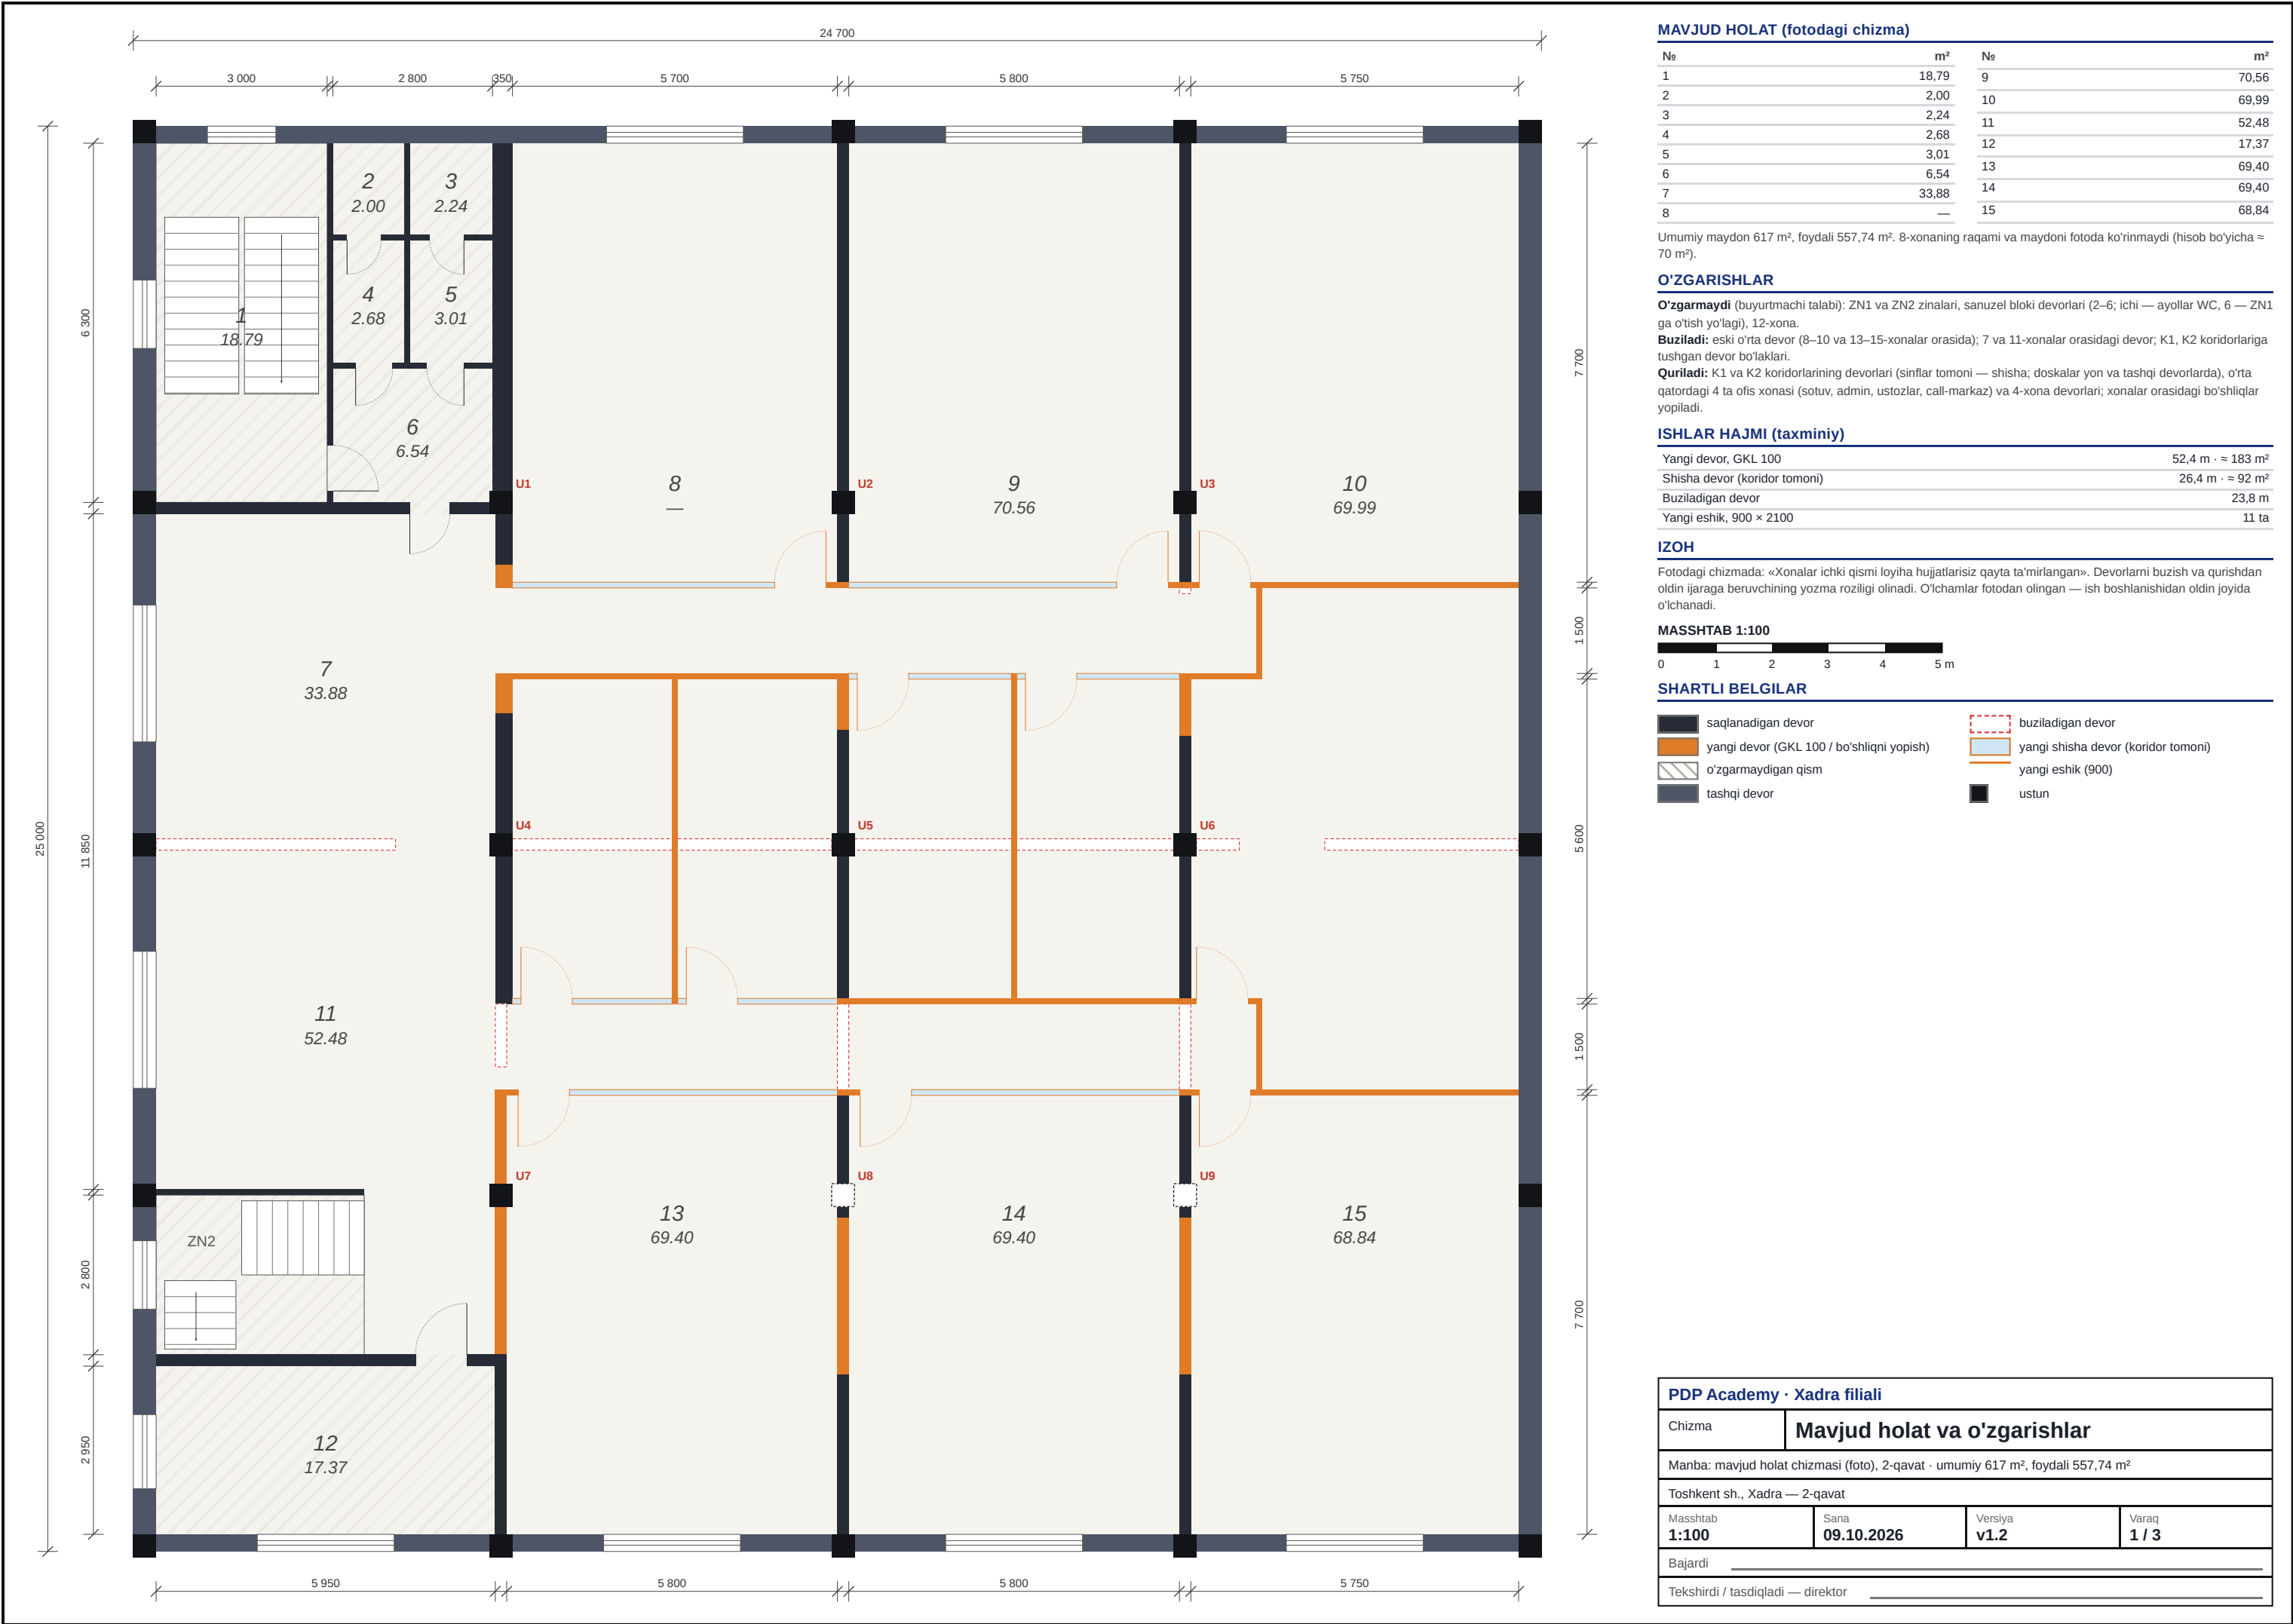

MAVJUD HOLAT (fotodagi chizma)

| № | m²    | №  | m²    |
|---|-------|----|-------|
| 1 | 18,79 | 9  | 70,56 |
| 2 | 2,00  | 10 | 69,99 |
| 3 | 2,24  | 11 | 52,48 |
| 4 | 2,68  | 12 | 17,37 |
| 5 | 3,01  | 13 | 69,40 |
| 6 | 6,54  | 14 | 69,40 |
| 7 | 33,88 | 15 | 68,84 |
| 8 | —     |    |       |

Umumiy maydon 617 m², foydali 557,74 m². 8-xonaning raqami va maydoni fotoda koʻrinmaydi (hisob boʻyicha ≈ 70 m²).

OʻZGARISHLAR

**Oʻzgarmaydi** (buyurtmachi talabi): ZN1 va ZN2 zinalari, sanuzel bloki devorlari (2–6; ichi — ayollar WC, 6 — ZN1 ga oʻtish yoʻlagi), 12-xona.

**Buziladi**: eski oʻrta devor (8–10 va 13–15-xonalar orasida); 7 va 11-xonalar orasidagi devor; K1, K2 koridorlariga tushgan devor boʻlaklari.

**Quriladi**: K1 va K2 koridorlarining devorlari (sinflar tomoni — shisha; doskalar yon va tashqi devorlarda), oʻrta qatordagi 4 ta ofis xonasi (sotuv, admin, ustozlar, call-markaz) va 4-xona devorlari; xonalar orasidagi boʻshliqlar yopiladi.

ISHLAR HAJMI (taxminiy)

|                               |                   |
|-------------------------------|-------------------|
| Yangi devor, GKL 100          | 52,4 m · ≈ 183 m² |
| Shisha devor (koridor tomoni) | 26,4 m · ≈ 92 m²  |
| Buziladigan devor             | 23,8 m            |
| Yangi eshik, 900 × 2100       | 11 ta             |

IZOH

Fotodagi chizmada: «Xonalar ichki qismi loyiha hujjatlarisiz qayta taʼmirlangan». Devorlarni buzish va qurishdan oldin ijaraga beruvchining yozma roziligi olinadi. Oʻlchamlar fotodan olingan — ish boshlanishidan oldin joyida oʻlchanadi.

MASSHTAB 1:100



SHARTLI BELGILAR

|                                           |                                     |
|-------------------------------------------|-------------------------------------|
| saqlanadigan devor                        | buziladigan devor                   |
| yangi devor (GKL 100 / boʻshliqni yopish) | yangi shisha devor (koridor tomoni) |
| oʻzgarmaydigan qism                       | yangi eshik (900)                   |
| tashqi devor                              | ustun                               |

PDP Academy · Xadra filiali

Chizma Mavjud holat va oʻzgarishlar

Manba: mavjud holat chizmasi (foto), 2-qavat · umumiy 617 m², foydali 557,74 m²

Toshkent sh., Xadra — 2-qavat

|                         |                           |                        |                       |
|-------------------------|---------------------------|------------------------|-----------------------|
| Mashtab<br><b>1:100</b> | Sana<br><b>09.10.2026</b> | Versiya<br><b>v1.2</b> | Varaq<br><b>1 / 3</b> |
|-------------------------|---------------------------|------------------------|-----------------------|

Bajardi \_\_\_\_\_

Tekshirdi / tasdiqladi — direktor \_\_\_\_\_



| MAYDON                                                        |                       |
|---------------------------------------------------------------|-----------------------|
| Ichki gabarit                                                 | 23 900 × 24 400       |
| Umumiy maydon (hujjat)                                        | 617 m²                |
| Foydali maydon (hujjat)                                       | 557,74 m²             |
| O'quv xonalari, 7 ta · 164 o'rin                              | 312,6 m²              |
| Offline sotuv (XZ1) va admin (XZ2)                            | 31,3 m²               |
| Ustozlar (XZ3), call-markaz (XZ4)                             | 31,8 m²               |
| Koworking / tadbirlar zali (KW)                               | 70,5 m²               |
| CEO xonasi (12-xona, o'zgarmaydi)                             | 17,6 m²               |
| Koridorlar K1, K2 va kirish zali ZL                           | 46,7 m²               |
| Zinalar, ayollar WC va o'tish yo'lagi (devorlari o'zgarmaydi) | 45,8 m²               |
| Balandlik (poldan shiftgacha)                                 | 3500 mm (buyurtmachi) |

| XONALAR           |                 |       |       |          |                                                  |
|-------------------|-----------------|-------|-------|----------|--------------------------------------------------|
| Xona              | O'lcham, m      | m²    | O'rin | m²/kishi | Partalar                                         |
| SR1 · 1-xona      | 7.70 × 5.70     | 43,9  | 24    | 1,8      | 4+4+4                                            |
| SR2 · 2-xona      | 7.70 × 5.80     | 44,6  | 24    | 1,9      | 4+4+4                                            |
| SR3 · 3-xona      | 7.70 × 5.75     | 44,2  | 24    | 1,8      | 4+4+4                                            |
| SR4 · 4-xona      | 8.80 × 5.75 (L) | 46,6  | 20    | 2,3      | 4+4+2                                            |
| SR5 · 5-xona      | 7.70 × 5.75     | 44,2  | 24    | 1,8      | 4+4+4                                            |
| SR6 · 6-xona      | 7.70 × 5.80     | 44,6  | 24    | 1,9      | 4+4+4                                            |
| SR7 · 7-xona      | 7.70 × 5.80     | 44,6  | 24    | 1,9      | 4+4+4                                            |
| XZ1 · sotuv       | 2.80 × 5.60     | 15,7  | 2     | —        | 2 stol + 4 mijoz stuli, shisha devor             |
| XZ2 · admin       | 2.80 × 5.60     | 15,6  | 2     | —        | 2 stol + 2 mehmon stuli, shisha devor            |
| XZ3 · ustozlar    | 2.85 × 5.60     | 15,9  | 9     | —        | umumiy stol, lokerlar                            |
| XZ4 · call-markaz | 2.85 × 5.60     | 15,9  | 6     | —        | devor bo'ylab 6 ish o'rni                        |
| CEO (12-xona)     | 5.95 × 2.95     | 17,6  | 1     | —        | ish stoli + 4 kishilik stol, derazali            |
| KW                | 5.95 × 11.85    | 70,5  | ~35   | —        | koworking; sahna — XZ1 devori, tadbirda 68 o'rin |
| Jami              |                 | 312,6 | 164   |          | 6 × 24 + 1 × 20                                  |

| USTUNLAR — MAVJUD |     |        |        |             |
|-------------------|-----|--------|--------|-------------|
| Kod               | O'q | X      | Y      | O'lcham     |
| U1                | 2-B | 6 050  | 6 300  | 400 × 400   |
| U2                | 3-B | 12 050 | 6 300  | 400 × 400   |
| U3                | 4-B | 18 050 | 6 300  | 400 × 400   |
| U4                | 2-C | 6 050  | 12 300 | 400 × 400   |
| U5                | 3-C | 12 050 | 12 300 | 400 × 400   |
| U6                | 4-C | 18 050 | 12 300 | 400 × 400   |
| U7                | 2-D | 6 050  | 18 450 | 400 × 400   |
| U8                | 3-D | 12 050 | 18 450 | 400 × 400 * |
| U9                | 4-D | 18 050 | 18 450 | 400 × 400 * |

Koordinata — ichki yuzaning yuqori-chap burchagidan, ustun markazi bo'yicha; o'qlar taxminiy. \* U8, U9 fotoda ko'rinmaydi — to'r bo'yicha qo'yilgan (devor ichida), joyida tekshirilsin.

**PARTA TO'RI (Xadra filiali)**

parta 1400 × 600 (2 kishilik) · stul 380 × 420  
qatorda 4 parta (8 o'rin) · yo'lak 600 · deraza tomonda devorgacha 200  
3 qator · qadam 1 300 (parta 600 + stul va o'tish 700)  
doskadan 1-partagacha 1 850 · oxirgi parta 5 050 · sig'im 24  
ISTISNO: SR3 — doska va ustoz joyi kirish tomonida (buyurtmachi), deraza o'quvchilarning o'ng tomonida; SR4 — 4 + 4 + 2 parta, 20 o'rin (doska o'ng tashqi devorda)  
Beruniy standarti: parta 690 × 500 (1 kishilik), 2 + 2 + 2 × 4 qator, qadam 1 300, doskadan 2 440, oxirgi 6 840  
ustundan: oldi/orqa 500 · yon 0. Doska 3000 yon (kar) devorda, deraza o'quvchilarning chap tomonida (SR3 dan tashqari); eshiklar 900.  
K1, K2 koridorlari 1500. Yangi devorlar — GKL 100; sinflarning koridor tomoni — akustik shisha.  
KW: o'ng tomonda ~1,6 m o'tish yo'lagi bo'sh (6-xona — ZN1 ga o'tish, K1, K2, kirish zali); sahna — XZ1 devorida, podiumsiz.  
Ayollar WC: 2 kabina eng ichkarida (2, 3 — unitaz), oldida tambur (4, 5 — rakovina); ikki eshik orqali kiriladi.  
Ofis xonalari (XZ1–XZ4): eshik tomoni shisha devor; barcha yangi eshiklar shisha.  
XZ3 — ustozlar xonasi, XZ4 — call-markaz va online sotuv; 12-xona — CEO (mavjud holicha).  
Zinalar mavjud holicha; 1-qavatda zina oldida resepsn va turniket.



| SHARTLI BELGILAR                              |                                                       |
|-----------------------------------------------|-------------------------------------------------------|
| kesilgan ichki devor                          | kesilgan tashqi devor                                 |
| mavjud ustun 400 × 400                        | taxminiy ustun (fotoda yo'q)                          |
| deraza (joyi taxminiy)                        | parta 1400 × 600 (2 kishilik)                         |
| stul 380 × 420                                | doska (kar devorda)                                   |
| o'qituvchi / xodim stoli                      | shisha devor (koridor tomoni)                         |
| yorituvchi logotip (koridor oxiri, GKL devor) | e'lonlar doskasi                                      |
| e'tirof doskasi (faxriylar, oy o'quvchisi)    | koworking sahnasi (XZ1 devori): logotip, ekran, reyka |

| PDP Academy · Xadra filiali                                                     |                  |         |       |
|---------------------------------------------------------------------------------|------------------|---------|-------|
| Chizma                                                                          | Jihozlash rejasi |         |       |
| Manba: mavjud holat chizmasi (foto), 2-qavat · umumiy 617 m², foydali 557,74 m² |                  |         |       |
| Toshkent sh., Xadra — 2-qavat                                                   |                  |         |       |
| Masshtab                                                                        | Sana             | Versiya | Varaq |
| 1:100                                                                           | 09.10.2026       | v1.2    | 2 / 3 |

