


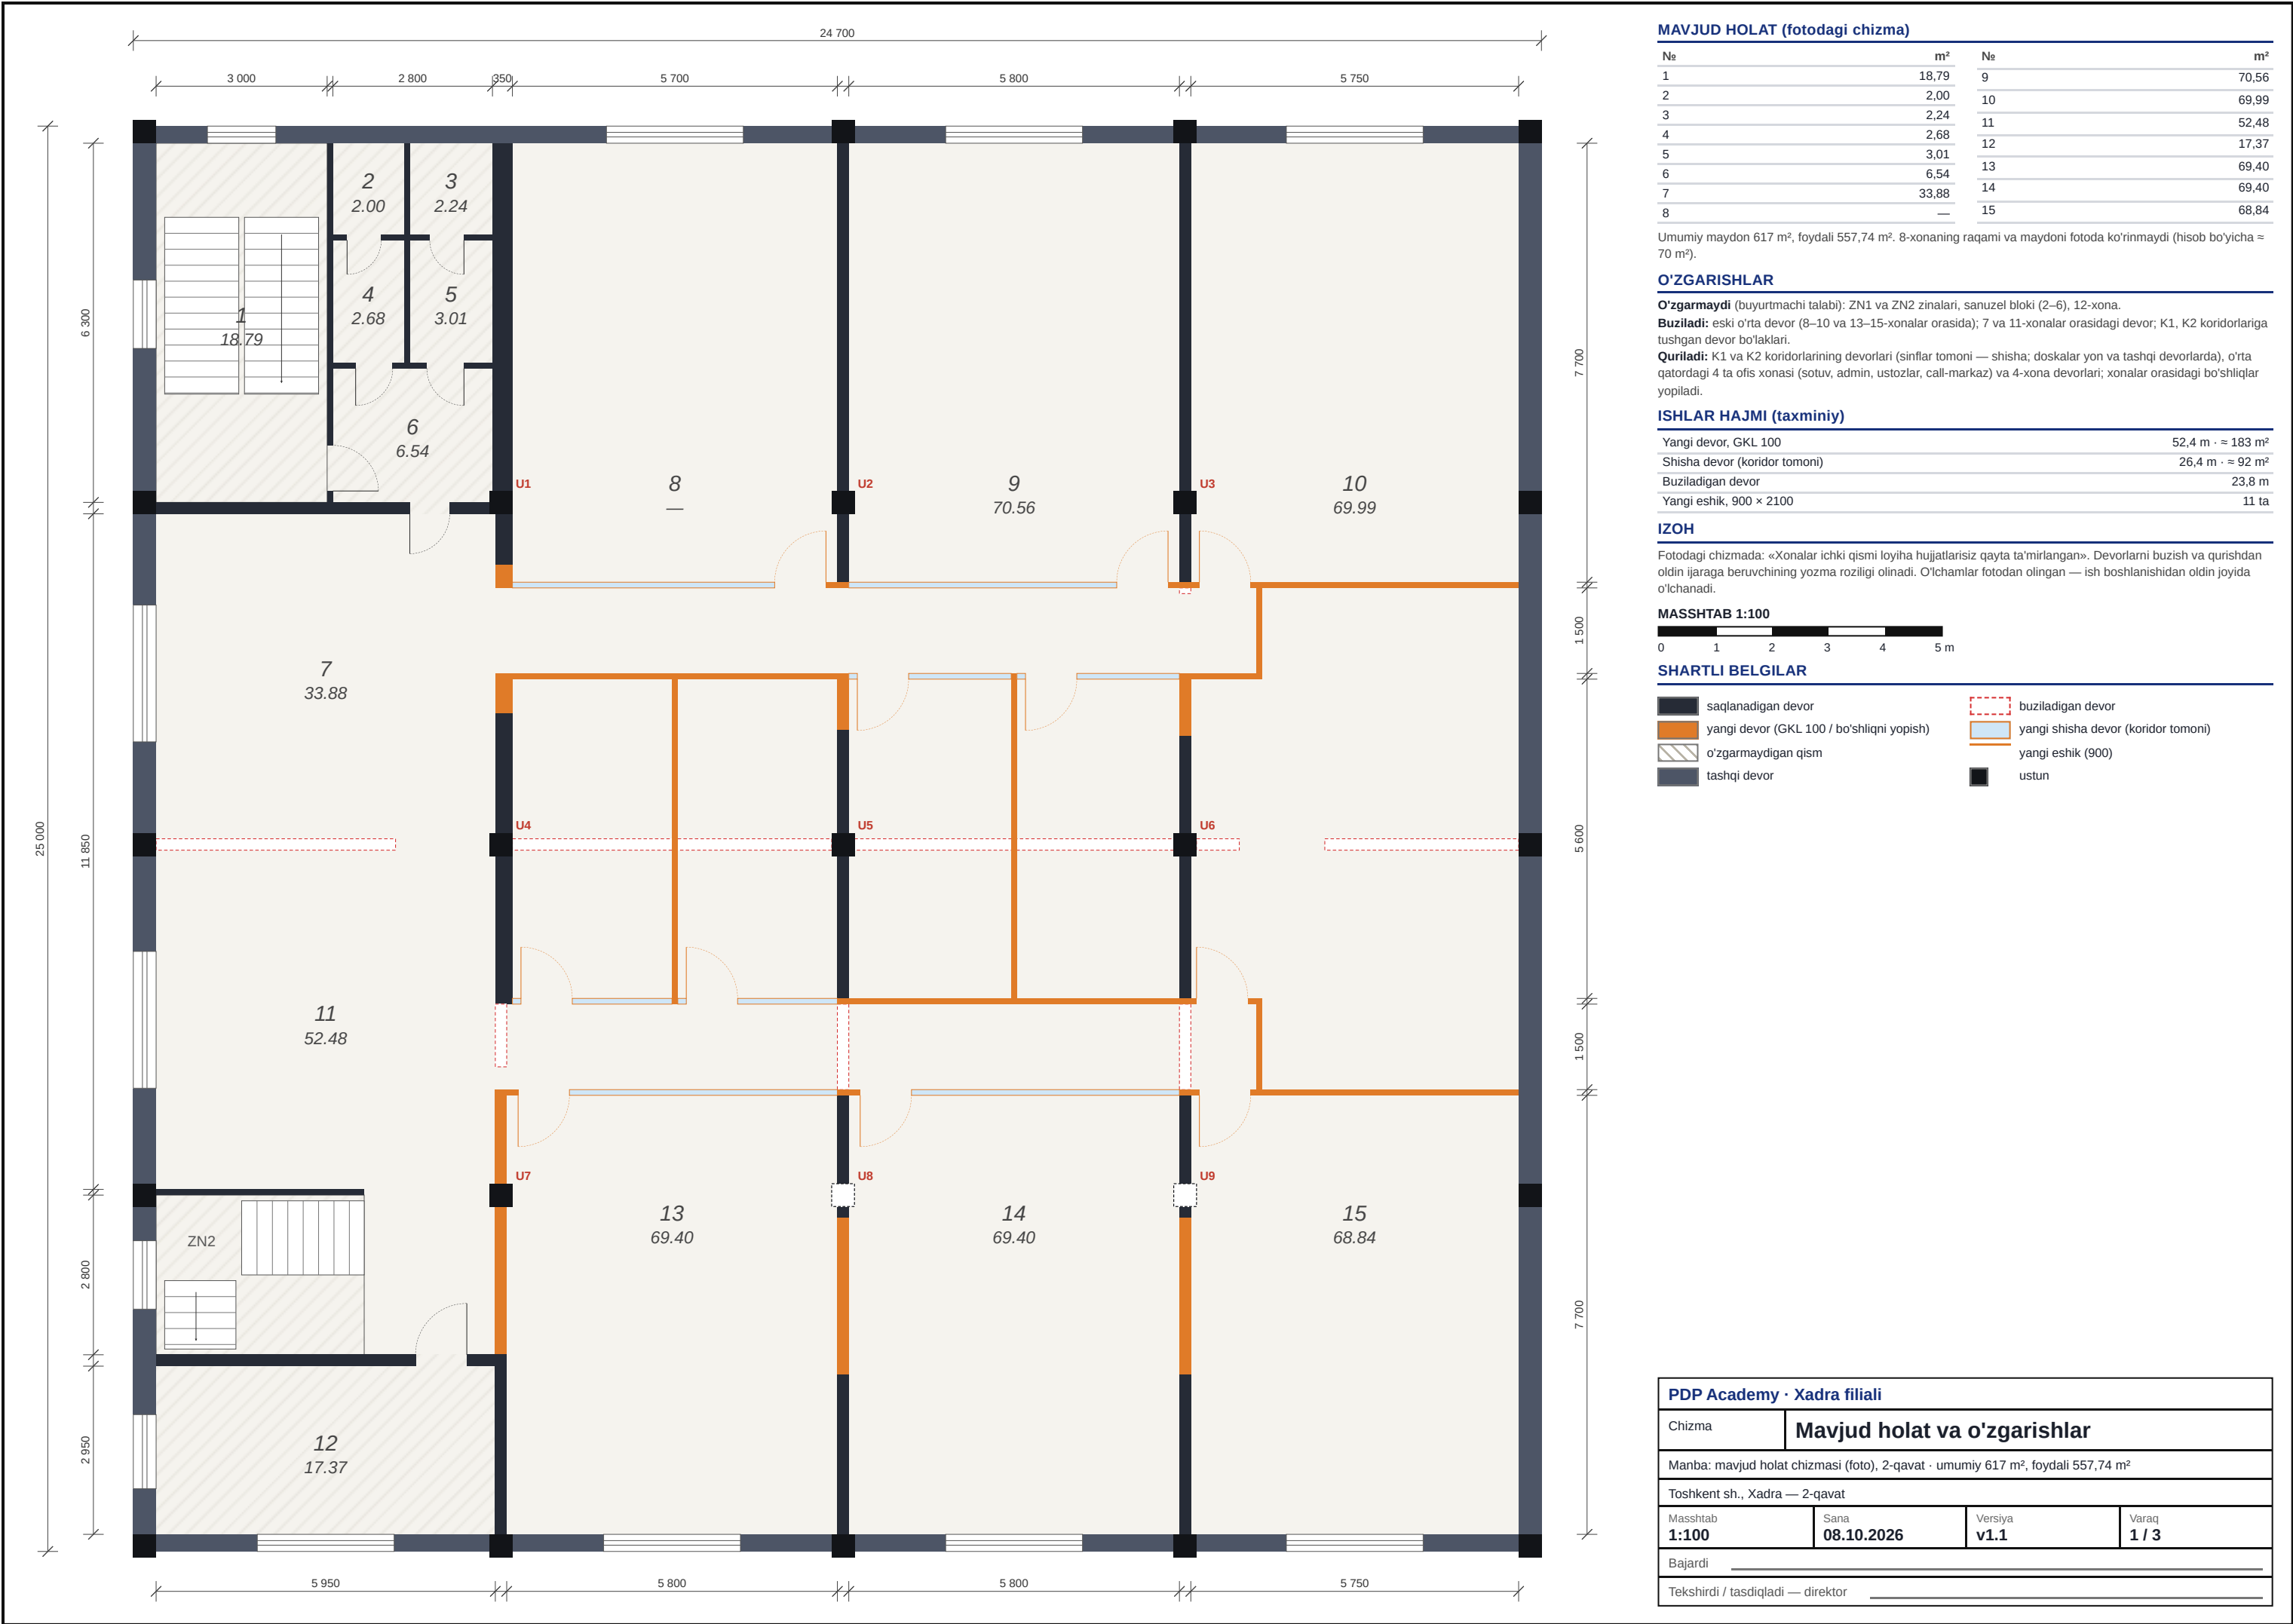

MAVJUD HOLAT (fotodagi chizma)

№	m²	№	m²
1	18,79	9	70,56
2	2,00	10	69,99
3	2,24	11	52,48
4	2,68	12	17,37
5	3,01	13	69,40
6	6,54	14	69,40
7	33,88	15	68,84
8	—		

Umumiy maydon 617 m², foydali 557,74 m². 8-xonaning raqami va maydoni fotoda koʻrinmaydi (hisob boʻyicha ≈ 70 m²).

OʻZGARISHLAR

Oʻzgarmaydi (buyurtmachi talabi): ZN1 va ZN2 zinalari, sanuzel bloki (2–6), 12-xona.
Buziladi: eski oʻrta devor (8–10 va 13–15-xonalar orasida); 7 va 11-xonalar orasidagi devor; K1, K2 koridorlariga tushgan devor boʻlaklari.
Quriladi: K1 va K2 koridorlarining devorlari (sinflar tomoni — shisha; doskalar yon va tashqi devorlarda), oʻrta qatordagi 4 ta ofis xonasi (sotuv, admin, ustozlar, call-markaz) va 4-xona devorlari; xonalar orasidagi boʻshliqlar yopiladi.

ISHLAR HAJMI (taxminiy)

Yangi devor, GKL 100	52,4 m · ≈ 183 m²
Shisha devor (koridor tomoni)	26,4 m · ≈ 92 m²
Buziladigan devor	23,8 m
Yangi eshik, 900 × 2100	11 ta

IZOH

Fotodagi chizmada: «Xonalar ichki qismi loyiha hujjatlarisiz qayta taʼmirlangan». Devorlarni buzish va qurishdan oldin ijaraga beruvchining yozma roziligi olinadi. Oʻlchamlar fotodan olingan — ish boshlanishidan oldin joyida oʻlchanadi.

MASSHTAB 1:100



SHARTLI BELGILAR

saqlanadigan devor	buziladigan devor
yangi devor (GKL 100 / boʻshliqni yopish)	yangi shisha devor (koridor tomoni)
oʻzgarmaydigan qism	yangi eshik (900)
tashqi devor	ustun

PDP Academy · Xadra filiali

Chizma	Mavjud holat va oʻzgarishlar		
Manba: mavjud holat chizmasi (foto), 2-qavat · umumiy 617 m², foydali 557,74 m²			
Toshkent sh., Xadra — 2-qavat			
Mashtab 1:100	Sana 08.10.2026	Versiya v1.1	Varaq 1 / 3
Bajardi _____			
Tekshirdi / tasdiqladi — direktor _____			

PDP Academy · Xadra filiali			
Chizma	Havo almashinuvi sxemasi		
Manba: mavjud holat chizmasi (foto), 2-qavat · umumiy 617 m², foydali 557,74 m²			
Toshkent sh., Xadra — 2-qavat			
Masstab 1:100	Sana 08.10.2026	Versiya v1.1	Varaq 3 / 3
Bajardi _____			
Tekshirdi / tasdiqladi — direktor _____			