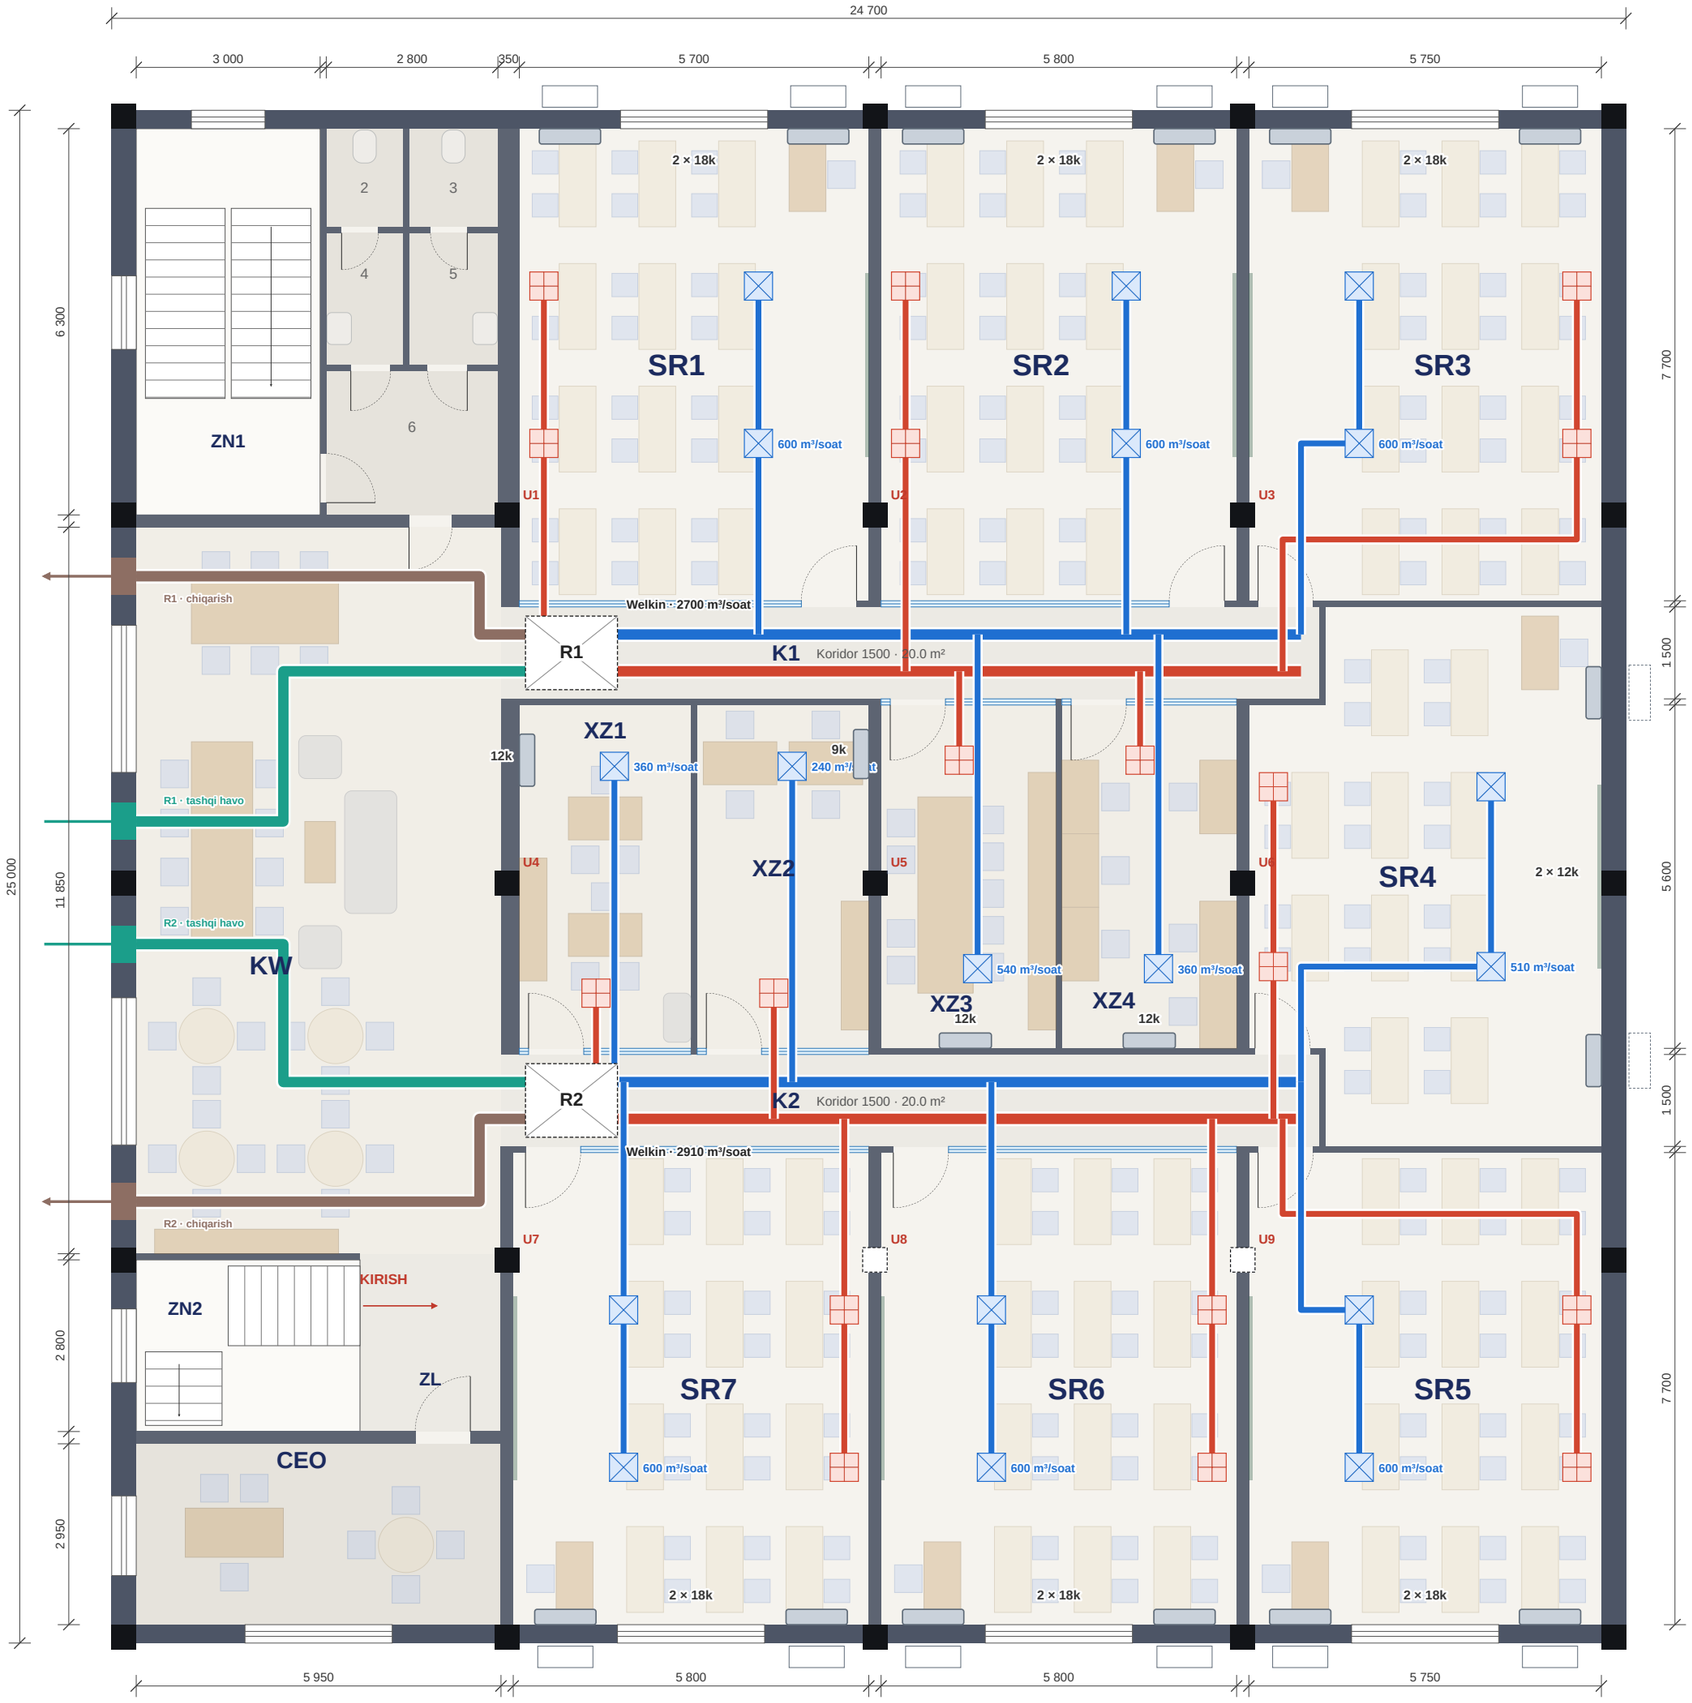


VENTILYATSIYA — 2 TA REKUPERATOR (WELKIN)

Qurilma	Xonalar	Loyiha, m³/soat	Me'yoriy min	Kanal
R1 · K1	SR1, SR2, SR3, XZ3, XZ4	2 700	2 537	600×300
R2 · K2	SR4, SR5, SR6, SR7, XZ1, XZ2	2 910	2 717	600×300
Jami		**5 610**	**5 253**	

XONALAR: TASHQI HAVO VA SPLIT

Xona	Odam	Havo, m³/soat	Rek.	CO_2, ppm	Yuk, kW	Split
SR1	25	600	R1	1 170	5.1–7.6	**2 × 18k**
SR2	25	600	R1	1 170	5.1–7.6	**2 × 18k**
SR3	25	600	R1	1 170	5.1–7.6	**2 × 18k**
SR4	21	510	R2	1 161	4.2–5.5	**2 × 12k**
SR5	25	600	R2	1 170	5.1–7.6	**2 × 18k**
SR6	25	600	R2	1 170	5.1–7.6	**2 × 18k**
SR7	25	600	R2	1 170	5.1–7.6	**2 × 18k**
XZ1	6	360	R2	720	1.9–2.3	**12k**
XZ2	4	240	R2	720	1.4–1.8	**9k**
XZ3	9	540	R1	720	2.3–2.7	**12k**
XZ4	6	360	R1	720	2.5–2.9	**12k**
KW	70	1400	—		12.5–17.0	**2 × 36k kas.**
X12	7	—	—		1.5–4.1	**1 × 18k**

HISOB ASOSI

Tashqi havo: sinflarda 24 m³/soat·kishi (me'yoriy ~22), derazasiz xizmat xonalarida 60 m³/soat·kishi (KMK). Har rekuperator 2500–3000 m³/soat: R2 ga 2 910 m³/soat kerak — **3000 m³/soatlik model** (kanal qarshiligi ~300 Pa da).

Split: xona yuklamasi (odamlar 115 W/kishi, yoritish, panel/kompyuter, devor-oyna-tom oralig'i) + rekuperatordan keyingi tashqi havo qoldig'i (FIK 55%); tanlov — 42–43 °C da (quvvat ~87%) yuqori chegarani qoplaydi. Sinflarda 2 tadan blok — havo bir tekis taqsimlanadi.

Toza havo doska oldida beriladi, orqa devor yonida so'riladi. Kanallar koridorlar osma shifti ichida (~2.8 m), koworkingda — shift ostida (fasadgacha). Tashqi bloklar fasadda; SR4 va xizmat xonalarinikini — tomda yoki o'ng devor ortidagi oraliqda (aniqlanadi). Kanallar yo'nalishi — taklif, buyurtmachi o'zgartirishi mumkin.

MASSHTAB 1:100

0 1 2 3 4 5 m

SHARTLI BELGILAR

- R1, R2 — Welkin rekuperatori (koridor shiftida)
- so'rish kanali (xonalardan rekuperatorga)
- chiqarish kanali (fasadga)
- so'rish panjarasi
- split — tashqi blok (fasadda; punktir — joyi aniqlanadi)
- toza havo kanali (rekuperatordan xonalarga)
- tashqi havo kanali (fasaddan)
- toza havo diffuzori
- split — ichki blok (devorda), yozuv: BTU/soat

PDP Academy · Xadra filiali	
Chizma	**Ventilyatsiya va konditsionerlash**
Manba: mavjud holat chizmasi (foto), 2-qavat · umumiy 617 m², foydali 557,74 m²	
Toshkent sh., Xadra — 2-qavat	
Masshtab **1:100** · Sana **09.10.2026** · Versiya **v1.2** · Varaq **3 / 3**	
Bajardi	
Tekshirdi / tasdiqladi — direktor	