1-varaq · Devorlar va eshiklar rejasi (butun qavat), 1:100



DEVORLAR VA ESHIKLAR — UMUMIY REJA

- mavjud devor / ustun (saqlanadi)
- yangi shisha devor (S…)
- yangi shisha eshik (E…), yoy — ochilishi
- zina panjarasi (P1), metall
- yangi GKL devor, 100 mm
- buziladigan devor
- ustun — joyida tekshiriladi

Xonalar: ichki o'lchamlari (devor yuzidan devor yuzigacha)

Xona	Eni × chuqurligi, mm	Maydon, m²
1-xona	5 700 × 7 700	43.9
2-xona	5 800 × 7 700	44.6
3-xona	5 750 × 7 700	44.2
4-xona	5 750 × 5 600	32.2
5-xona	5 750 × 7 700	44.2
6-xona	5 800 × 7 700	44.6
7-xona	5 800 × 7 700	44.6
XZ1 · sotuv	5 700 × 2 600	14.8
XZ2 · admin	5 800 × 2 600	15.1
XZ3 · ustozlar	5 800 × 2 800	16.2
XZ4 · call-markaz	5 700 × 2 800	16.0
Koworking	5 950 × 11 850	70.5
CEO	5 950 × 2 950	17.6
KL1 · kladovka	2 800 × 1 500	4.2
KL2 · kladovka	2 800 × 1 500	4.2
Kirish zali	2 300 × 2 900	6.6

Devor turlari

- **GKL 100:** metall profil 75 mm (stoyka qadami 600), ikki tomonida 12.5 mm gipsokarton; ichida 50 mm mineral paxta (shovqin uchun, tavsiya); poldan shiftgacha 3 500 mm.
- **Shisha devor:** poldan 2 500 mm gacha shisha (laminatlangan, kamida 2 × 6 mm yoki 10 mm toblangan), alyumin profilda; 2 500–3 500 mm — GKL (shisha ustida). 1 000–1 600 mm da matli plyonka.
- **Eshiklar (founder, 16.10):** shisha, 1 000 × 2 100 mm, **yonga suriladigan** (Damas eshigi kabi): barg xona ichida, yuqori relsda devor bo'ylab suriladi, ochilganda yonidagi shisha oldida turadi; ustida 400 mm qo'zg'almas shisha. Kladovka eshiklari — 800 × 2 100, ichkariga ochiladi. Jadvali — 2-varaqda.
- **Bo'shliqlarni yopish** (eski eshik va o'tish joylari, 1-varaqdagi to'q sariq bo'laklar) — GKL, mavjud devor qalinligida (200–300 mm), ikki tomoni tekislanadi.
- **4-xona doska devori (17.10):** g'arbiy mavjud devorga GKL qoplama 100 mm (profil 75 + 12.5 mm ikki qatlam), U6 ustuni yuzi bilan tekis — interaktiv doska va bambuk panel shu yuzaga; doska eshik tomonida.


Buyurtmachi va founder (16.10): K1 va K2 koridorlari 4-xona orqali uning o'rtasigacha (x 21 000) davom etadi; oxirida ko'ndalang GKL devor va eshik — orqasi **kladovka** (KL1, KL2), ustida kanalli konditsioner. 3-, 4-, 5-xonaning koridor tomoni kladovkagacha shisha; 4-xona kichrayadi (5.75 × 5.6 m). Barcha 11 eshik — 1 m, suriladigan.
Buyurtmachi qarorlari (14.10): (1) xizmat xonalari zonasidagi **eski o'rta devor (C o'qi) buzilmaydi** — 2 × 2 xona: K2 tomonda XZ1 sotuv va XZ2 admin (yonma-yon, eshiklari o'rtada), K1 tomonda XZ4 call-markaz va XZ3 ustozlar; koridor tomoni shisha. (2) **Kirishdagi ZN2 zinasi bilan koworking orasidagi devor buziladi** — o'rniga zina tuynugi chetida metall panjara P1 (h 1 100, uzunligi 3 650).

Ishni boshlashdan oldin joyida tekshiriladi

- Barcha o'lchamlar mavjud chizma fotosidan olingan: ish boshlashdan oldin ustunlar (U1–U9) va mavjud devorlar yuzasi o'lchab chiqiladi; farq 30 mm dan katta bo'lsa — loyihachiga xabar beriladi.
- U8, U9 ustunlari fotoda ko'rinmaydi — U7 bilan bir chiziqda deb olingan (punktir).
- Shisha devorlar GKL karkas va eshik o'rinlari belgilangandan keyin **joyida o'lchanib** buyurtma qilinadi (jadvaldagi o'lchamlar — loyiha bo'yicha).
- Poldan shiftgacha 3 500 mm (buyurtmachi); to'sinlar bo'lsa, GKL va shisha ustidagi qism moslanadi.
- ZN2 devorini buzishdan oldin: devor yuk ko'taruvchi emasligi va zinapoya to'sig'i bo'yicha yong'in xavfsizligi talabi tekshiriladi (ijaraga beruvchi va yong'in nazorati bilan kelishiladi). Panjara: balandligi 1 100 mm, tik ustunchalar orasi ≤ 110 mm (bolalar uchun xavfsiz).

PDP Academy · Xadra filiali

Chizma	**Devorlar va eshiklar rejasi (o'lchamli)**
Ish chizmasi — ustalar uchun. Toshkent sh., Xadra — 2-qavat	
Masshtab: 1:100	Sana: 14.10.2026
Versiya: v1.2	Varaq: 1 / 2
Bajardi: _____	Tekshirdi: _____

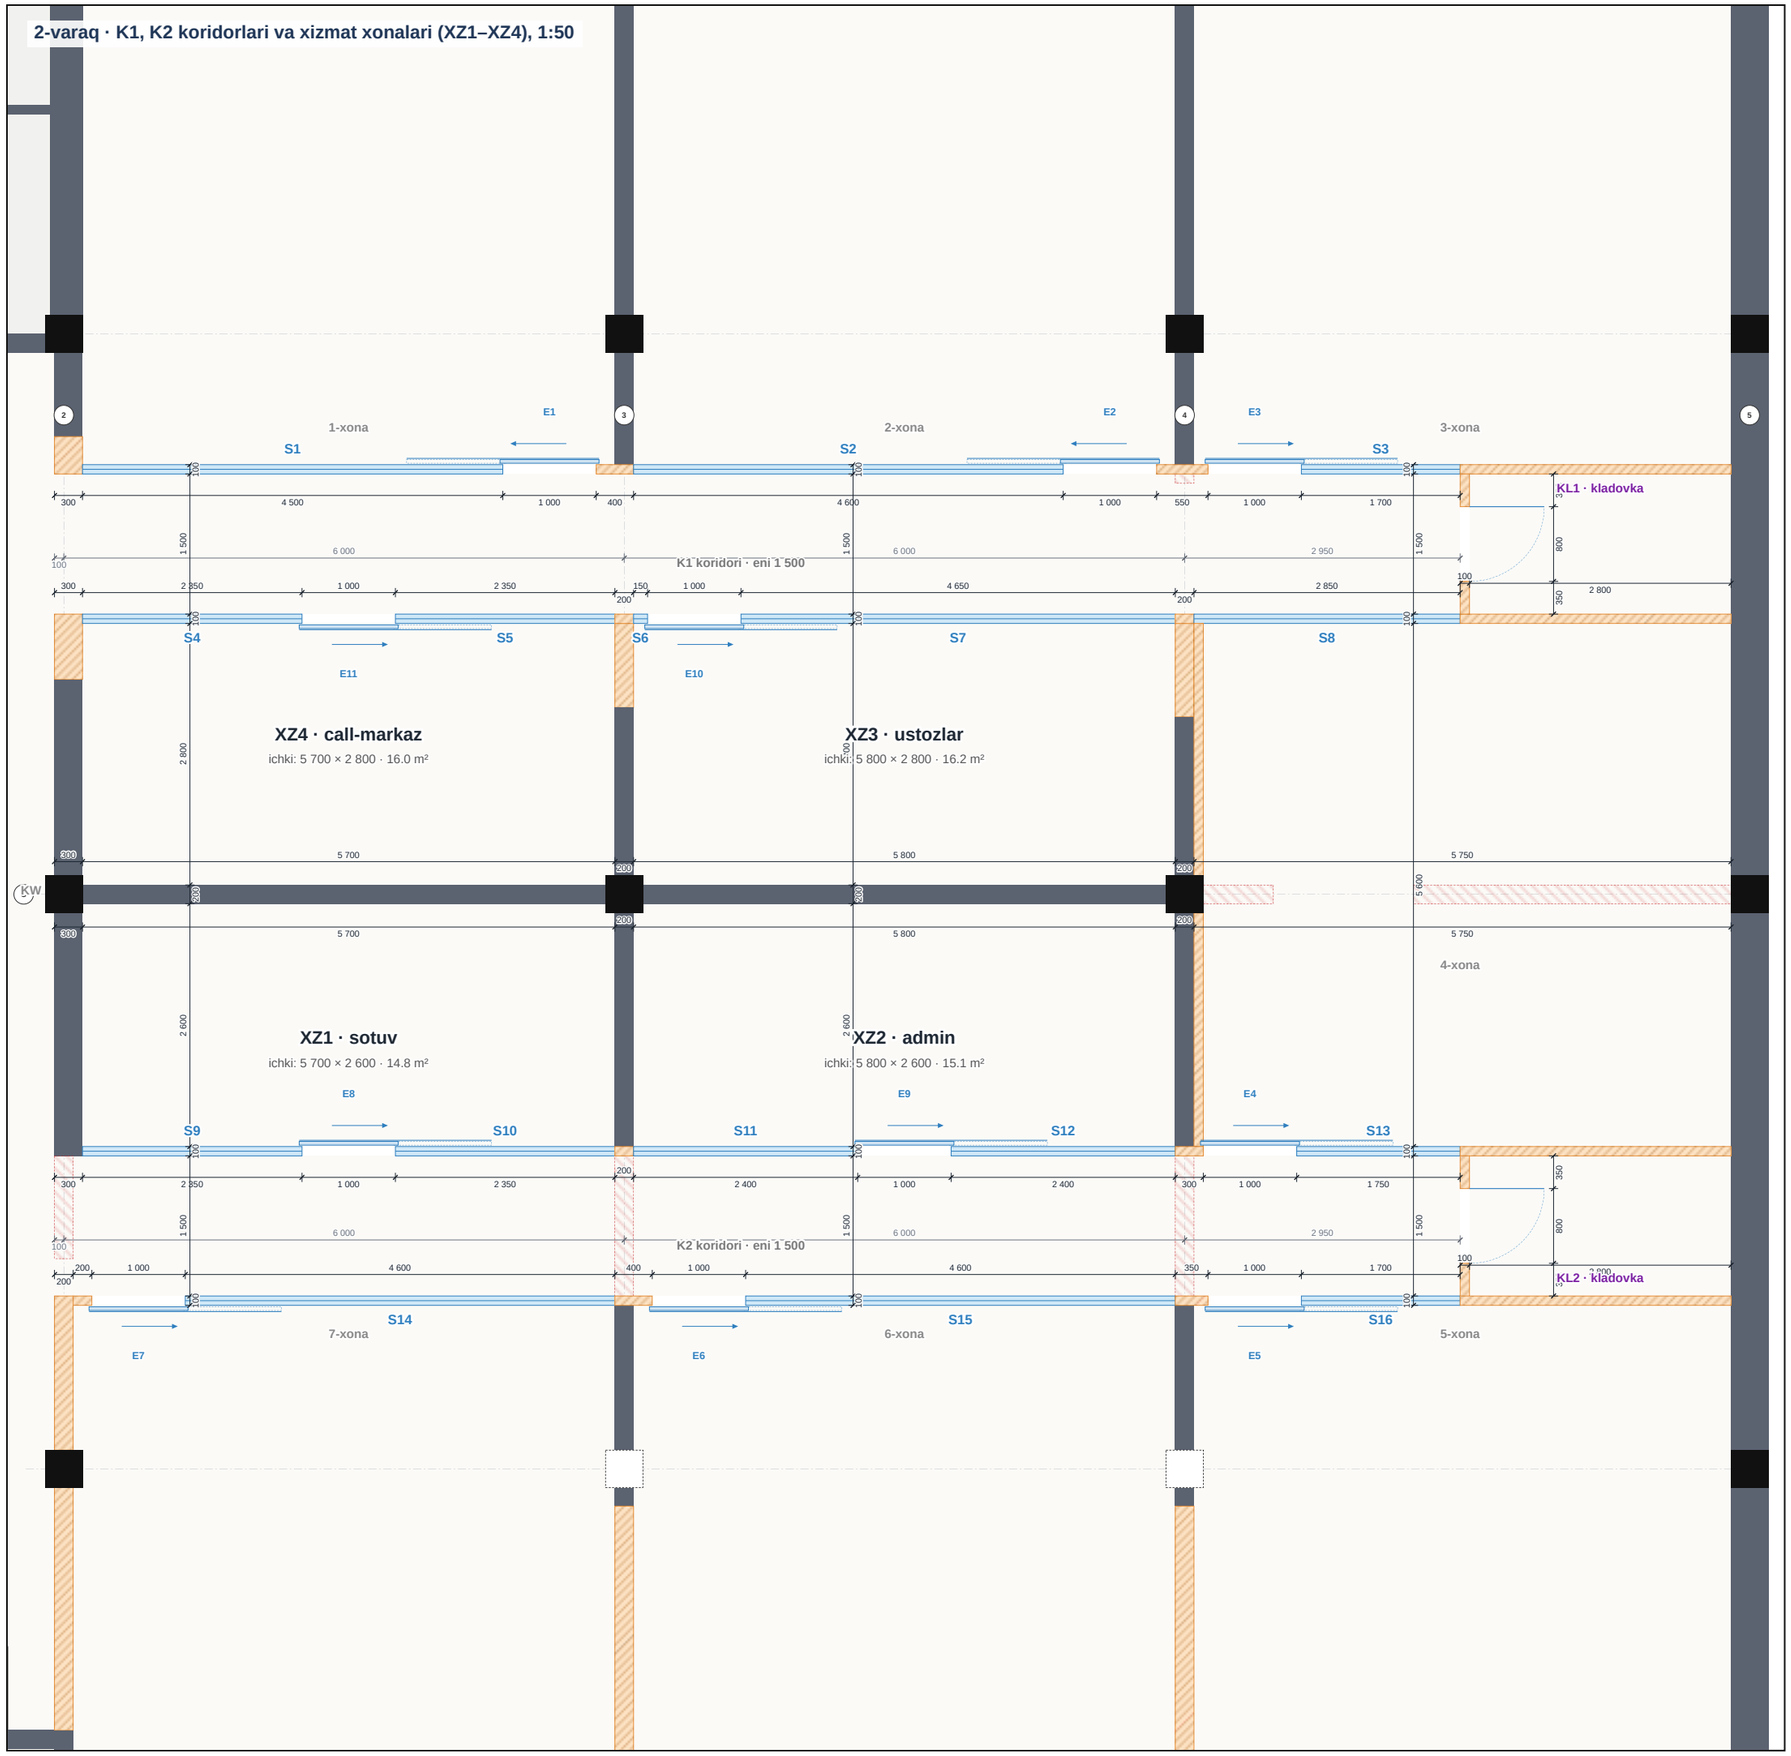

SHISHA DEVORLAR, ESHIKLAR VA GKL — JADVALLAR

Eshiklar (yangi) — 13 ta: 11 ta shisha suriladigan (1 m, barg xona ichida) va 2 ta kladovka eshigi


Kod	Xona	Joyi	x, mm	O'lchami	Turi (koridordan qaraganda)
E1	1-xona	K1 shimoliy devori	10 750–11 750	1 000 × 2 100	suriladi chapga
E2	2-xona	K1 shimoliy devori	16 750–17 750	1 000 × 2 100	suriladi chapga
E3	3-xona	K1 shimoliy devori	18 300–19 300	1 000 × 2 100	suriladi o'ngga
E4	4-xona	K2 shimoliy devori	18 250–19 250	1 000 × 2 100	suriladi o'ngga
E5	5-xona	K2 janubiy devori	18 300–19 300	1 000 × 2 100	suriladi chapga
E6	6-xona	K2 janubiy devori	12 350–13 350	1 000 × 2 100	suriladi chapga
E7	7-xona	K2 janubiy devori	6 350–7 350	1 000 × 2 100	suriladi chapga
E8	XZ1 · sotuv	K2 shimoliy devori	8 600–9 600	1 000 × 2 100	suriladi o'ngga
E9	XZ2 · admin	K2 shimoliy devori	14 550–15 550	1 000 × 2 100	suriladi o'ngga
E10	XZ3 · ustozlar	K1 janubiy devori	12 300–13 300	1 000 × 2 100	suriladi chapga
E11	XZ4 · call-markaz	K1 janubiy devori	8 600–9 600	1 000 × 2 100	suriladi chapga
E12	KL1 · kladovka	K1 oxiri (x 21 000)	8 150–8 950	800 × 2 100	ochiladi, ichkariga
E13	KL2 · kladovka	K2 oxiri (x 21 000)	15 450–16 250	800 × 2 100	ochiladi, ichkariga

Shisha devorlar (S) — balandligi 2 500 mm

Kod	Joyi	x, mm	Uzunligi	m²
S1	K1 shimoliy devori	6 250–10 750	4 500	11.25
S2	K1 shimoliy devori	12 150–16 750	4 600	11.50
S3	K1 shimoliy devori	19 300–21 000	1 700	4.25
S4	K1 janubiy devori	6 250–8 600	2 350	5.88
S5	K1 janubiy devori	9 600–11 950	2 350	5.88
S6	K1 janubiy devori	12 150–12 300	150	0.38
S7	K1 janubiy devori	13 300–17 950	4 650	11.63
S8	K1 janubiy devori	18 150–21 000	2 850	7.13
S9	K2 shimoliy devori	6 250–8 600	2 350	5.88
S10	K2 shimoliy devori	9 600–11 950	2 350	5.88
S11	K2 shimoliy devori	12 150–14 550	2 400	6.00
S12	K2 shimoliy devori	15 550–17 950	2 400	6.00
S13	K2 shimoliy devori	19 250–21 000	1 750	4.38
S14	K2 janubiy devori	7 350–11 950	4 600	11.50
S15	K2 janubiy devori	13 350–17 950	4 600	11.50
S16	K2 janubiy devori	19 300–21 000	1 700	4.25
	Jami (eshiklarsiz)		**45 300**	**113.3**

Yangi GKL bo'laklari (to'q sariq) — eshik va ustunlar yonida; o'lchamlari zanjirlarda. Bo'shliqlarni yopish — 1-varaqda.

Shisha devor — tipik yoyilma (koridordan ko'rinish)

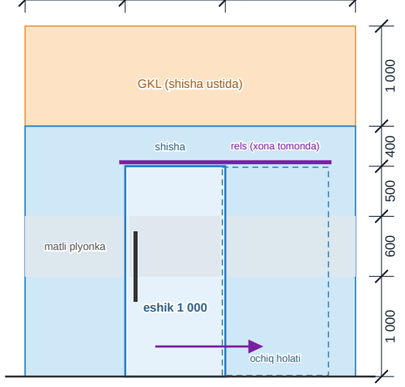

- Zanjirlar koridor ichida, koworking devori yuzasidan (x = 5 950) boshlanadi; o'qlar 2, 3, 4 — ustunlar markazi.
- XZ xonalari ichki eni 5 700 (XZ1, XZ2) va 5 800 (XZ3, XZ4); chuqurligi K1 tomonda 2 600, K2 tomonda 2 600 (o'rta devor 200 mm).

PDP Academy · Xadra filiali			
Chizma	**Koridorlar va xizmat xonalari — shisha, eshiklar**		
Ish chizmasi — ustalar uchun. Toshkent sh., Xadra — 2-qavat			
Masshtab 1:50	Sana 14.10.2026	Versiya v1.2	Varaq 2 / 2
Bajardi: _____	Tekshirdi: _____		