

MAVJUD HOLAT (fotodagi chizma)

№	m²	№	m²
1	18,79	9	70,56
2	2,00	10	69,99
3	2,24	11	52,48
4	2,68	12	17,37
5	3,01	13	69,40
6	6,54	14	69,40
7	33,88	15	68,84
8	—		

Umumiy maydon 617 m², foydali 557,74 m². 8-xonaning raqami va maydoni fotoda ko'rinmaydi (hisob bo'yicha ≈ 70 m²).

O'ZGARISHLAR

O'zgarmaydi (buyurtmachi talabi): ZN1 va ZN2 zinalari, sanuzel bloki devorlari (2–6; ichi — ayollar WC, 6 — ZN1 ga o'tish yo'lagi), 12-xona.
Buziladi: eski o'rta devor (8–10 va 13–15-xonalar orasida); 7 va 11-xonalar orasidagi devor; K1, K2 koridorlariga tushgan devor bo'laklari.
Quriladi: K1 va K2 koridorlarining devorlari (sinflar tomoni — shisha; doskalar yon va tashqi devorlarda), o'rta qatordagi 4 ta ofis xonasi (sotuv, admin, ustozlar, call-markaz) va 4-xona devorlari; xonalar orasidagi bo'shliqlar yopiladi.

ISHLAR HAJMI (taxminiy)

Yangi devor, GKL 100	52,4 m · ≈ 183 m²
Shisha devor (koridor tomoni)	26,4 m · ≈ 92 m²
Buziladigan devor	23,8 m
Yangi eshik, 900 × 2100	11 ta

IZOH

Fotodagi chizmada: «Xonalar ichki qismi loyiha hujjatlarisiz qayta ta'mirlangan». Devorlarni buzish va qurishdan oldin ijaraga beruvchining yozma roziligi olinadi. O'lchamlar fotodan olingan — ish boshlanishidan oldin joyida o'lchanadi.

MASSHTAB 1:100

0 1 2 3 4 5 m

SHARTLI BELGILAR

- saqlanadigan devor
- yangi devor (GKL 100 / bo'shliqni yopish)
- o'zgarmaydigan qism
- tashqi devor
- buziladigan devor
- yangi shisha devor (koridor tomoni)
- yangi eshik (900)
- ustun


PDP Academy · Xadra filiali

Chizma	**Mavjud holat va o'zgarishlar**
Manba: mavjud holat chizmasi (foto), 2-qavat · umumiy 617 m², foydali 557,74 m²	
Toshkent sh., Xadra — 2-qavat	

Masshtab	Sana	Versiya	Varaq
1:100	**09.10.2026**	**v1.2**	**1 / 4**

Bajardi _____

Tekshirdi / tasdiqladi — direktor _____

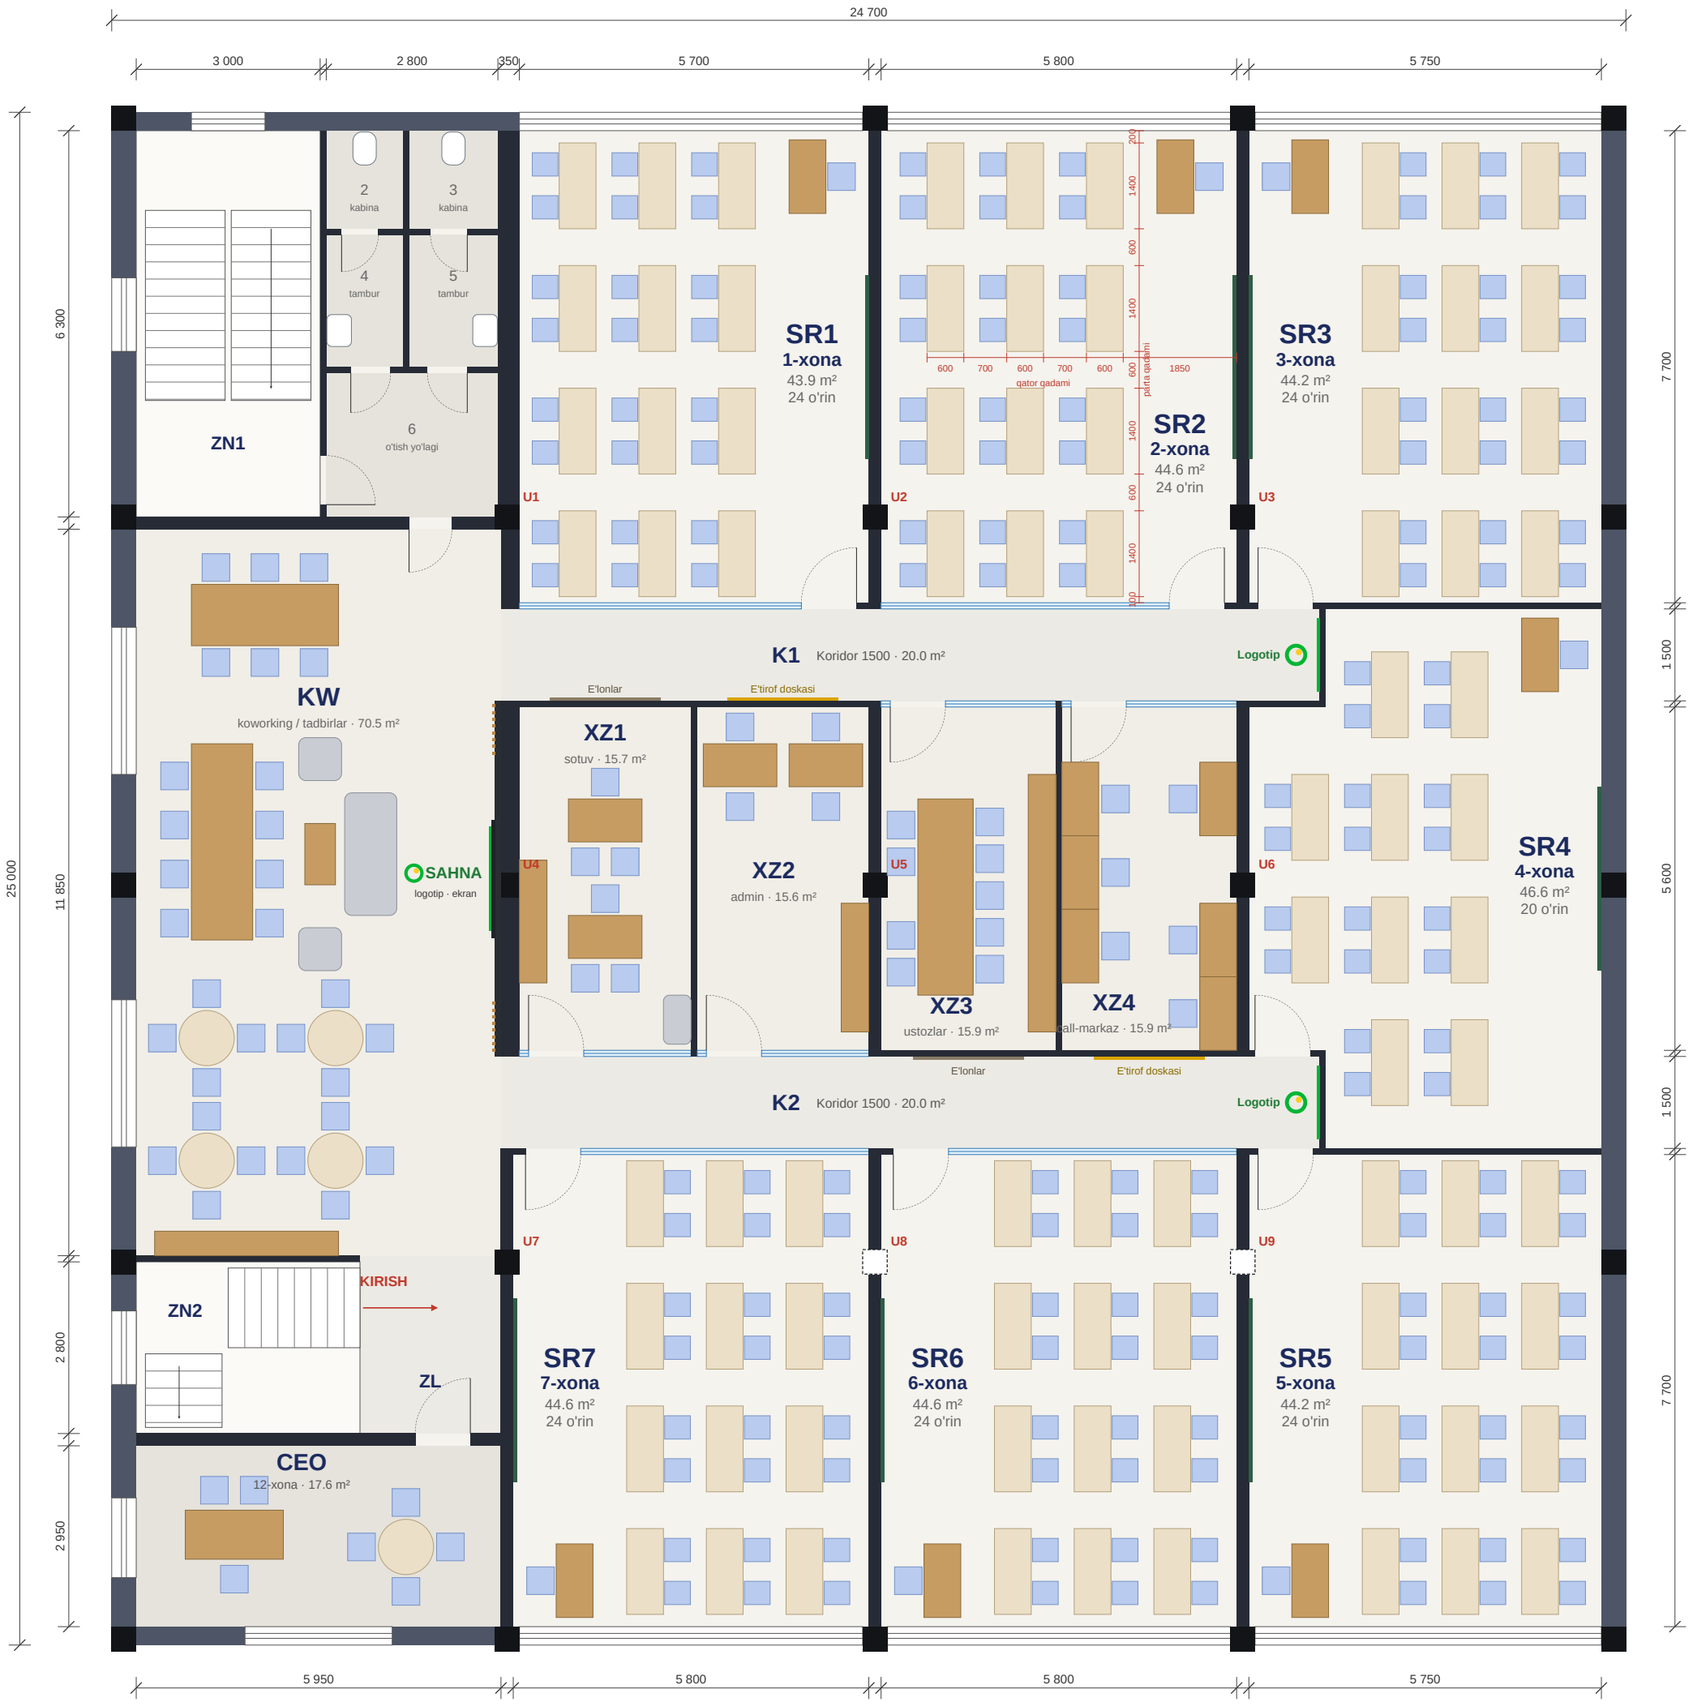

MAYDON

Ichki gabarit	23 900 × 24 400
Umumiy maydon (hujjat)	617 m²
Foydali maydon (hujjat)	557,74 m²
O'quv xonalari, 7 ta · 164 o'rin	312,6 m²
Offline sotuv (XZ1) va admin (XZ2)	31,3 m²
Ustozlar (XZ3), call-markaz (XZ4)	31,8 m²
Koworking / tadbirlar zali (KW)	70,5 m²
CEO xonasi (12-xona, o'zgarmaydi)	17,6 m²
Koridorlar K1, K2 va kirish zali ZL	46,7 m²
Zinalar, ayollar WC va o'tish yo'lagi (devorlari o'zgarmaydi)	45,8 m²
Balandlik (poldan shiftgacha)	3500 mm (buyurtmachi)

XONALAR

Xona	O'lcham, m	m²	O'rin	m²/kishi	Partalar
SR1 · 1-xona	7.70 × 5.70	43,9	24	1,8	4+4+4
SR2 · 2-xona	7.70 × 5.80	44,6	24	1,9	4+4+4
SR3 · 3-xona	7.70 × 5.75	44,2	24	1,8	4+4+4
SR4 · 4-xona	8.80 × 5.75 (L)	46,6	20	2,3	4+4+2
SR5 · 5-xona	7.70 × 5.75	44,2	24	1,8	4+4+4
SR6 · 6-xona	7.70 × 5.80	44,6	24	1,9	4+4+4
SR7 · 7-xona	7.70 × 5.80	44,6	24	1,9	4+4+4
XZ1 · sotuv	2.80 × 5.60	15,7	2	—	2 stol + 4 mijoz stuli, shisha devor
XZ2 · admin	2.80 × 5.60	15,6	2	—	2 stol + 2 mehmon stuli, shisha devor
XZ3 · ustozlar	2.85 × 5.60	15,9	9	—	umumiy stol, lokerlar
XZ4 · call-markaz	2.85 × 5.60	15,9	6	—	devor bo'ylab 6 ish o'rni
CEO (12-xona)	5.95 × 2.95	17,6	1	—	ish stoli + 4 kishilik stol, derazali
KW	5.95 × 11.85	70,5	~35	—	koworking; sahna — XZ1 devori, tadbirda 68 o'rin
Jami		**312,6**	**164**		**6 × 24 + 1 × 20**

USTUNLAR — MAVJUD

Kod	O'q	X	Y	O'lcham
U1	2-B	6 050	6 300	400 × 400
U2	3-B	12 050	6 300	400 × 400
U3	4-B	18 050	6 300	400 × 400
U4	2-C	6 050	12 300	400 × 400
U5	3-C	12 050	12 300	400 × 400
U6	4-C	18 050	12 300	400 × 400
U7	2-D	6 050	18 450	400 × 400
U8	3-D	12 050	18 450	400 × 400 *
U9	4-D	18 050	18 450	400 × 400 *

Koordinata — ichki yuzaning yuqori-chap burchagidan, ustun markazi bo'yicha; o'qlar taxminiy. * U8, U9 fotoda ko'rinmaydi — to'r bo'yicha qo'yilgan (devor ichida), joyida tekshirilsin.

PARTA TO'RI (Xadra filiali)

parta 1400 × 600 (2 kishilik) · stul 380 × 420
qatorda 4 parta (8 o'rin) · yo'lak 600 · deraza tomonda devorgacha 200
3 qator · qadam 1 300 (parta 600 + stul va o'tish 700)
doskadan 1-partagacha 1 850 · oxirgi parta 5 050 · sig'im 24
ISTISNO: SR3 — doska va ustoz joyi kirish tomonida (buyurtmachi), deraza o'quvchilarning o'ng tomonida; SR4 — 4 + 4 + 2 parta, 20 o'rin (doska o'ng tashqi devorda)
Beruniy standarti: parta 690 × 500 (1 kishilik), 2 + 2 + 2 × 4 qator, qadam 1 300, doskadan 2 440, oxirgi 6 840
ustundan: oldi/orqa 500 · yon 0. Doska 3000 yon (kar) devorda, deraza o'quvchilarning chap tomonida (SR3 dan tashqari); eshiklar 900.
K1, K2 koridorlari 1500. Yangi devorlar — GKL 100; sinflarning koridor tomoni — akustik shisha.
KW: o'ng tomonda ~1,6 m o'tish yo'lagi bo'sh (6-xona — ZN1 ga o'tish, K1, K2, kirish zali); sahna — XZ1 devorida, podiumsiz.
Ayollar WC: 2 kabina eng ichkarida (2, 3 — unitaz), oldida tambur (4, 5 — rakovina); ikki eshik orqali kiriladi.
Ofis xonalari (XZ1–XZ4): eshik tomoni shisha devor; barcha yangi eshiklar shisha.
XZ3 — ustozlar xonasi, XZ4 — call-markaz va online sotuv; 12-xona — CEO (mavjud holicha).
Zinalar mavjud holicha; 1-qavatda zina oldida resepshn va turniket.

MASSHTAB 1:100

0 1 2 3 4 5 m


SHARTLI BELGILAR

- kesilgan ichki devor
- kesilgan tashqi devor
- mavjud ustun 400 × 400
- taxminiy ustun (fotoda yo'q)
- deraza (joyi taxminiy)
- parta 1400 × 600 (2 kishilik)
- stul 380 × 420
- doska (kar devorda)
- o'qituvchi / xodim stoli
- shisha devor (koridor tomoni)
- yorituvchi logotip (koridor oxiri, GKL devor)
- e'lonlar doskasi
- e'tirof doskasi (faxriylar, oy o'quvchisi)
- koworking sahnasi (XZ1 devori): logotip, ekran, reyka

PDP Academy · Xadra filiali

Chizma	**Jihozlash rejasi**
Manba: mavjud holat chizmasi (foto), 2-qavat · umumiy 617 m², foydali 557,74 m²	
Toshkent sh., Xadra — 2-qavat	

Masshtab	Sana	Versiya	Varaq
1:100	09.10.2026	v1.2	2 / 4

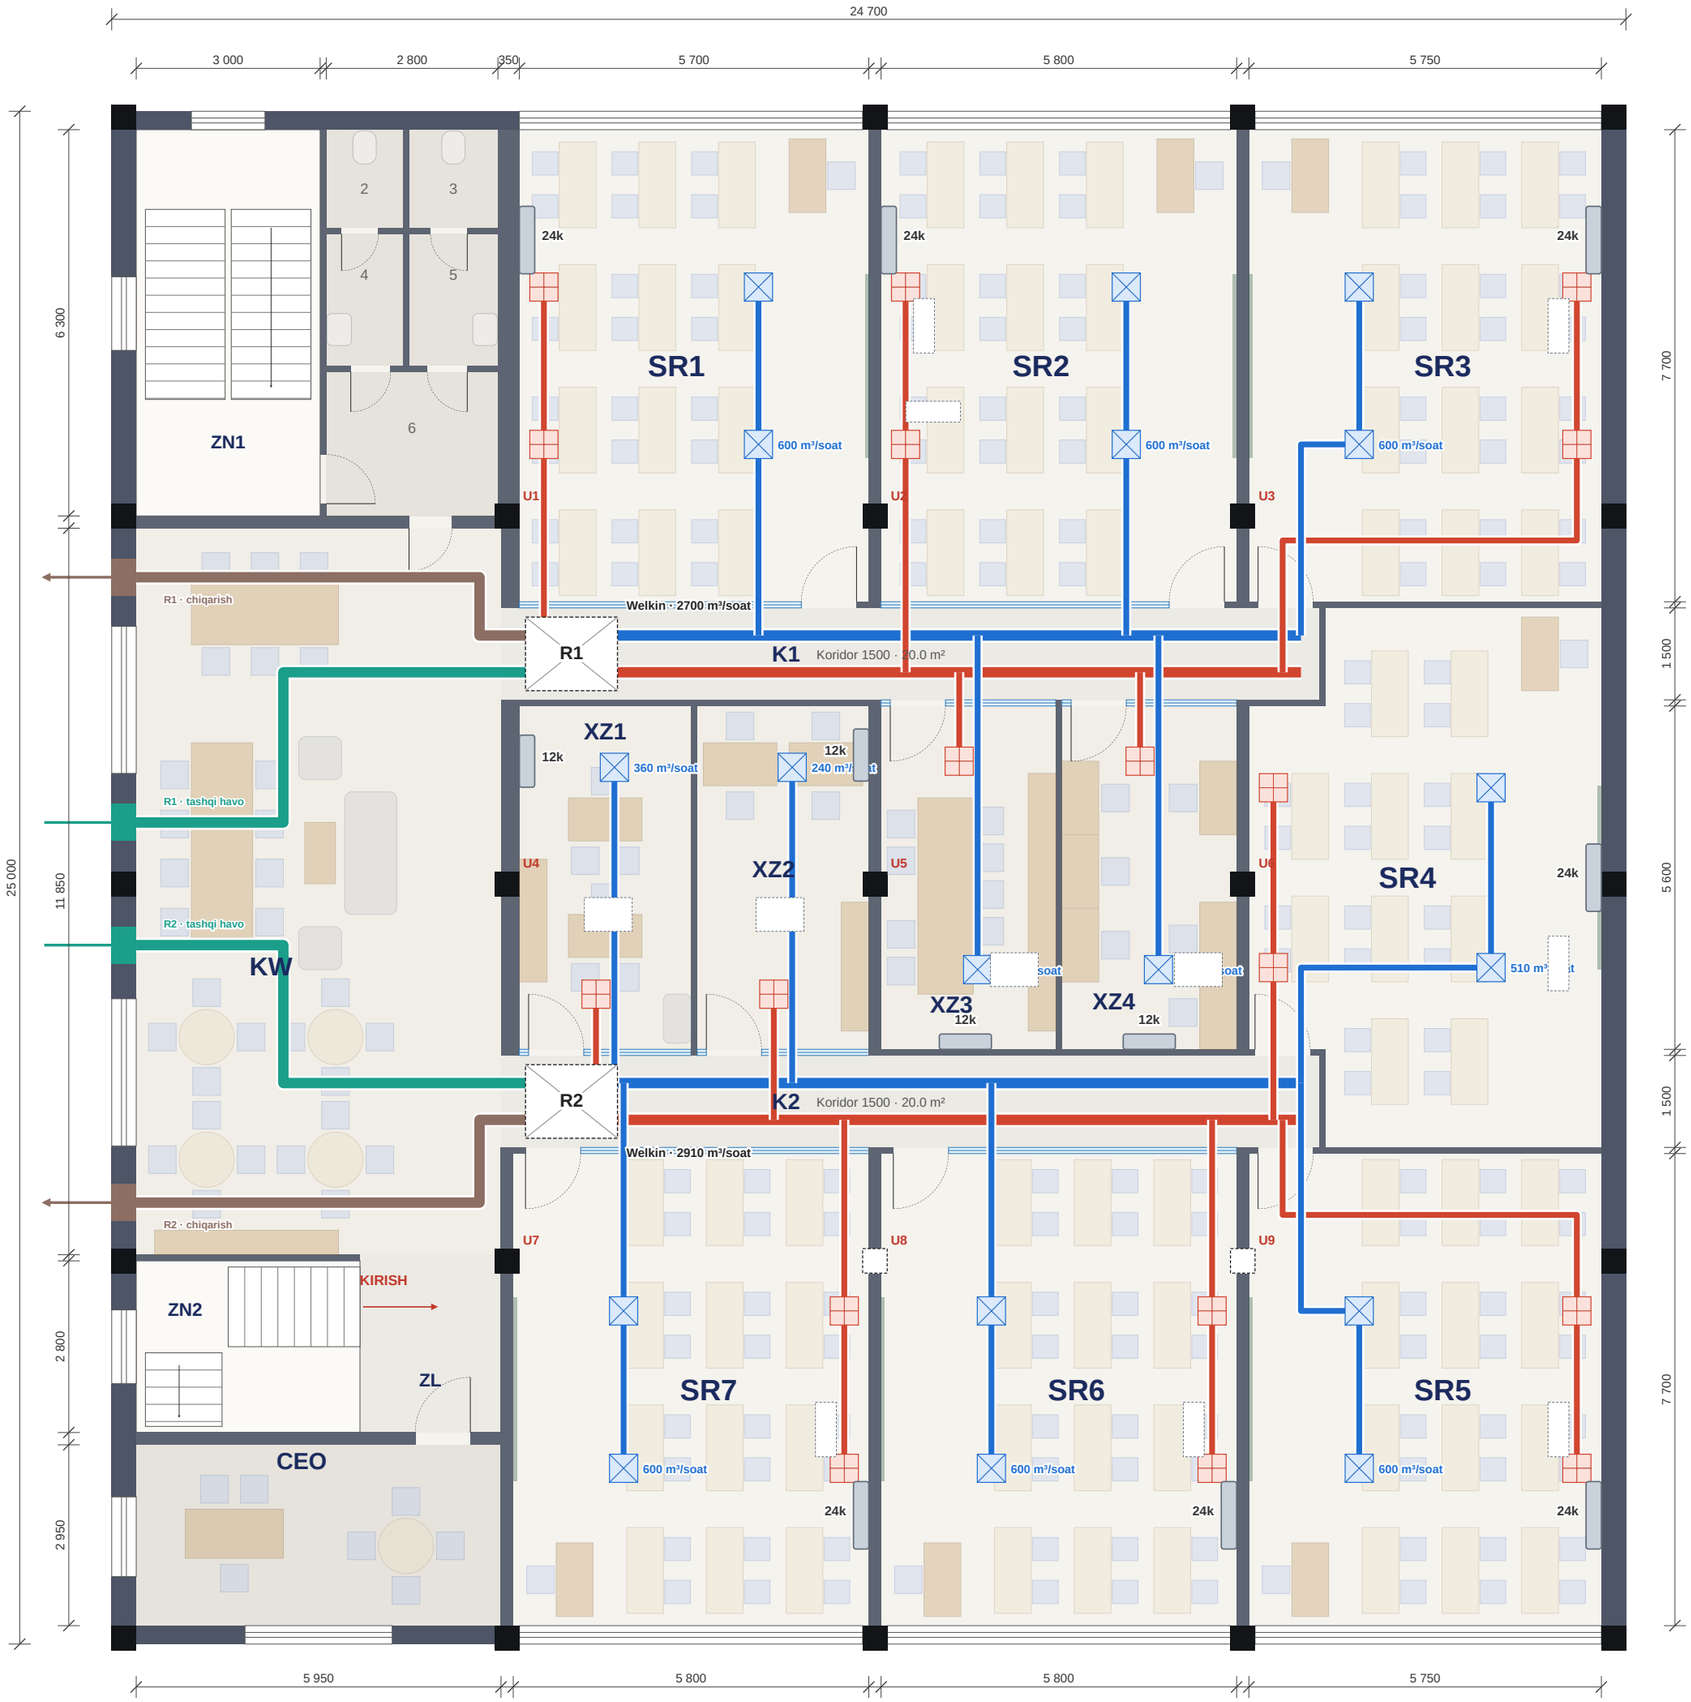

VENTILYATSIYA — 2 TA REKUPERATOR (WELKIN)

Qurilma	Xonalar	Loyiha, m³/soat	Me'yoriy min	Kanal
R1 · K1	SR1, SR2, SR3, XZ3, XZ4	2 700	2 537	600×300
R2 · K2	SR4, SR5, SR6, SR7, XZ1, XZ2	2 910	2 717	600×300
Jami	**havo kanallari ~223 m**	**5 610**	**5 253**	

XONALAR: TASHQI HAVO VA SPLIT (BUYURTMACHI TANLOVI)

Xona	Odam	Havo, m³/soat	Rek.	CO₂, ppm	Yuk, kW	Split
SR1	25	600	R1	1 170	7.5–8.1	**24k ✗**
SR2	25	600	R1	1 170	7.6–9.3	**24k ✗**
SR3	25	600	R1	1 170	7.6–9.3	**24k ✗**
SR4	21	510	R2	1 161	4.2–5.5	**24k ✓**
SR5	25	600	R2	1 170	8.0–9.4	**24k ✗**
SR6	25	600	R2	1 170	7.9–9.4	**24k ✗**
SR7	25	600	R2	1 170	7.9–9.4	**24k ✗**
XZ1	6	360	R2	720	1.9–2.3	**12k ✓**
XZ2	4	240	R2	720	1.4–1.8	**12k ✓**
XZ3	9	540	R1	720	2.3–2.7	**12k ✓**
XZ4	6	360	R1	720	2.5–2.9	**12k ✓**
KW	35/70	—	—		6.5–15.1	mavjud 24k + 18k
CEO	7	—	—			mavjud

HISOB ASOSI

Tashqi havo: sinflarda 24 m³/soat·kishi (me'yoriy ~22), derazasiz xizmat xonalarida 60 m³/soat·kishi (KMK). R2 ga 2 910 m³/soat kerak — **3000 m³/soatlik model** (kanal qarshiligi ~300 Pa da).

Split: yuk — odamlar (115 W/kishi), yoritish, panel/kompyuter, oynali fasad (quyosh: sharq — 9:00, g'arb — 16:00; steklopaket + reklama plyonkasi), devor, tom va rekuperatordan keyingi tashqi havo qoldig'i. ✓ — yetarli; ≈ — chegarada; ✗ — eng og'ir paytda kam (oynali sinflar: tavsiyalar — konditsionerlar chizmasi, 2-varaq). Ichki blok — orqa yon devorda, oynaga yaqin; tashqi bloklar — tomda (punktir). Koworkingdagi mavjud konditsionerlar koridorlarni ham sovutadi.

Toza havo doska oldida beriladi, orqa devor yonida so'riladi. Kanallar koridorlar osma shifti ichida (~2.8 m), koworkingda — shift ostida (fasadgacha). Kanallar yo'nalishi — taklif, buyurtmachi o'zgartirishi mumkin.

MASSHTAB 1:100

0 1 2 3 4 5 m

SHARTLI BELGILAR

- R1, R2 — Welkin rekuperatori (koridor shiftida)
- so'rish kanali (xonalardan rekuperatorga)
- chiqarish kanali (fasadga)
- so'rish panjarasi
- split — tashqi blok (tomda, punktir)
- toza havo kanali (rekuperatordan xonalarga)
- tashqi havo kanali (fasaddan)
- toza havo diffuzori
- split — ichki blok (devorda), yozuv: BTU/soat

PDP Academy · Xadra filiali			
Chizma	**Ventilyatsiya va konditsionerlash**		
Manba: mavjud holat chizmasi (foto), 2-qavat · umumiy 617 m², foydali 557,74 m²			
Toshkent sh., Xadra — 2-qavat			
Masshtab **1:100**	Sana **09.10.2026**	Versiya **v1.2**	Varaq **3 / 4**
Bajardi			
Tekshirdi / tasdiqladi — direktor			



KONDITSIONERLAR (SPLIT, DEVORGA)

Kod	Xona	BTU	Ichki blok	Tashqi blok (TB)	Trassa	Elektr
KD-1	SR1	24k	orqa yon devorda, oynadan 1.8 m	tomda, yaqin ochiq joyda (xona ustida 3-qavat)	~13 m	3×2.5 mm², 20 A
KD-2	SR2	24k	orqa yon devorda, oynadan 1.8 m	tomda, xona ustida	~5 m	3×2.5 mm², 20 A
KD-3	SR3	24k	orqa yon devorda, oynadan 1.8 m	tomda, xona ustida	~5 m	3×2.5 mm², 20 A
KD-4	SR4	24k	o'ng devorda, doska ustida	tomda, xona ustida	~5 m	3×2.5 mm², 20 A
KD-5	SR5	24k	orqa yon devorda, oynadan 1.8 m	tomda, xona ustida	~5 m	3×2.5 mm², 20 A
KD-6	SR6	24k	orqa yon devorda, oynadan 1.8 m	tomda, xona ustida	~5 m	3×2.5 mm², 20 A
KD-7	SR7	24k	orqa yon devorda, oynadan 1.8 m	tomda, xona ustida	~5 m	3×2.5 mm², 20 A
KD-8	XZ1	12k	ichki devorda	tomda, yaqin ochiq joyda (xona ustida 3-qavat)	~7 m	3×1.5 mm², 16 A
KD-9	XZ2	12k	ichki devorda	tomda, yaqin ochiq joyda (xona ustida 3-qavat)	~7 m	3×1.5 mm², 16 A
KD-10	XZ3	12k	ichki devorda	tomda, xona ustida	~5 m	3×1.5 mm², 16 A
KD-11	XZ4	12k	ichki devorda	tomda, xona ustida	~5 m	3×1.5 mm², 16 A
—	KW	24k + 18k	mavjud, joyi o'zgarmaydi; koridorlarni ham sovutadi			
—	CEO	—	mavjud			

O'RNATISH

Sinflar (ko'cha tomoni to'liq oynali): SR1–SR3 (g'arb) — oyna ~1.0–3.1 m, SR5–SR7 (sharq) — poldan shiftgacha; oyna ustida blokka joy yo'q, fasad o'zgarmaydi. Ichki blok — doskaga qarama-qarshi yon devorda, oynadan ~1.8 m, pastki qirrasi 2.75 m: havo o'quvchilar ustidan doska tomonga, oyna zonasini ham sovutadi.
Tashqi bloklar — tomda, xona ustida, tayanch ramada (tomdan ≥ 0.4 m, tebranishga qarshi yostiqlar bilan); SR1, XZ1, XZ2 ustida 3-qavat — yaqin ochiq tomda. Trassa shift ichidan, tomdagi germetik o'tish (gusak) orqali; drenaj — shift ichida nishab bilan stoyakka yoki mini-nasos bilan tomga.
SR4: ichki blok o'ng devorda, doska ustida. **XZ1–XZ4:** ichki devorda.
Elektr: har bir split — shitdan alohida liniya. Jami ~20 kW (to'liq yuklamada). Detallar — 2-varaq (o'rnatish detallari).

MASSHTAB 1:100

0 1 2 3 4 5 m

SHARTLI BELGILAR

- KD — split ichki bloki (devorda, 2.75 m dan yuqori)
- TB — tashqi blok tomda (kesimdan yuqorida — punktir)
- freon trassasi (shift ichida, tomga chiqadi)
- oynali fasad: g'arb 1.0–3.1 m, sharq poldan shiftgacha
- sovuq havo oqimi yo'nalishi

PDP Academy · Xadra filiali	
Chizma	**Konditsionerlar joylashuvi**
Manba: mavjud holat chizmasi (foto), 2-qavat · umumiy 617 m², foydali 557,74 m²	
Toshkent sh., Xadra — 2-qavat	
Masshtab **1:100** · Sana **09.10.2026** · Versiya **v1.2** · Varaq **4 / 4**	
Bajardi	
Tekshirdi / tasdiqladi — direktor	