
SR4 ga koridorlar kirgan joylar (K1 va K2 uchlari), 1:75

v1.2 · 09.10.2026
o'lchamlar mm da, chizma fotosidan — joyida tekshiriladi

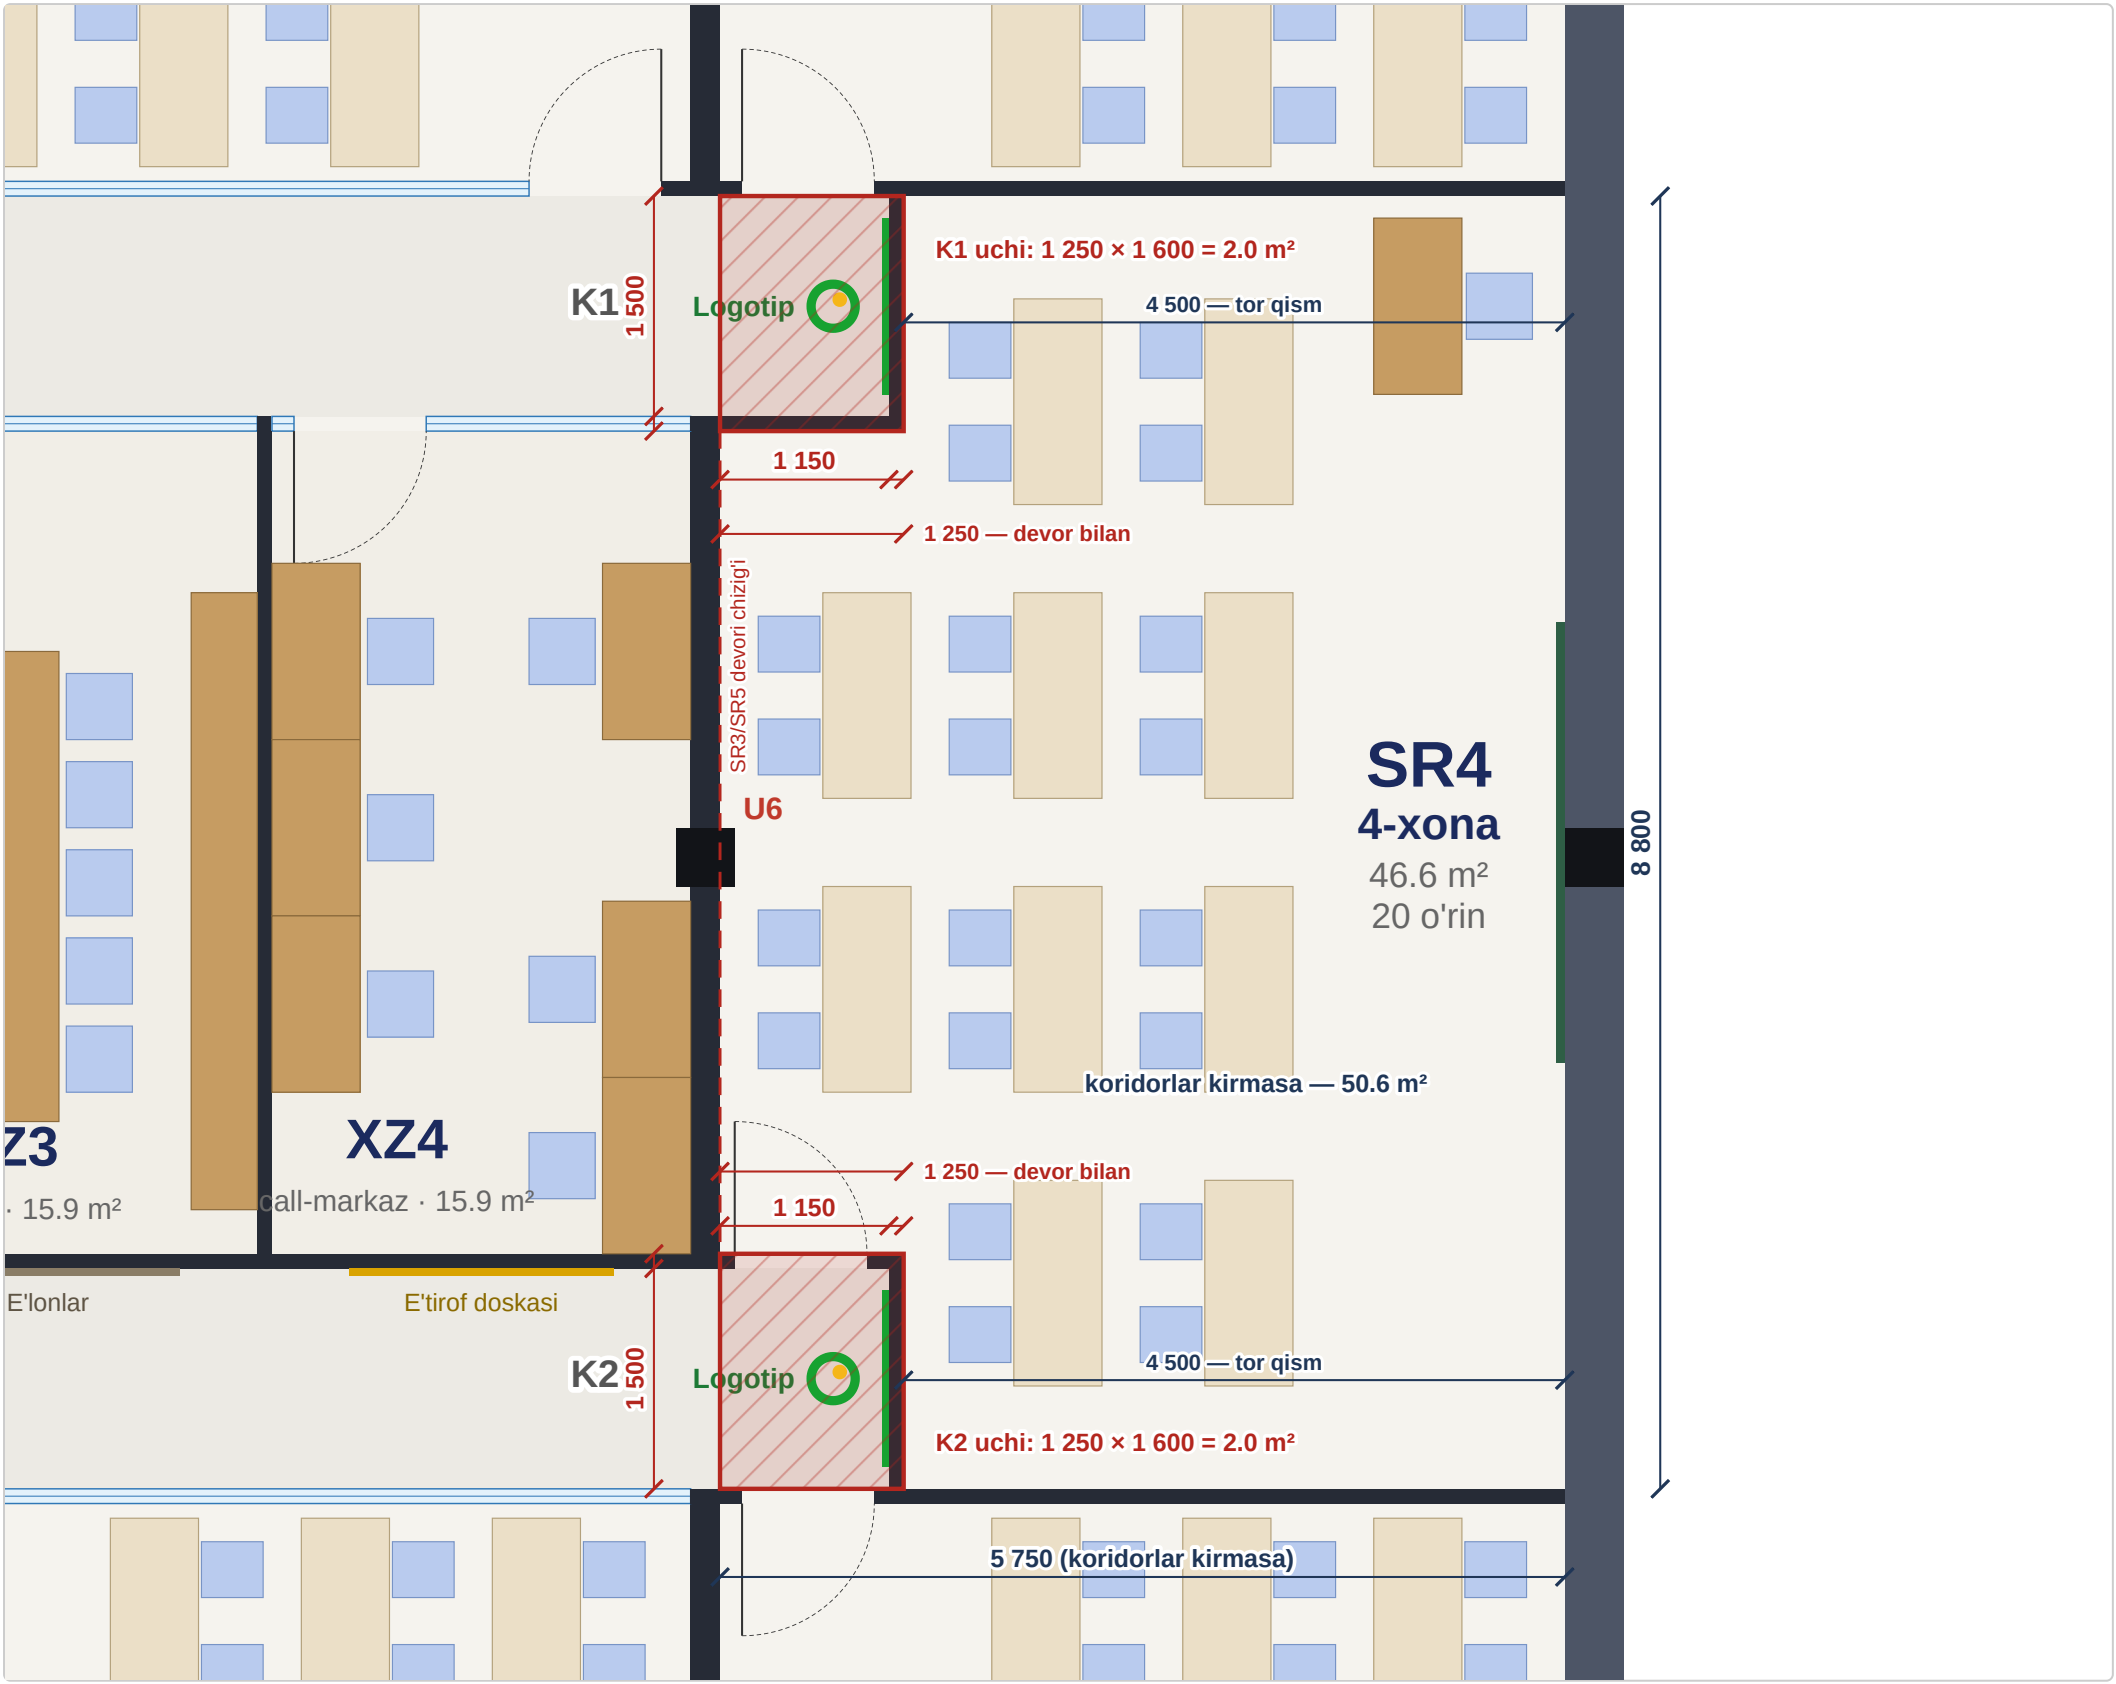

Joy	Koridor SR4 ichiga	Koridor eni	Koridor polining maydoni	Devorlari bilan
K1 uchi (SR4 ning yuqori chap burchagi)	1 150 mm	1 500 mm	1.73 m²	1 250 × 1 600 = 2.0 m²
K2 uchi (SR4 ning pastki chap burchagi)	1 150 mm	1 500 mm	1.73 m²	1 250 × 1 600 = 2.0 m²
Jami SR4 dan			**3.45 m²**	**4.0 m²**

Qizil shtrix — koridor uchi va uni o'rab turgan 100 mm GKL devorlar (koridor oxiridagi logotipli devor va SR4 bilan koridor orasidagi devor). Qizil punktir — SR3/SR5 devori chizig'i: koridorlar shu yerda tugasa, SR4 5 750 × 8 800 mm to'g'ri to'rtburchak (50.6 m²) bo'ladi; hozir 46.6 m², ikki chetidagi 1 600 mm lik qismlarda eni 4 500 mm.