
PDP Academy · Xadra filiali

2-qavat rejasi — xonalarga bo'linishi

Masshtab 1:100 (A3) · v1.2 · 17.10.2026

0 1 2 3 4 5 m

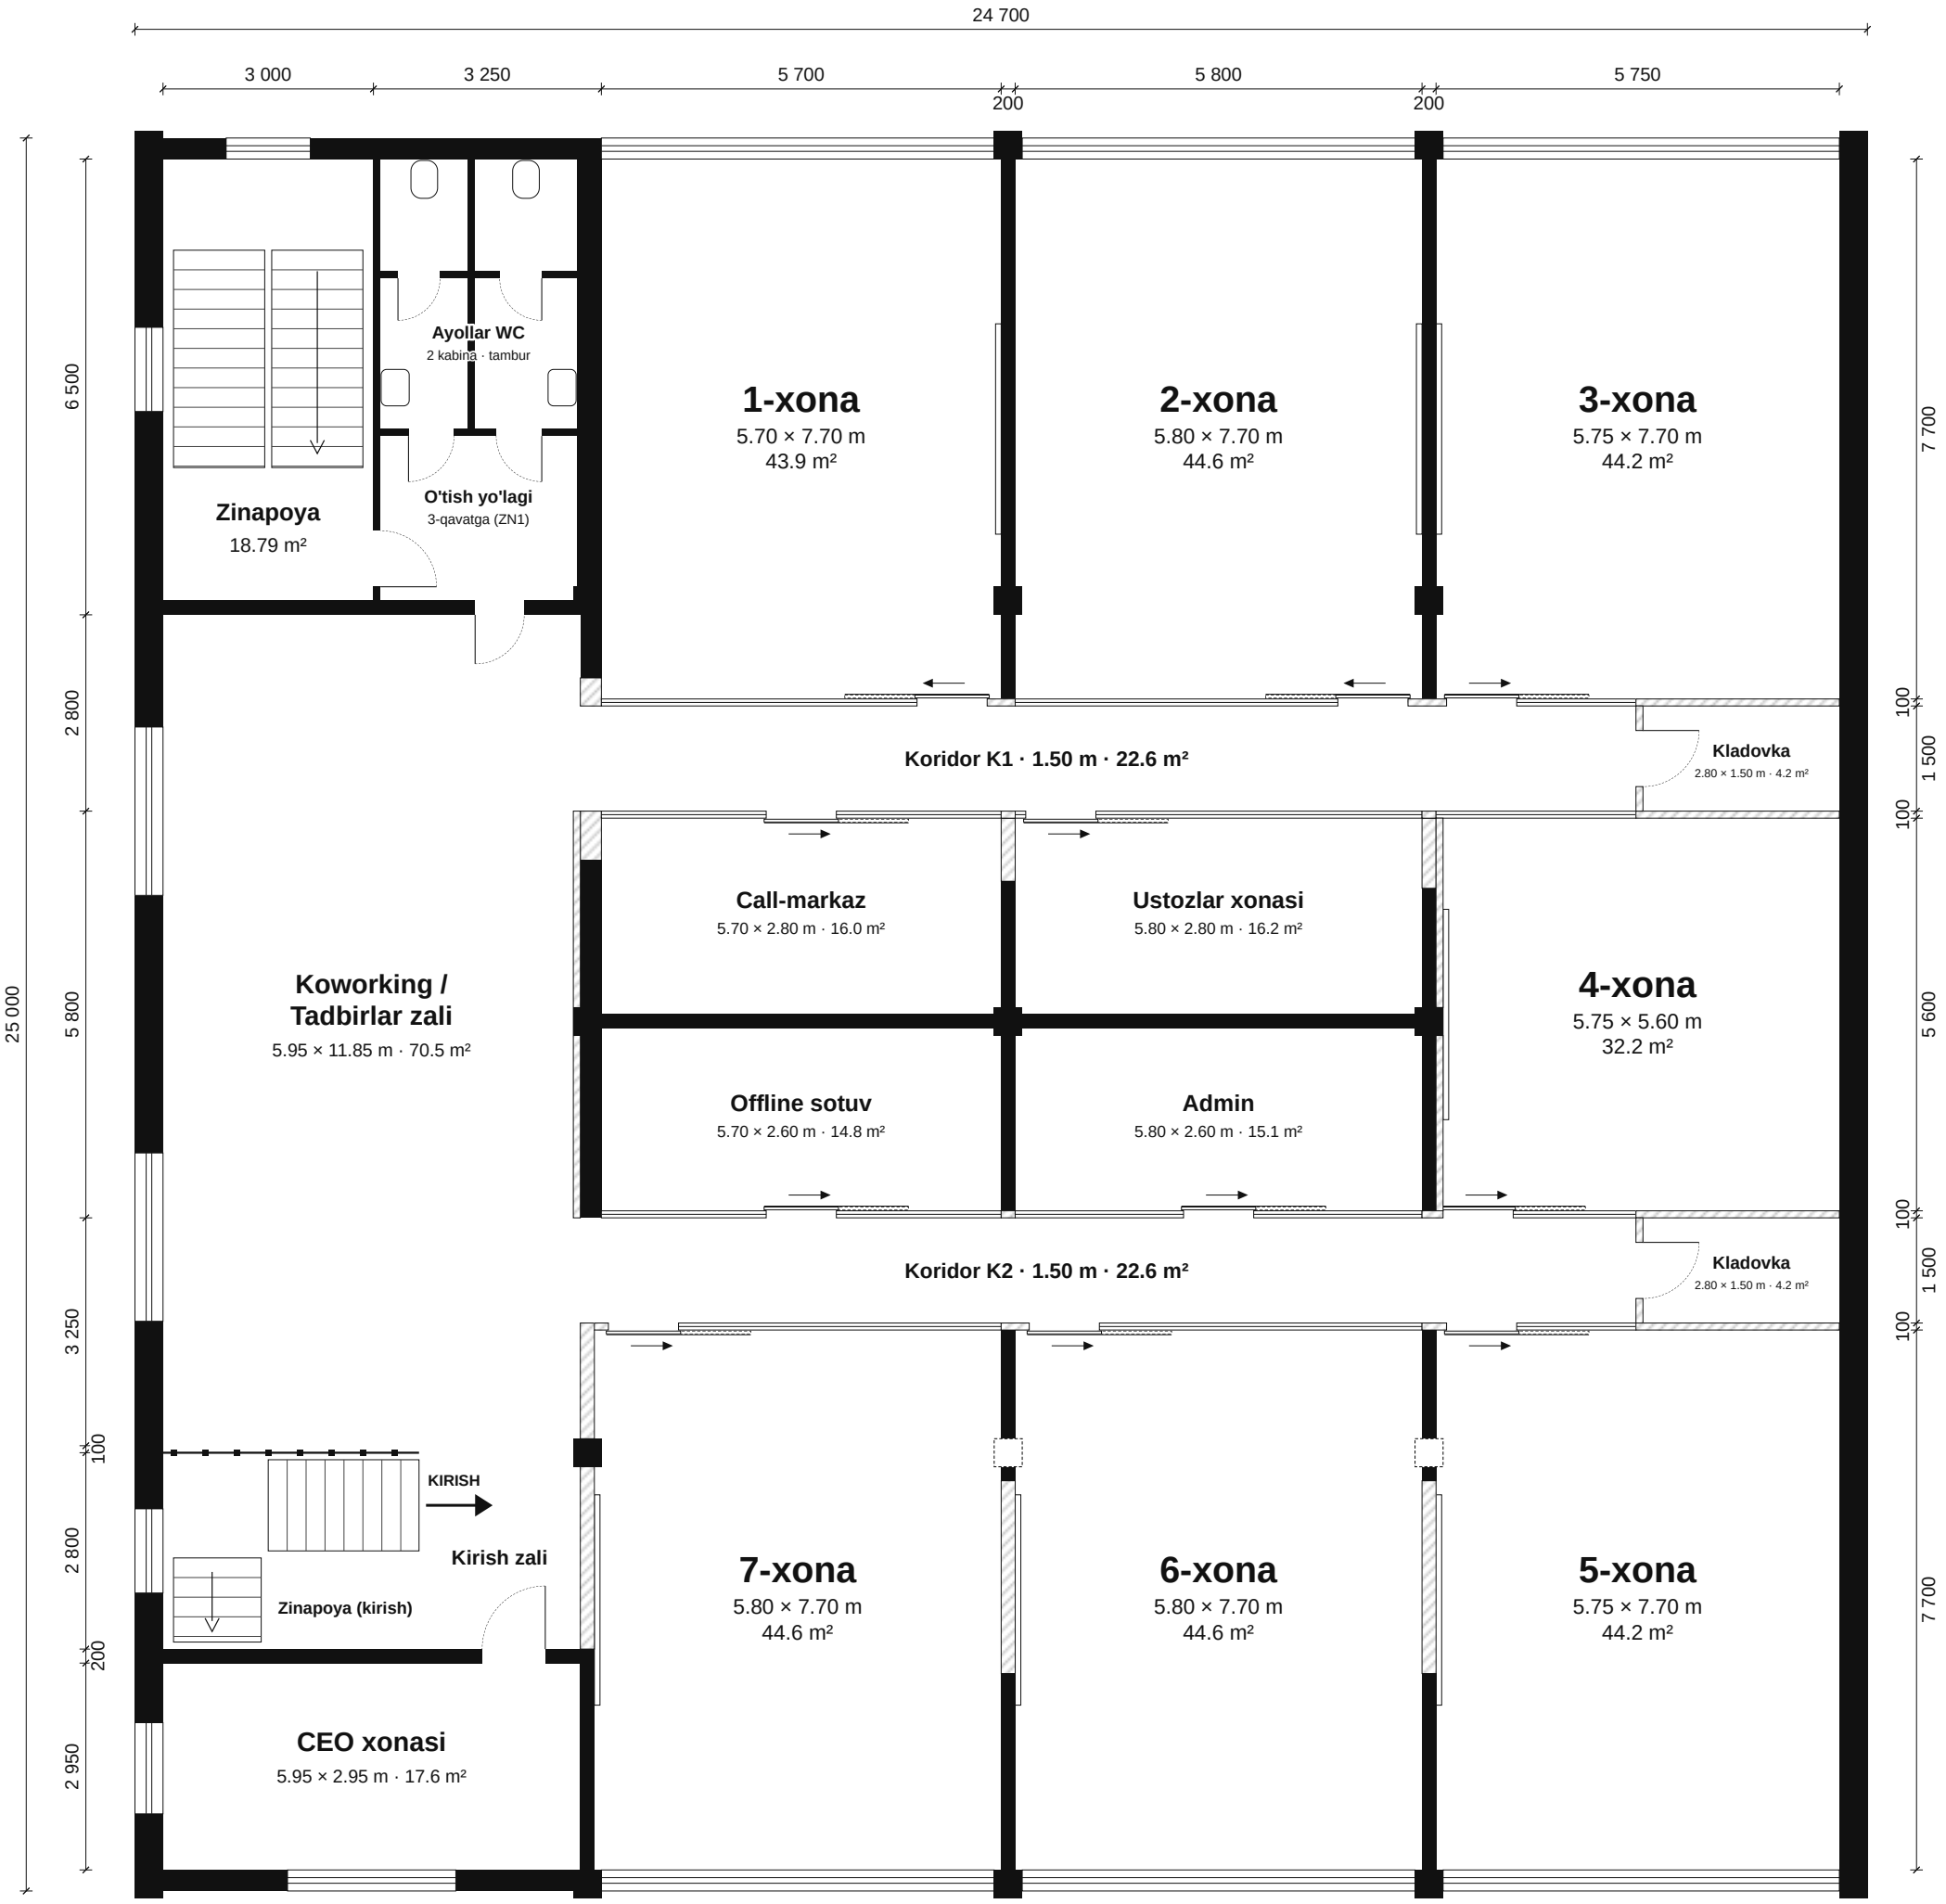

Xona	Ichki o'lcham	Maydon
1-xona	5.70 × 7.70 m	43.9 m²
2-xona	5.80 × 7.70 m	44.6 m²
3-xona	5.75 × 7.70 m	44.2 m²
4-xona	5.75 × 5.60 m	32.2 m²
5-xona	5.75 × 7.70 m	44.2 m²
6-xona	5.80 × 7.70 m	44.6 m²
7-xona	5.80 × 7.70 m	44.6 m²
Offline sotuv	5.70 × 2.60 m	14.8 m²
Admin	5.80 × 2.60 m	15.1 m²
Ustozlar xonasi	5.80 × 2.80 m	16.2 m²
Call-markaz	5.70 × 2.80 m	16.0 m²
O'quv xonalari, jami		**298.2 m²**

Xona	Ichki o'lcham	Maydon
Koworking / Tadbirlar zali	5.95 × 11.85 m	70.5 m²
CEO xonasi	5.95 × 2.95 m	17.6 m²
K1 koridori	15.05 × 1.50 m	22.6 m²
K2 koridori	15.05 × 1.50 m	22.6 m²
Kladovka (K1 oxiri)	2.80 × 1.50 m	4.2 m²
Kladovka (K2 oxiri)	2.80 × 1.50 m	4.2 m²
Kirish zali	2.30 × 2.90 m	6.6 m²
Zinapoyalar, WC, o'tish yo'lagi		45.8 m²
Umumiy foydali maydon (hujjat)		**557.74 m²**

Shartli belgilar va izoh

- mavjud va tashqi devor
- yangi devor — GKL 100
- shisha devor (2.5 m gacha)
- suriladigan eshik 1 m (barg xona ichida)
- ustun

- Ichki o'lcham — devor yuzidan devor yuzigacha, m; maydon ustunlarsiz. Mavjud chizmadan, joyida o'lchanadi.
- Balandlik 3.5 m. Doska — yon devorda (oq to'rtburchak); 4-xonada eshik tomonida, U6 bilan tekis GKL qoplama.
- Kladovka ustida kanalli konditsioner (KK1, KK2).