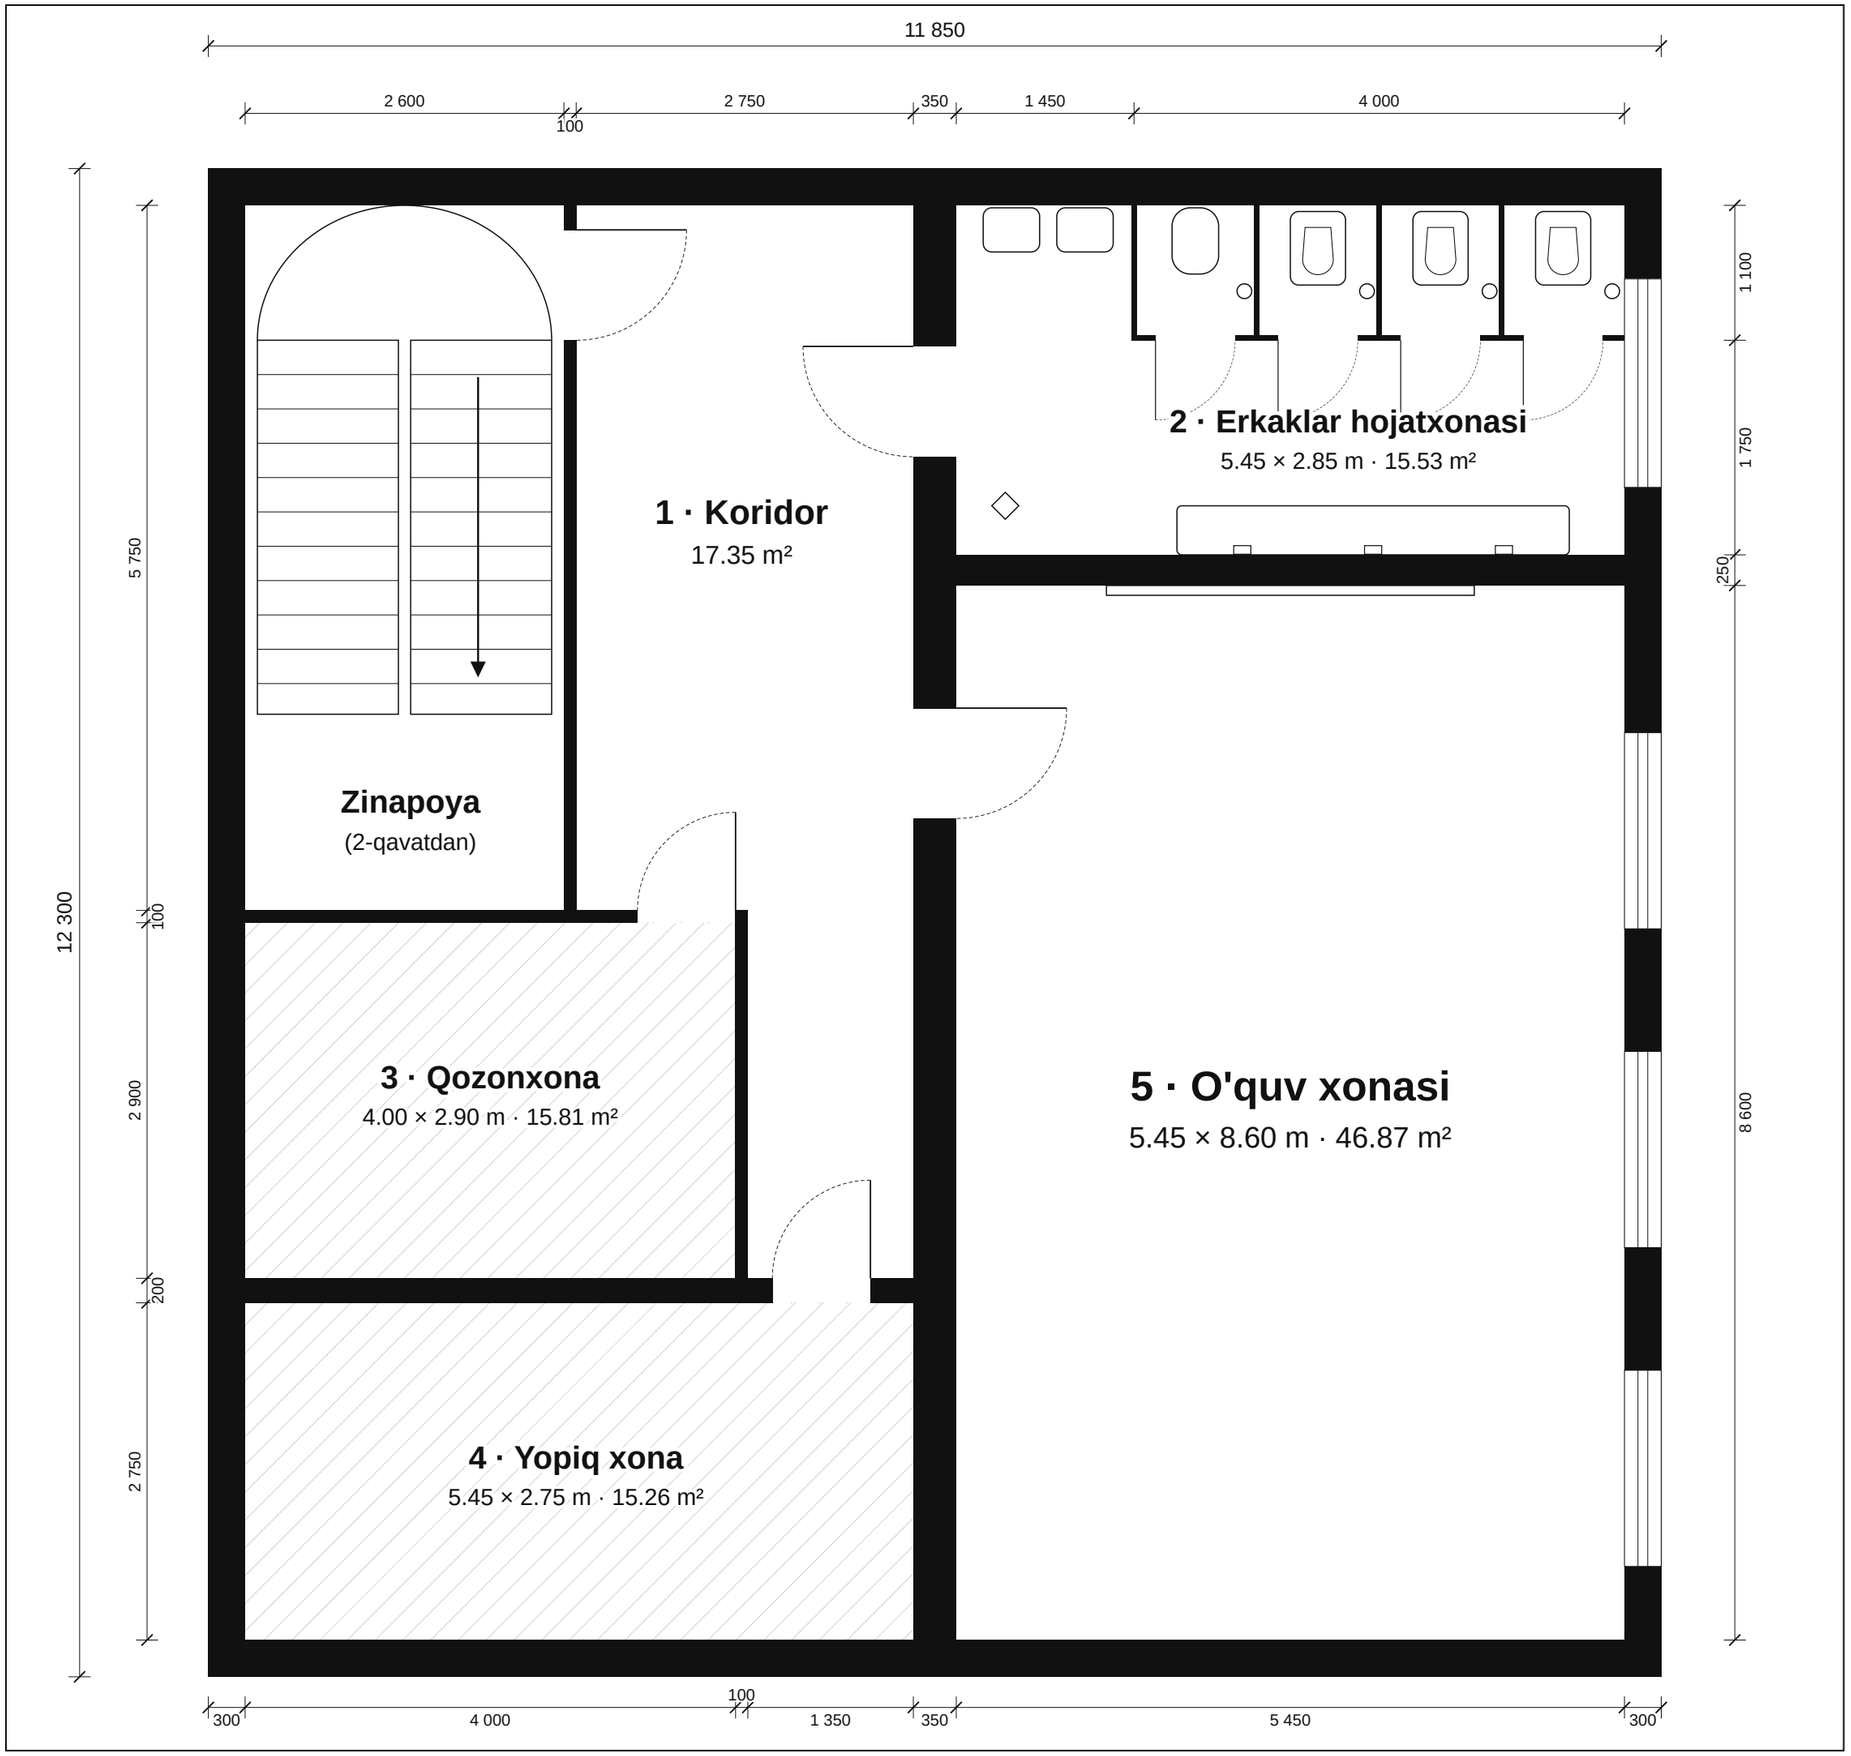


PDP Academy · Xadra filiali

3-qavat rejasi — rangsiz, mebelsiz

5-xona — o'quv xonasi, 2-xona — erkaklar hojatxonasi; 1, 3, 4 o'zgarmaydi

Masshtab 1:50 (A3) · v1.2 · 17.10.2026

0 0.5 1 1.5 2 2.5 m

Xona	Ichki o'lcham	Maydon
1 · Koridor	L shakli	17.35 m²
2 · Erkaklar hojatxonasi	5.45 × 2.85 m	15.53 m²
3 · Qozonxona	4.00 × 2.90 m	15.81 m²
4 · Yopiq xona (bino egasiniki)	5.45 × 2.75 m	15.26 m²
5 · O'quv xonasi	5.45 × 8.60 m	46.87 m²
Foydali maydon (hujjat)		**110.82 m²**

Izoh

- Devorlar — qora; 3 va 4-xona o'zgarmaydi (xira shtrix).
- 2-xona: 4 ta kabina (1 × 1.1 m, eshigi 650), 1-sida unitaz, qolganlarida chashagen, har birida mustahab; kirganda chapda 2 ta rakovina; janubiy devor bo'ylab taxorat joyi (3 jo'mrak), eshik yonida trap.
- 5-xona: doska shimoliy devorda (oq to'rtburchak) — eshikdan kirganda chapda; derazalar o'ng tomonda.
- Derazalar joyi taxminiy; o'lchamlar chizma fotosidan — joyida o'lchanadi.