


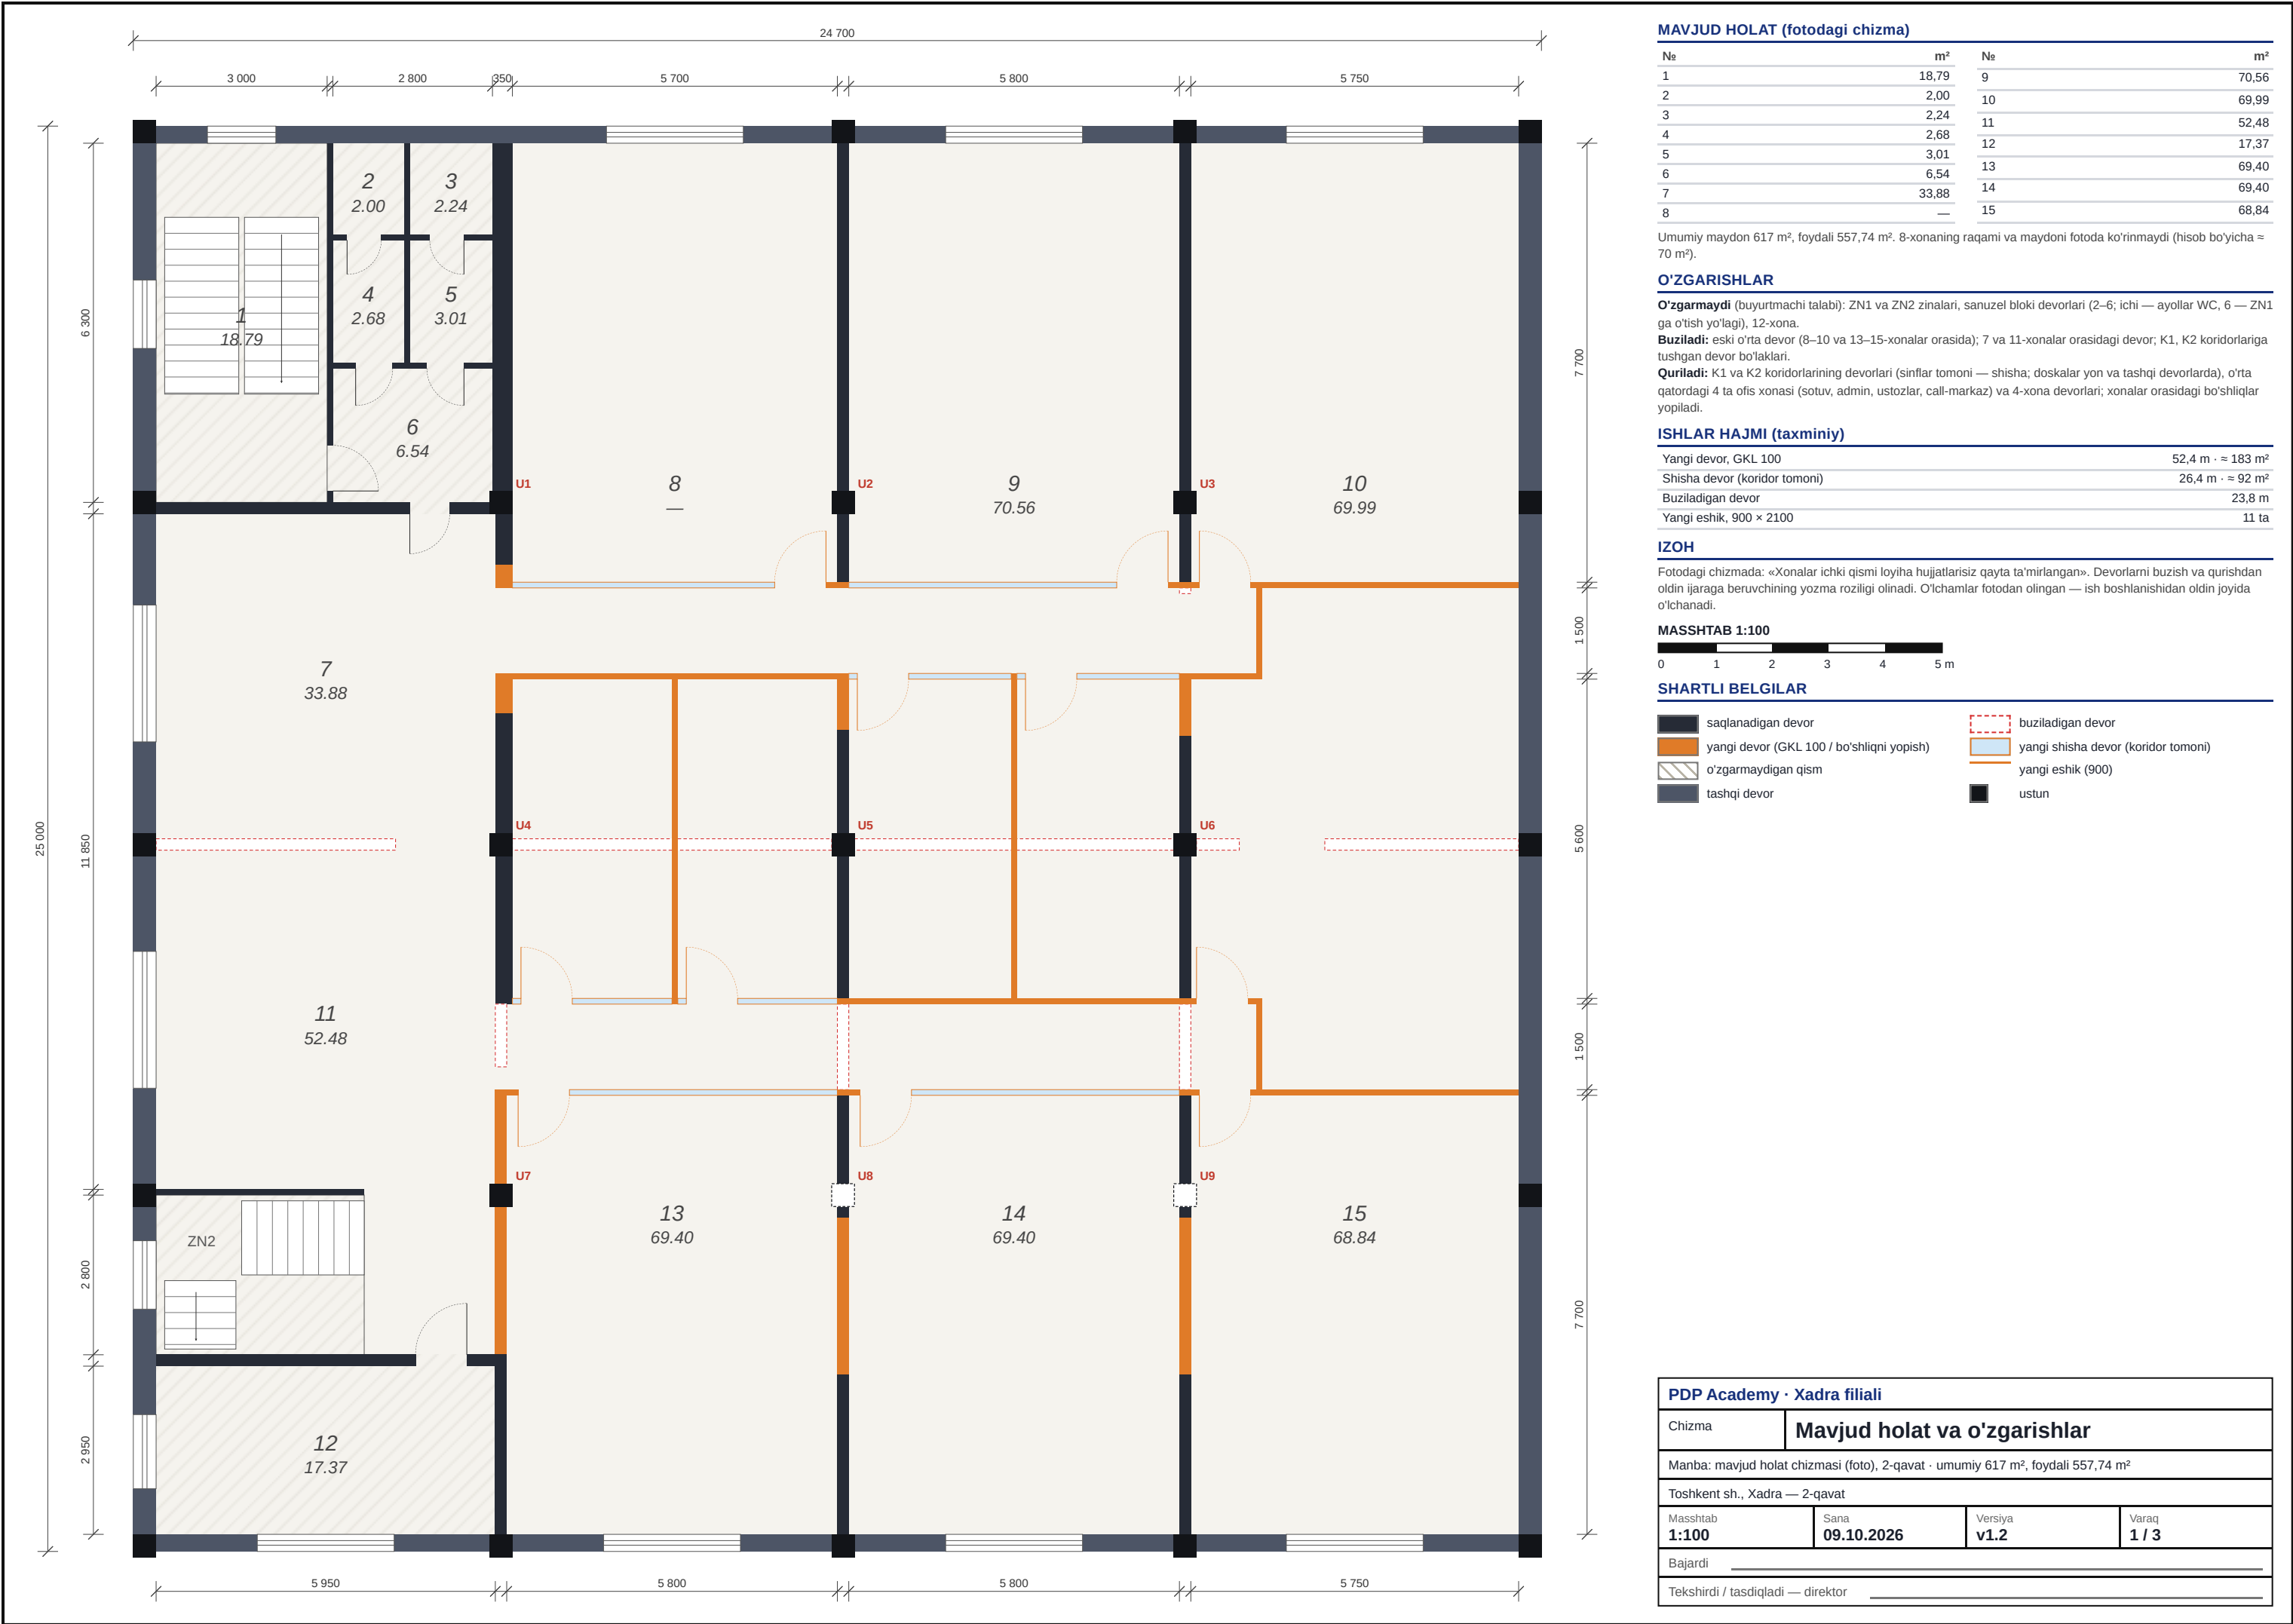

MAVJUD HOLAT (fotodagi chizma)

№	m²	№	m²
1	18,79	9	70,56
2	2,00	10	69,99
3	2,24	11	52,48
4	2,68	12	17,37
5	3,01	13	69,40
6	6,54	14	69,40
7	33,88	15	68,84
8	—		

Umumiy maydon 617 m², foydali 557,74 m². 8-xonaning raqami va maydoni fotoda koʻrinmaydi (hisob boʻyicha ≈ 70 m²).

OʻZGARISHLAR

Oʻzgarmaydi (buyurtmachi talabi): ZN1 va ZN2 zinalari, sanuzel bloki devorlari (2–6; ichi — ayollar WC, 6 — ZN1 ga oʻtish yoʻlagi), 12-xona.

Buziladi: eski oʻrta devor (8–10 va 13–15-xonalar orasida); 7 va 11-xonalar orasidagi devor; K1, K2 koridorlariga tushgan devor boʻlaklari.

Quriladi: K1 va K2 koridorlarining devorlari (sinflar tomoni — shisha; doskalar yon va tashqi devorlarda), oʻrta qatordagi 4 ta ofis xonasi (sotuv, admin, ustozlar, call-markaz) va 4-xona devorlari; xonalar orasidagi boʻshliqlar yopiladi.


ISHLAR HAJMI (taxminiy)

Yangi devor, GKL 100	52,4 m · ≈ 183 m²
Shisha devor (koridor tomoni)	26,4 m · ≈ 92 m²
Buziladigan devor	23,8 m
Yangi eshik, 900 × 2100	11 ta

IZOH

Fotodagi chizmada: «Xonalar ichki qismi loyiha hujjatlarisiz qayta taʼmirlangan». Devorlarni buzish va qurishdan oldin ijaraga beruvchining yozma roziligi olinadi. Oʻlchamlar fotodan olingan — ish boshlanishidan oldin joyida oʻlchanadi.

MASSHTAB 1:100

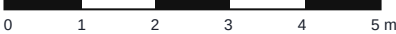

SHARTLI BELGILAR

saqlanadigan devor	buziladigan devor
yangi devor (GKL 100 / boʻshliqni yopish)	yangi shisha devor (koridor tomoni)
oʻzgarmaydigan qism	yangi eshik (900)
tashqi devor	ustun

PDP Academy · Xadra filiali			
Chizma	Mavjud holat va o'zgarishlar		
Manba: mavjud holat chizmasi (foto), 2-qavat · umumiy 617 m², foydali 557,74 m²			
Toshkent sh., Xadra — 2-qavat			
Mashtab 1:100	Sana 09.10.2026	Versiya v1.2	Varaq 1 / 3
Bajardi _____			
Tekshirdi / tasdiqladi — direktor _____			



MAYDON	
Ichki gabarit	23 900 × 24 400
Umumiy maydon (hujjat)	617 m²
Foydali maydon (hujjat)	557,74 m²
O'quv xonalari, 7 ta · 164 o'rin	312,6 m²
Offline sotuv (XZ1) va admin (XZ2)	31,3 m²
Ustozlar (XZ3), call-markaz (XZ4)	31,8 m²
Koworking / tadbirlar zali (KW)	70,5 m²
CEO xonasi (12-xona, o'zgarmaydi)	17,6 m²
Koridorlar K1, K2 va kirish zali ZL	46,7 m²
Zinalar, ayollar WC va o'tish yo'lagi (devorlari o'zgarmaydi)	45,8 m²
Balandlik (poldan shiftgacha)	3500 mm (buyurtmachi)

XONALAR					
Xona	O'lcham, m	m²	O'rin	m²/kishi	Partalar
SR1 · 1-xona	7.70 × 5.70	43,9	24	1,8	4+4+4
SR2 · 2-xona	7.70 × 5.80	44,6	24	1,9	4+4+4
SR3 · 3-xona	7.70 × 5.75	44,2	24	1,8	4+4+4
SR4 · 4-xona	8.80 × 5.75 (L)	46,6	20	2,3	4+4+2
SR5 · 5-xona	7.70 × 5.75	44,2	24	1,8	4+4+4
SR6 · 6-xona	7.70 × 5.80	44,6	24	1,9	4+4+4
SR7 · 7-xona	7.70 × 5.80	44,6	24	1,9	4+4+4
XZ1 · sotuv	2.80 × 5.60	15,7	2	—	2 stol + 4 mijoz stuli, shisha devor
XZ2 · admin	2.80 × 5.60	15,6	2	—	2 stol + 2 mehmon stuli, shisha devor
XZ3 · ustozlar	2.85 × 5.60	15,9	9	—	umumiy stol, lokerlar
XZ4 · call-markaz	2.85 × 5.60	15,9	6	—	devor bo'ylab 6 ish o'rni
CEO (12-xona)	5.95 × 2.95	17,6	1	—	ish stoli + 4 kishilik stol, derazali
KW	5.95 × 11.85	70,5	~35	—	koworking; sahna — XZ1 devori, tadbirda 68 o'rin
Jami		312,6	164		6 × 24 + 1 × 20

USTUNLAR — MAVJUD				
Kod	O'q	X	Y	O'lcham
U1	2-B	6 050	6 300	400 × 400
U2	3-B	12 050	6 300	400 × 400
U3	4-B	18 050	6 300	400 × 400
U4	2-C	6 050	12 300	400 × 400
U5	3-C	12 050	12 300	400 × 400
U6	4-C	18 050	12 300	400 × 400
U7	2-D	6 050	18 450	400 × 400
U8	3-D	12 050	18 450	400 × 400 *
U9	4-D	18 050	18 450	400 × 400 *

Koordinata — ichki yuzaning yuqori-chap burchagidan, ustun markazi bo'yicha; o'qlar taxminiy. * U8, U9 fotoda ko'rinmaydi — to'r bo'yicha qo'yilgan (devor ichida), joyida tekshirilsin.

PARTA TO'RI (Xadra filiali)

parta 1400 × 600 (2 kishilik) · stul 380 × 420
qatorda 4 parta (8 o'rin) · yo'lak 600 · deraza tomonida devorgacha 200
3 qator · qadam 1 300 (parta 600 + stul va o'tish 700)
doskadan 1-partagacha 1 850 · oxirgi parta 5 050 · sig'im 24
ISTISNO: SR3 — doska va ustoz joyi kirish tomonida (buyurtmachi), deraza o'quvchilarning o'ng tomonida; SR4 — 4 + 4 + 2 parta, 20 o'rin (doska o'ng tashqi devorda)
Beruniy standarti: parta 690 × 500 (1 kishilik), 2 + 2 + 2 × 4 qator, qadam 1 300, doskadan 2 440, oxirgi 6 840
ustundan: oldi/orqa 500 · yon 0. Doska 3000 yon (kar) devorda, deraza o'quvchilarning chap tomonida (SR3 dan tashqari); eshiklar 900.
K1, K2 koridorlari 1500. Yangi devorlar — GKL 100; sinflarning koridor tomoni — akustik shisha.
KW: o'ng tomonda ~1,6 m o'tish yo'lagi bo'sh (6-xona — ZN1 ga o'tish, K1, K2, kirish zali); sahna — XZ1 devorida, podiumsiz.
Ayollar WC: 2 kabina eng ichkarida (2, 3 — unitaz), oldida tambur (4, 5 — rakovina); ikki eshik orqali kiriladi.
Ofis xonalari (XZ1–XZ4): eshik tomoni shisha devor; barcha yangi eshiklar shisha.
XZ3 — ustozlar xonasi, XZ4 — call-markaz va online sotuv; 12-xona — CEO (mavjud holicha).
Zinalar mavjud holicha; 1-qavatda zina oldida resepsn va turniket.



SHARTLI BELGILAR	
kesilgan ichki devor	kesilgan tashqi devor
mavjud ustun 400 × 400	taxminiy ustun (fotoda yo'q)
deraza (joyi taxminiy)	parta 1400 × 600 (2 kishilik)
stul 380 × 420	doska (kar devorda)
o'qituvchi / xodim stoli	shisha devor (koridor tomoni)
yorituvchi logotip (koridor oxiri, GKL devor)	e'lonlar doskasi
e'tirof doskasi (faxriylar, oy o'quvchisi)	koworking sahnasi (XZ1 devori): logotip, ekran, reyka

PDP Academy · Xadra filiali			
Chizma	Jihozlash rejasi		
Manba: mavjud holat chizmasi (foto), 2-qavat · umumiy 617 m², foydali 557,74 m²			
Toshkent sh., Xadra — 2-qavat			
Mashtab	Sana	Versiya	Varaq
1:100	09.10.2026	v1.2	2 / 3



Havo almashinuvi — XONALAR BO'YICHA						
Xona	Odam	Havo, m³/soat	Hajm, m³	Marta / soat	Sovutish, kVt	Qurilma
SR1	25	750	153	4,9	8,0	PV-1
SR2	25	750	156	4,8	8,0	PV-2
SR3	25	750	155	4,8	8,0	PV-3
SR4	21	630	163	3,9	6,0	PV-4
SR5	25	750	155	4,8	8,0	PV-5
SR6	25	750	156	4,8	8,0	PV-6
SR7	25	750	156	4,8	8,0	PV-7
XZ1–XZ4	24	720	221	3,3	8,5	PV-9
KW (tadbir)	70	2 100	247	8,5	17,0	PV-8
Jami		7 950			79,5	

HISOB ASOSI

30 m³/soat har bir kishiga (o'quvchilar + o'qituvchi). Bir kishi soatiga ~18 l CO₂ chiqaradi: 18 l ÷ (1000 – 420) ppm ≈ 31 m³/soat — xonada CO₂ 1000 ppm dan oshmaydi.

Hajm — balandlik 3500 mm (buyurtmachi) bo'yicha. Sovutish — odamlar, noutbuklar, proyektor, yoritish, derazadan quyosh va toza havo (rekuperator FIK 60%) yig'indisi, Toshkent yozi (+40 °C) uchun dastlabki baho.

YECHIM

1–3 va 5–7-xonalar: deraza yon devorda, qarama-qarshi devorgacha 7,7 m: tabiiy shamollatish (~2,5 × H ≈ 7,5 m) deyarli butun xonaga yetadi, lekin qish va yozda derazalar yopiq — har sinfga alohida **PV qurilma** (rekuperatorli, ~750 m³/soat, shovqin ≤ 35 dB(A)), deraza devori yonida shift ichida.

4-xona va xizmat xonalarida deraza yo'q — mexanik ventilyatsiya va konditsioner majburiy. O'ng devor qo'shni bino bilan umumiy, orqasida tor oraliq bor: PV-4 panjaralari shu oraliqqa chiqariladi — kirish va chiqish bir-biridan uzoq (7 m), oraliq eni joyida o'lchanadi; havo turg'un bo'lsa, kanal K2 shifti orqali fasadga. PV-9 koworking chap devoridan olib, K1 shifti orqali XZ1–XZ4 ga beradi.

KW: derazalar chap devorda; tadbirida ~70 kishi — PV-8 ~2 100 m³/soat.

Toza havo doska oldida beriladi, orqa devor yonida so'riladi. CO₂ datchigi bilan boshqariladi; bo'sh xona o'chadi. Har sinfga 2 ta KD (kasseta yoki kanali).

V-1: sanuzel chiqarish ventilyatsiyasi 4 × 50 = 200 m³/soat — mavjud shaxtani tekshirish. Tutun chiqarish talabini yong'in xavfsizligi mutaxassisi belgilaydi.



- SHARTLI BELGILAR**
- PV — rekuperatorli kiritish-chiqarish qurilmasi (shift ichida)
 - toza havo diffuzori
 - fasad panjarasi: toza havo kirishi
 - KD — konditsioner ichki bloki
 - CO₂ datchigi
 - toza havo kanali
 - so'rish panjarasi
 - fasad panjarasi: iflos havo chiqishi
 - xonadagi havo oqimi

PDP Academy · Xadra filiali			
Chizma	Havo almashinuvi sxemasi		
Manba: mavjud holat chizmasi (foto), 2-qavat · umumiy 617 m², foydali 557,74 m²			
Toshkent sh., Xadra — 2-qavat			
Masshtab 1:100	Sana 09.10.2026	Versiya v1.2	Varaq 3 / 3
Bajardi _____			
Tekshirdi / tasdiqladi — direktor _____			