


1-qavat rejasi — kirish zali: resepshn, turniketlar va logotiplar

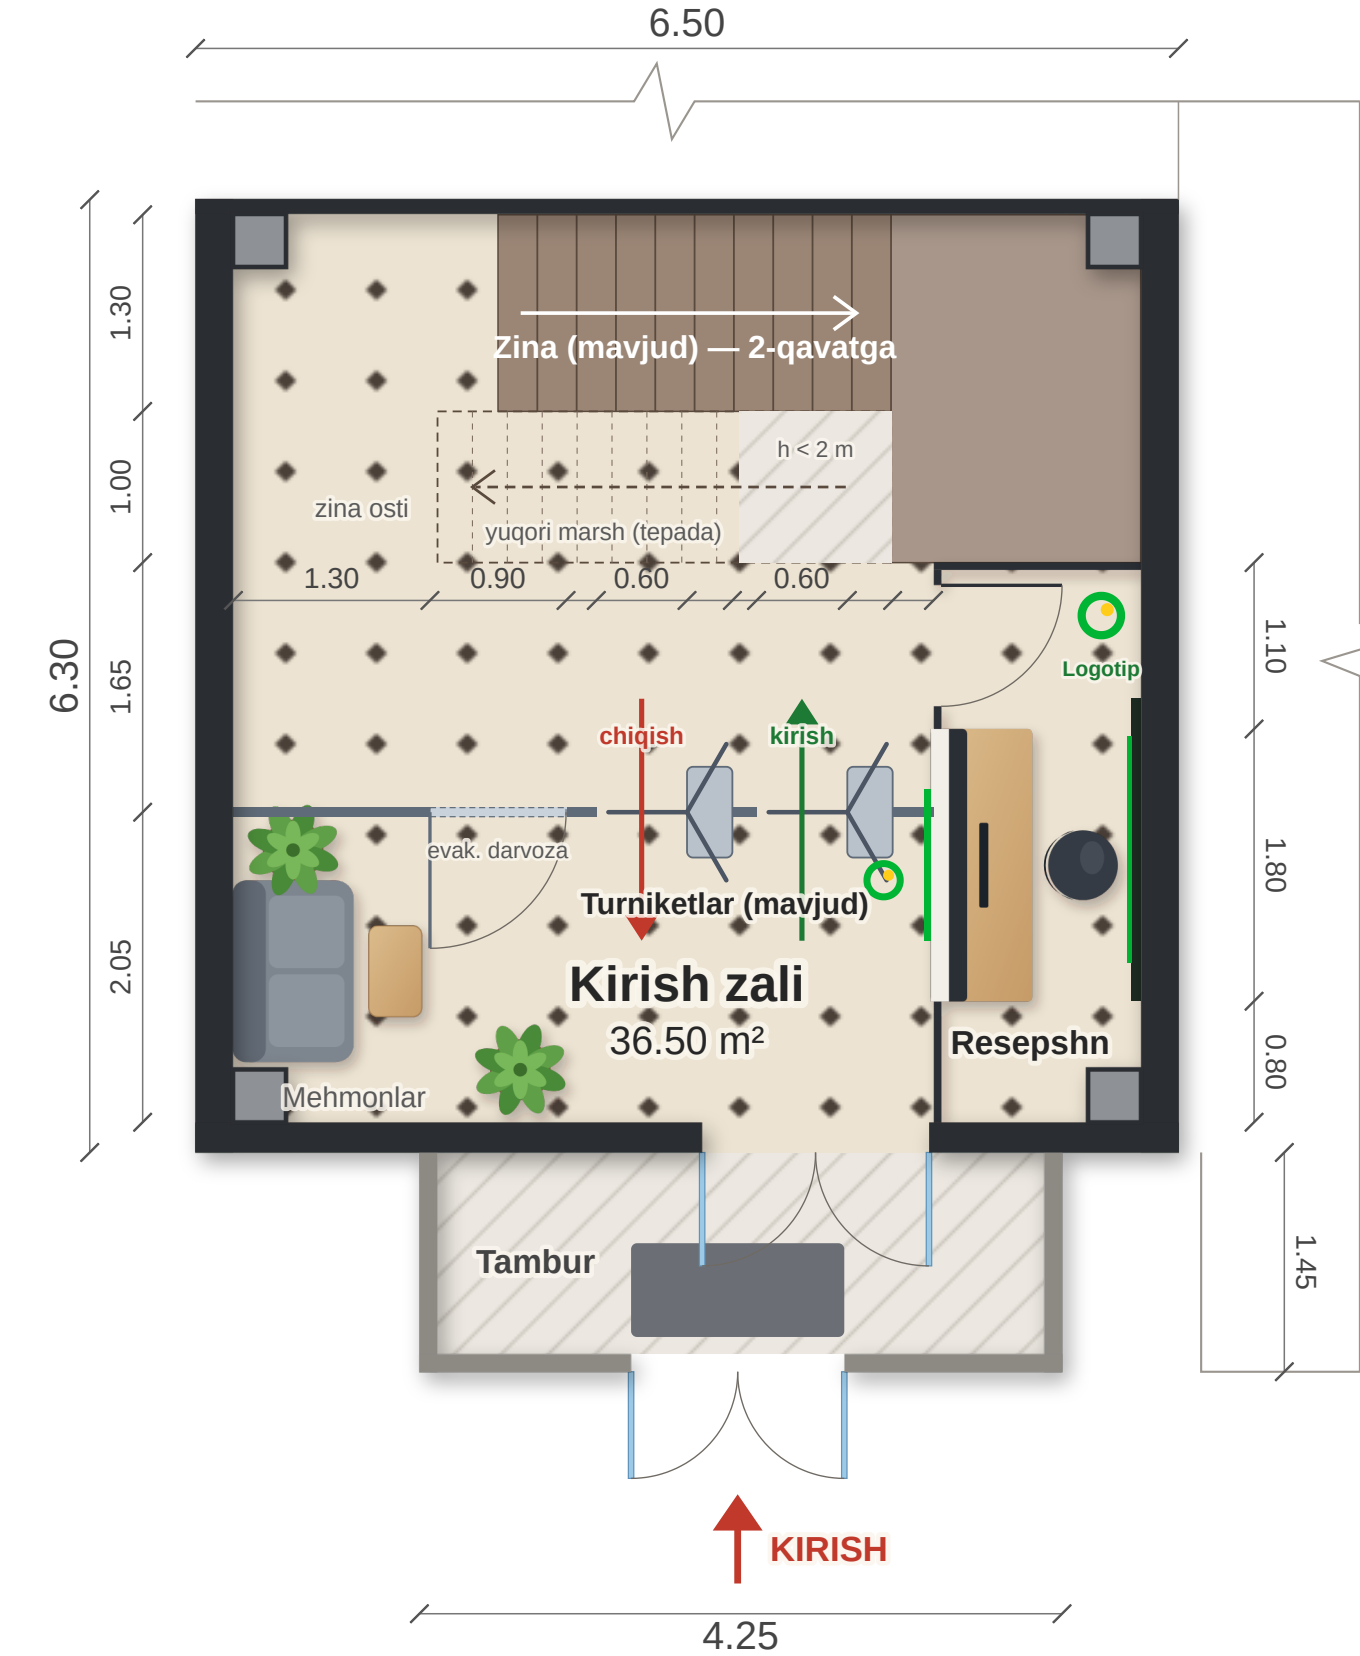

Yechim (buyurtmachi sxemasi bo'yicha)

- Zina mavjud holicha:** pastki marsh shimoliy devor bo'ylab sharqqa, sharqiy maydoncha (~1.5 m), undan yuqori marsh g'arbga — 2-qavatga. Shuning uchun zalning shimoliy qismi (2.30 m) zinaga band.
- Turniket chizig'i** eshikdan 2.05 m ichkarida, zal bo'ylab: o'ngda **kirish** (resepshn yonida), chaprog'ida **chiqish** — turniketlar buyurtmachida mavjud; o'tish yo'llari 60 va 60 sm. Chapda **evakuatsiya darvozasi** 90 sm (antipanika, chiqishga ochiladi), qolgan qismi to'siq.
- Resepshn** o'ng devor bo'ylab L shaklida: stoyka 1.80 m, zalga qaragan (turniketlar va eshik ko'rinadi), mijoz tomonida 1.10 m lik peshtaxta; qolgan qismi past to'siq panellari, shimolda — zina maydonchasi tagidagi yopuvchi panel. Xodim resepshnga turniketdan o'tgan zonadan, 80 sm eshikcha orqali kiradi.
- Logotiplar** (design.pdp.uz, PDP Academy): xodim orqasidagi o'ng devorda to'q panelda ichidan yoritilgan katta logotip (~1.50 m) — eshikdan kirganda o'ng tomonda, zaldan ko'rinadi; stoykaning zal tomonidagi panelida ikkinchi logotip (~1.00 m, yoritilgan).
- Mehmonlar joyi:** chap devor bo'ylab divan va jurnal stolchasi — kirish zonasida (turniketgacha).
- Pol (oktagon plitka), devorlar va zina — mavjud holicha (videodagi kabi).

Ko'rsatkich	Qiymat
Zal (tashqi / ichki)	6.50 × 6.30 m / 6.00 × 6.00 m · 36.50 m²
Turniket yo'llari / evakuatsiya darvozasi	600 / 600 / 900 mm
Resepshn stoykasi / to'siq panellari	1.80 m · h 1.10 / 0.75 m
Avtomatik tekshiruv (to'qnashuv, eshik, zina)	xato yo'q



3D: eshikdan kirganda



3D: resepshn va logotip

Tasdiqlash uchun

- Turniketlar 2 ta (kirish va chiqish) deb olindi — to'g'rimi? To'siq va evakuatsiya darvozasi komplektda bormi?
- Zina o'lchamlari videodan taxminiy — joyida o'lchanadi (ayniqsa yuqori marsh ostidagi balandlik).

O'lchamlar buyurtmachi yuborgan 1-qavat chizmasi, sxemasi va videosidan; ustunlar, devor qalinliklari va zina taxminiy — joyida o'lchanadi.