


1-qavat rejasi — kirish zali: resepshn, turniket va logotiplar

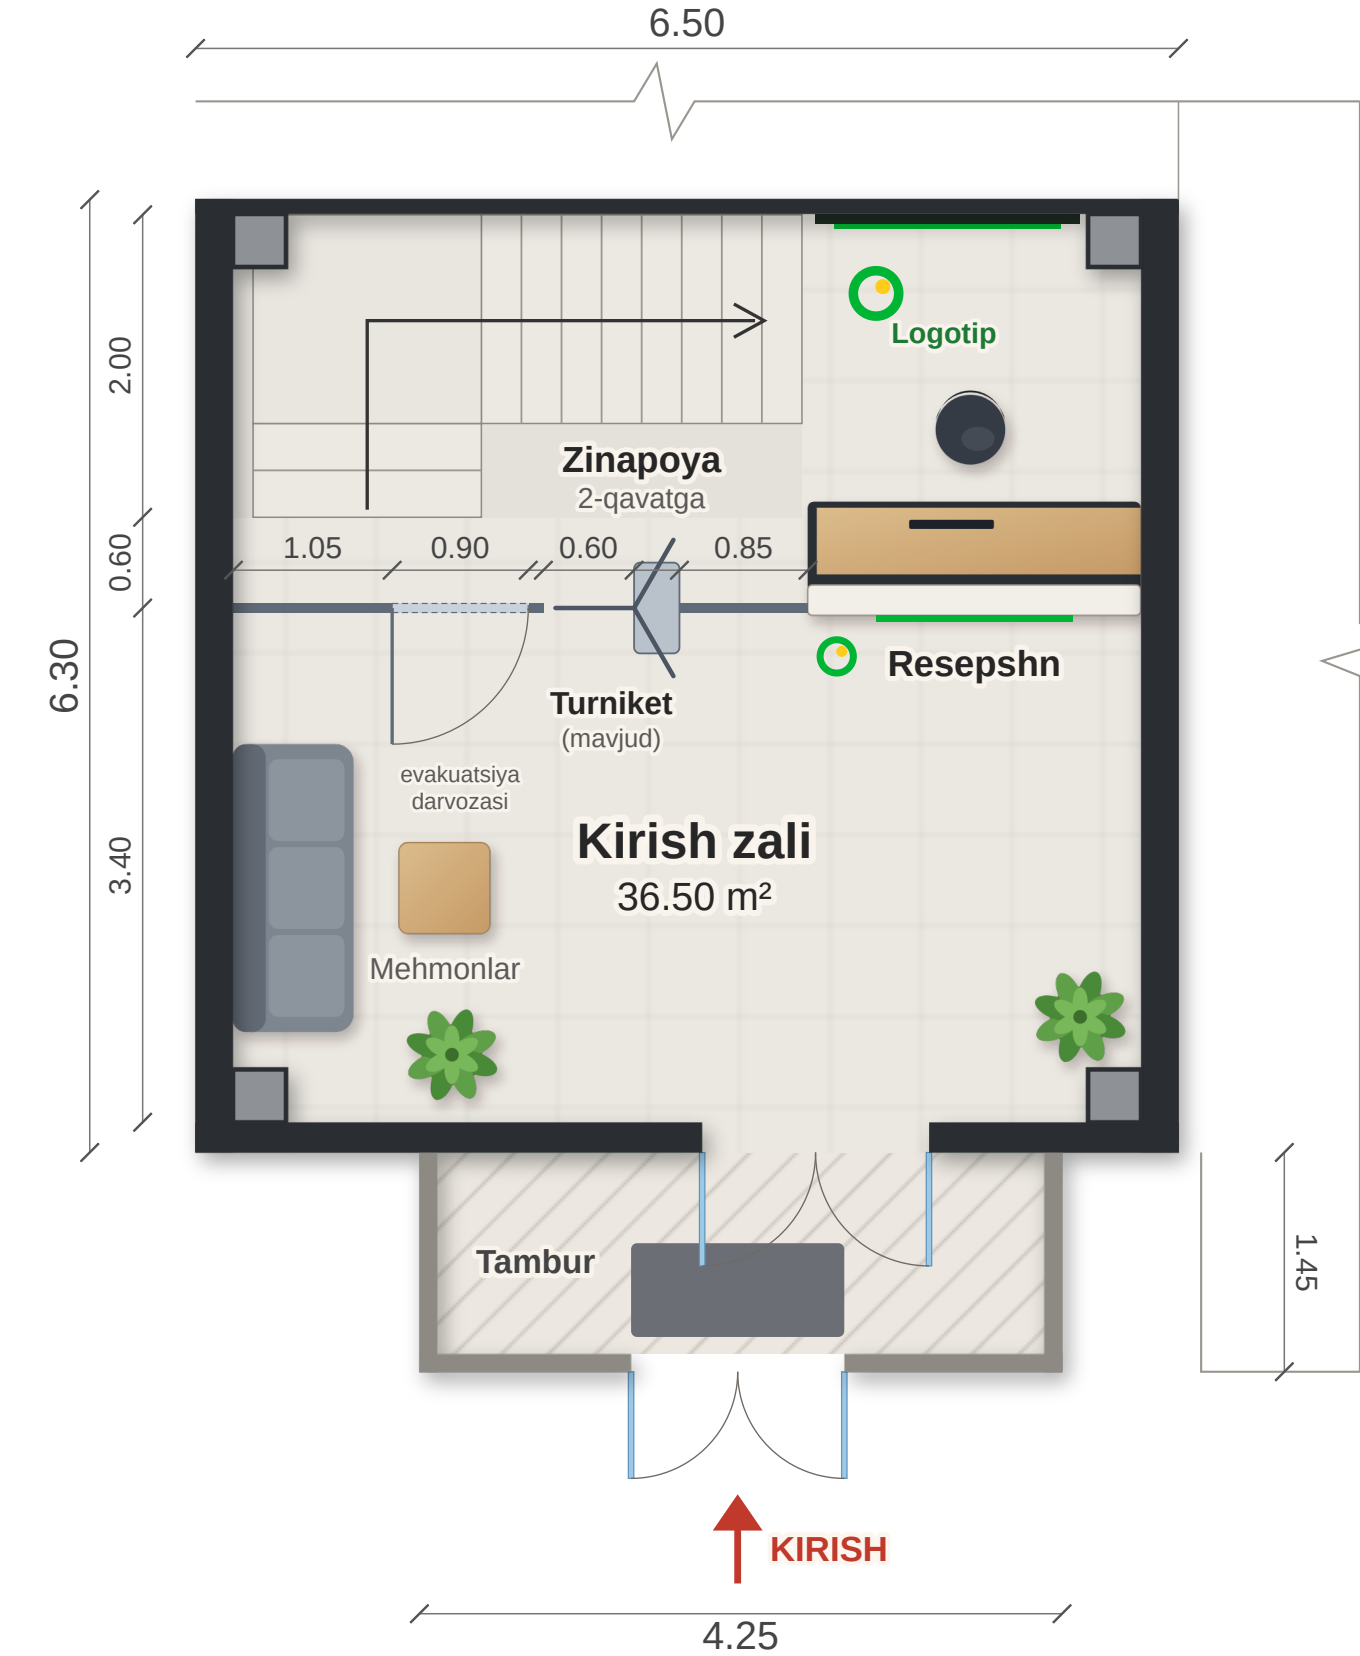

Yechim

- **Turniket chizig'i** zalni ikkiga bo'ladi: janubda kirish va mehmonlar zonasi, shimolda zina (2-qavatga). Eshikdan turniketgacha 3.40 m, turniketdan zina boshigacha 0.60 m.
- **Turniket** — buyurtmachida mavjud (tripod). O'tish yo'lagi 60 sm. Yonida **evakuatsiya darvozasi** 90 sm (antipanika: yong'in signalida ochiladi, resepshtndan ochib beriladi — sumka, aravacha, nogironlar aravasi uchun), qolgan qismi to'siq bilan yopiladi.
- **Resepshtn stoykasi** turniket chizig'ining o'ng qismida, eshikka qaragan: xodim kirgan har bir kishini ko'radi va turniketni boshqaradi. Uzunligi 2.20 m, mijoz tomonida 1.10 m lik peshtaxta, xodim tomonida 0.75 m ish yuzasi.
- **Logotiplar** (design.pdp.uz, PDP Academy asosiy logotipi): stoyka orqasidagi devorda ichidan yoritilgan katta logotip (~1.50 × 0.44 m, to'q panelda) — eshikdan kirganda ro'parada ko'rinadi; stoykaning old panelida ikkinchi logotip (~1.00 m, yoritilgan).
- **Mehmonlar zonasi**: chap devor bo'ylab 3 o'rinni divan va jurnal stolchasi (ota-onalar, kutayotganlar).

Ko'rsatkich	Qiymat
Zal (tashqi / ichki)	6.50 × 6.30 m / 6.00 × 6.00 m · 36.50 m²
Tambur	4.25 × 1.45 m, ikki tavaqali eshiklar
Turniket yo'lagi / evakuatsiya darvozasi	600 / 900 mm
Resepshtn stoykasi	2.20 × 0.70 m, h 1.10 / 0.75 m
Logotiplar	2 ta: devorda (yoritilgan) va stoykada
Avtomatik tekshiruv (to'qnashuv, eshik, zina)	xato yo'q

Tasdiqlash uchun

- Turniket nechta va qanday turda (tripod / tumba)? To'siq va evakuatsiya darvozasi uning komplektida bormi — bo'lmasa, alohida olinadi.
- Tambur (chizmada shtrixlangan) — mavjudmi yoki quriladimi?
- Zal shifti balandligi va yoritish (hisobda 3.5 m) — joyida aniqlanadi.

O'lchamlar buyurtmachi yuborgan 1-qavat chizmasi fotosidan; ustunlar, devor qalinliklari va zina chegarasi taxminiy — joyida o'lchanadi. Zina 2-qavatdagi kirish zinasiga (ZN2) olib chiqadi.