



3-qavat rejasi — o'quv xonasi (24 o'rin) va erkaklar hojatxonasi

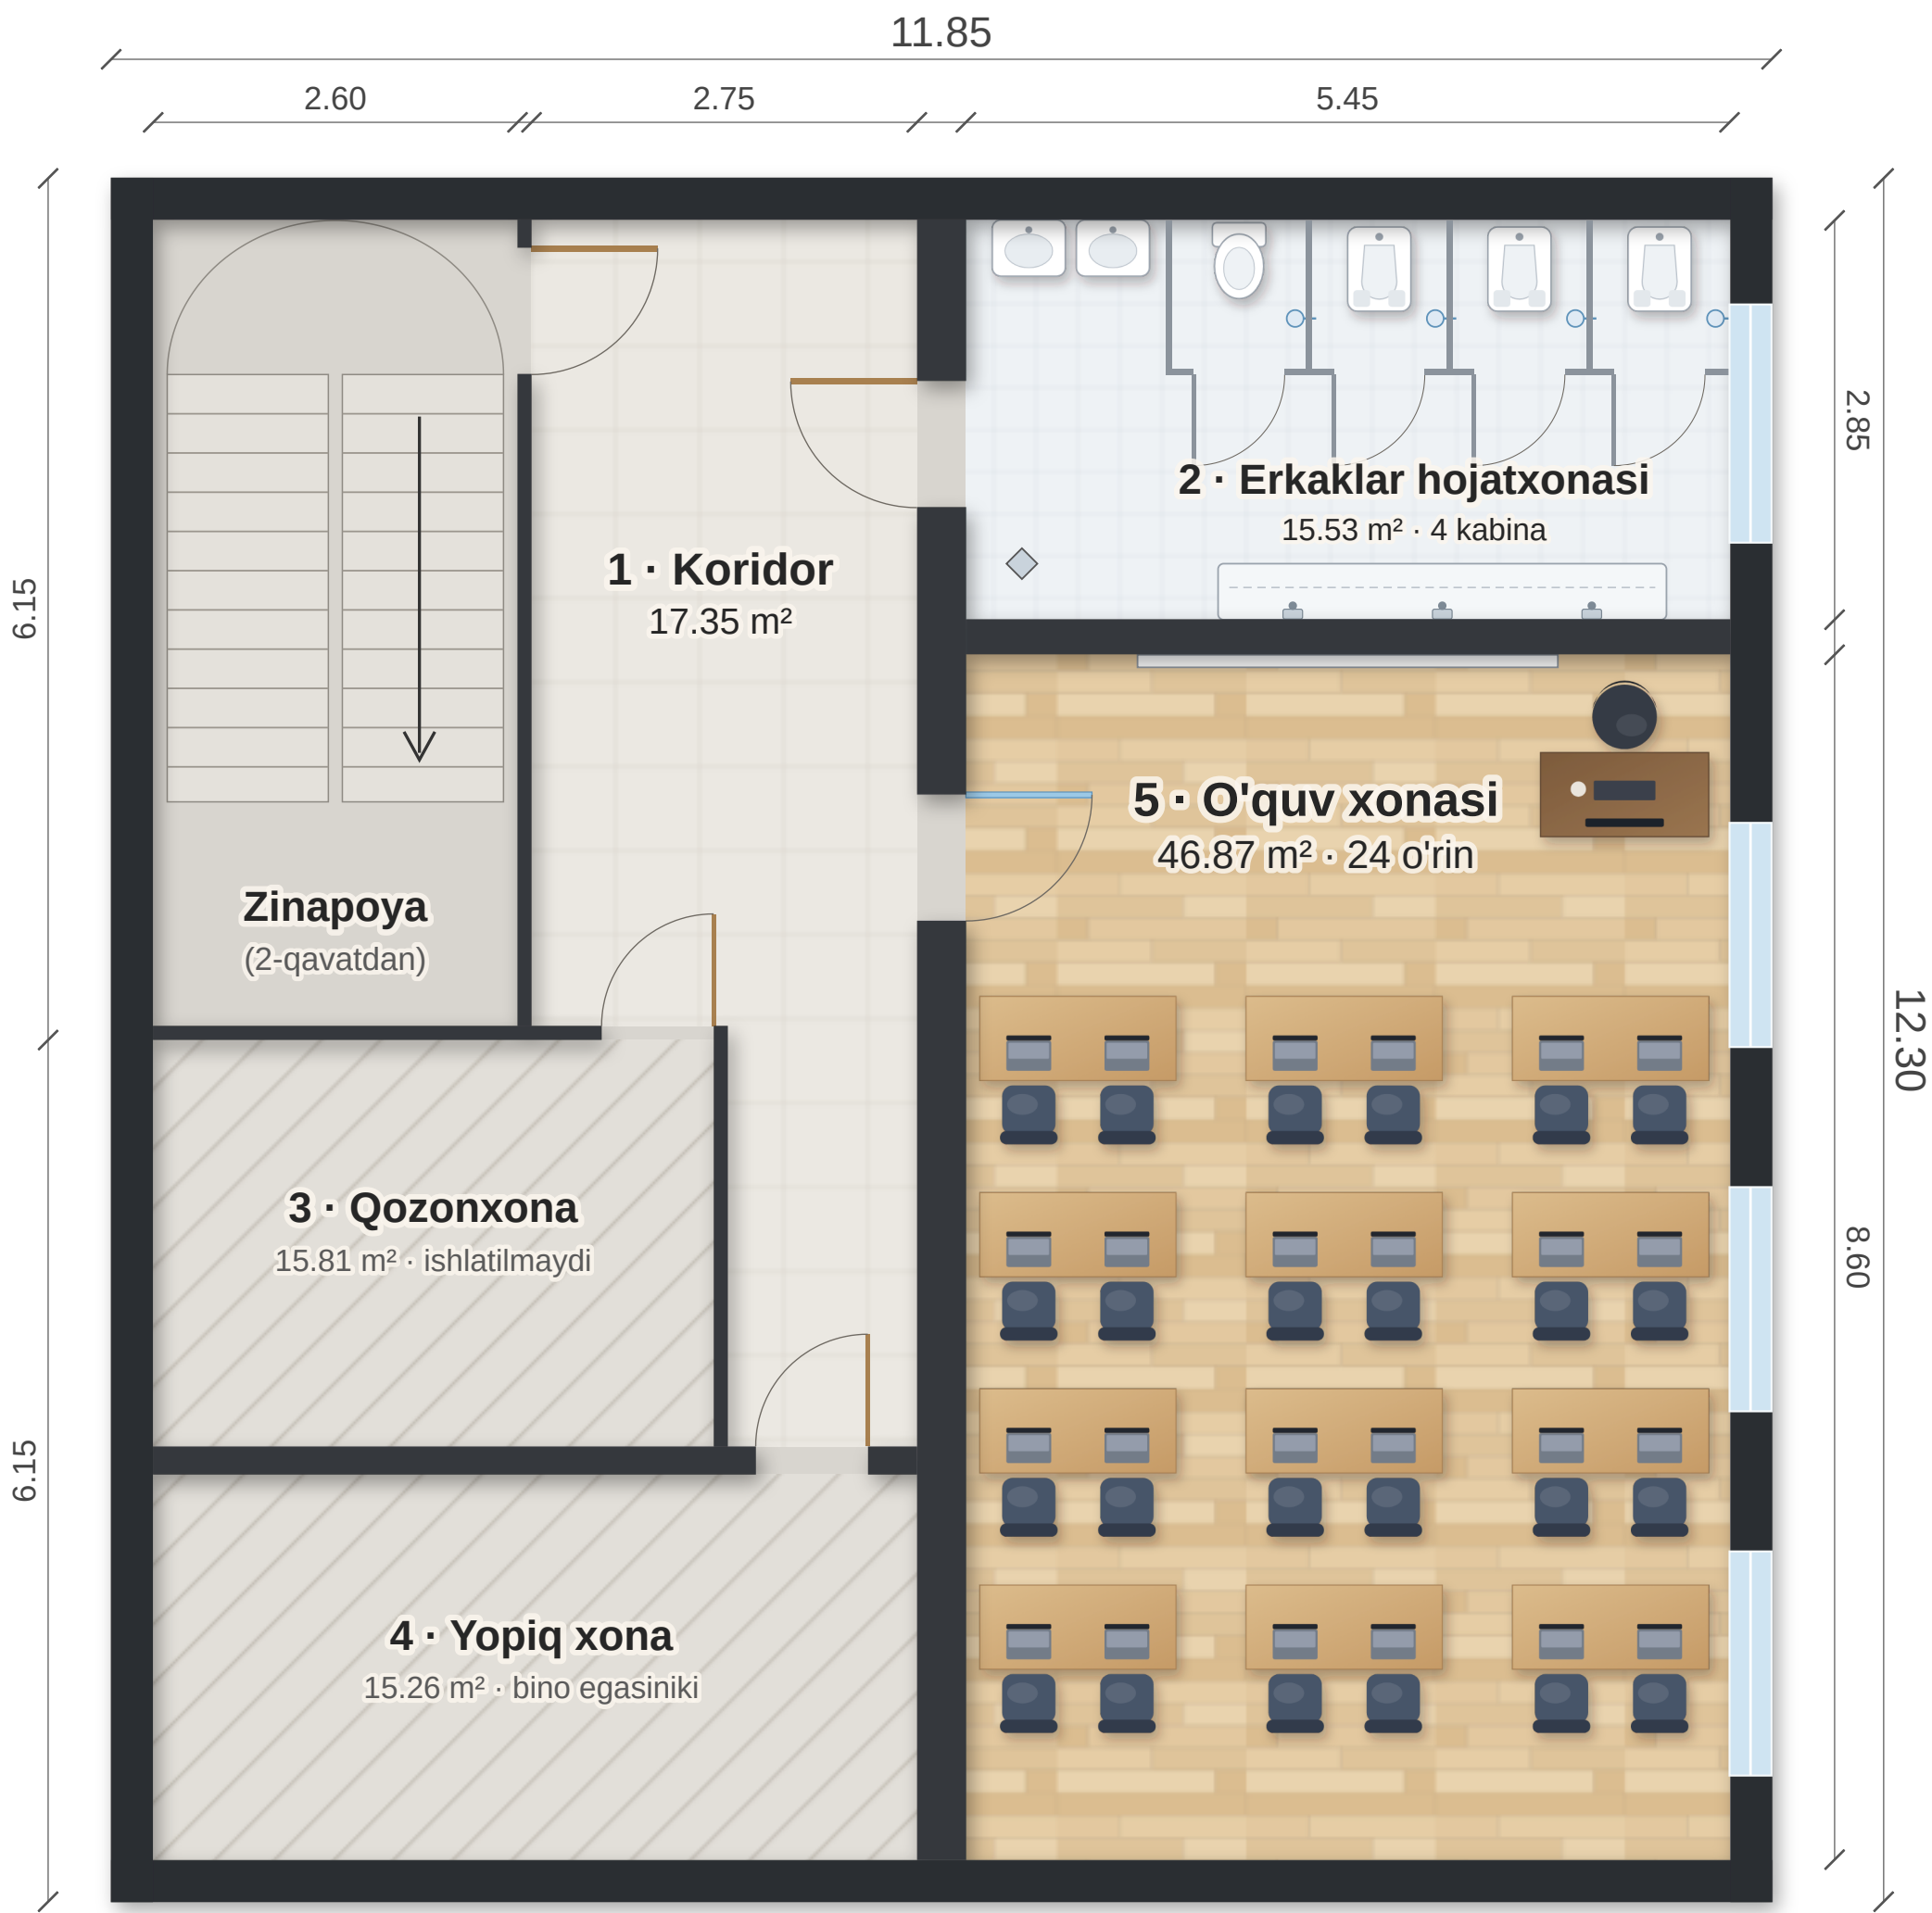

2-xona — erkaklar hojatxonasi (buyurtmachi chizgan ko'rinishda)

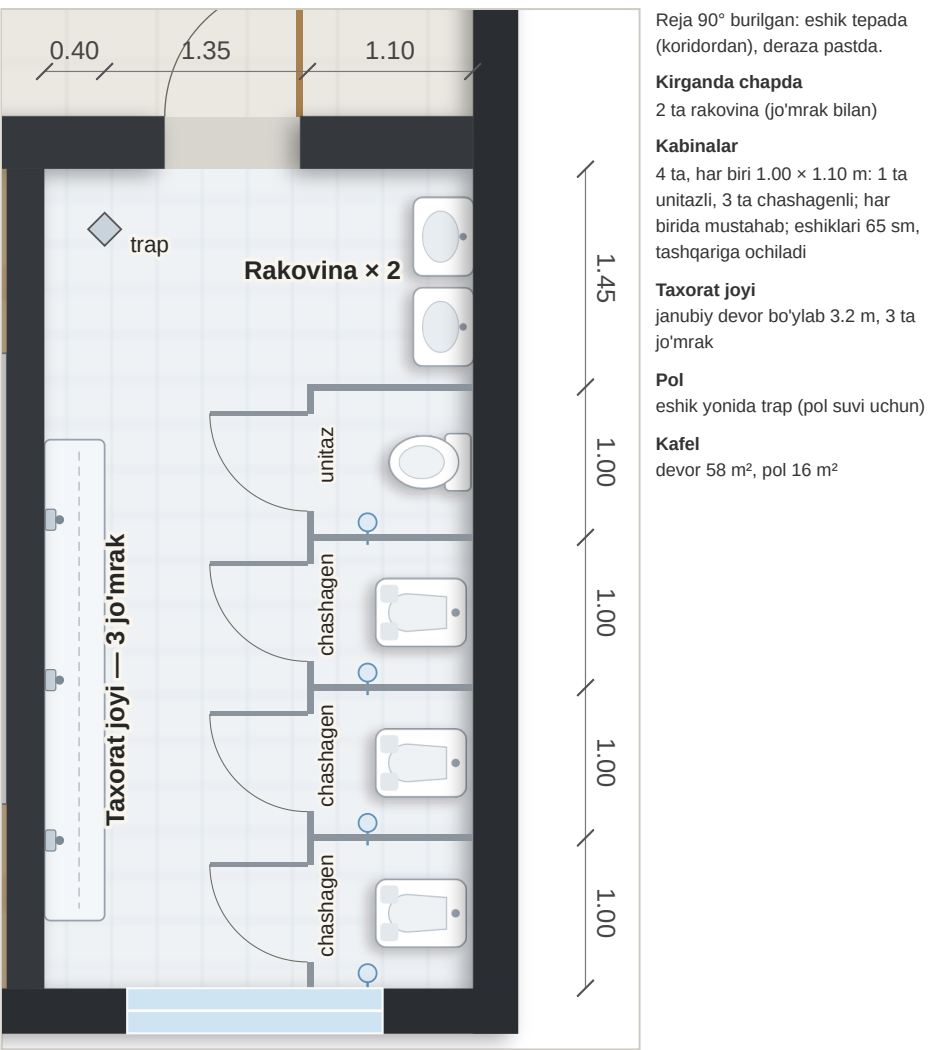

Xona	Vazifasi	m²
1	Koridor (zinapoyadan)	17.35
2	Erkaklar hojatxonasi	15.53
3	Qozonxona — ishlatilmaydi	15.81
4	Yopiq xona — bino egasini	15.26
5	O'quv xonasi, 24 o'rin	46.87
Umumiy / foydali maydon		118 / 110.82
5-xona: o'quv xonasi		
Partalar	12 ta ikki kishilik, 140 × 60 sm — 4 qator × 3 interaktiv, shimoliy devorda (kirganda chapda)	
Doska		
Doska → 1-parta / qator qadami	2.44 m / 1.40 m	
Yo'lak / devorgacha	50 sm / 10–15 sm	
Oxirgi parta (doskadan) / orqa devorgacha	7.24 m / 1.36 m	
Chetki o'rindan qarash burchagi	39.2° (Beruniy — 39.8°)	
Bambuk panel	3 devor, 2.5 m balandlikda	

O'chamlar 3-qavat chizmasi fotosidan olingan (11.85 × 12.30 m); derazalar joyi taxminiy — joyida o'chanadi. 2-qavatdagi WC — ayollar hojatxonasi (2 unitaz, 1 chashagen). Hojatxona ventilyatsiyasi (chiqarish) va suv/kanalizatsiya yo'li santexnik bilan aniqlanadi.