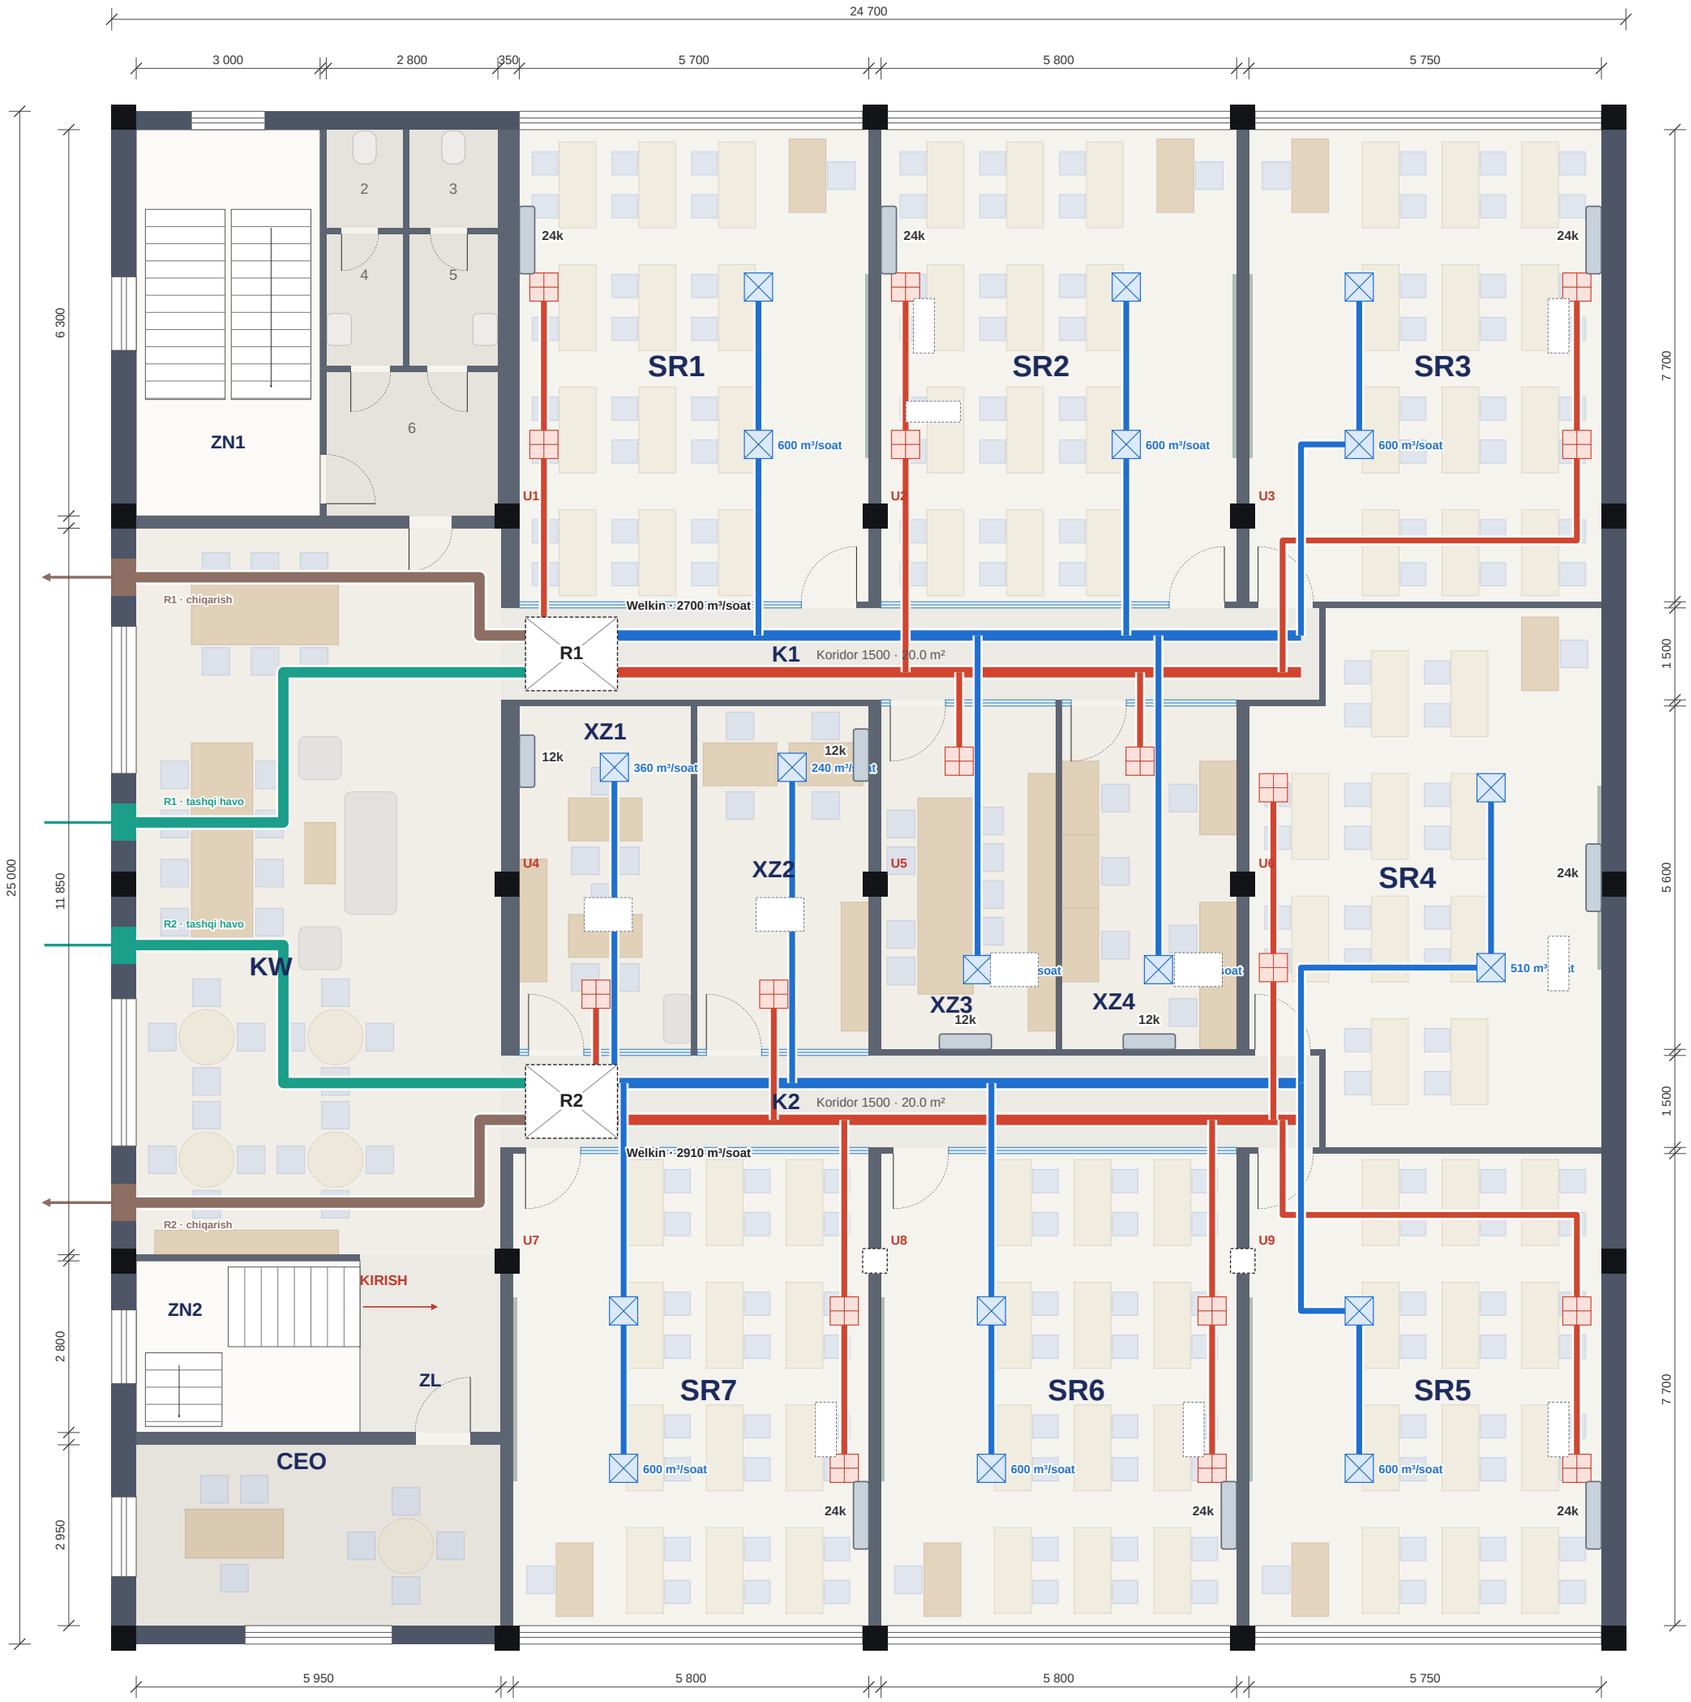



## VENTILYATSIYA — 2 TA REKUPERATOR (WELKIN)

| Qurilma | Xonalar | Loyiha, m³/soat | Me'yoriy min | Kanal |
|---|---|---|---|---|
| **R1** · K1 | SR1, SR2, SR3, XZ3, XZ4 | 2 700 | 2 537 | 600×300 |
| **R2** · K2 | SR4, SR5, SR6, SR7, XZ1, XZ2 | 2 910 | 2 717 | 600×300 |
| **Jami** | **havo kanallari ~223 m** | **5 610** | **5 253** | |

## XONALAR: TASHQI HAVO VA SPLIT (BUYURTMACHI TANLOVI)

| Xona | Odam | Havo, m³/soat | Rek. | CO₂, ppm | Yuk, kW | Split |
|---|---|---|---|---|---|---|
| SR1 | 25 | 600 | R1 | 1 170 | 7.5–8.1 | **24k ✗** |
| SR2 | 25 | 600 | R1 | 1 170 | 7.6–9.3 | **24k ✗** |
| SR3 | 25 | 600 | R1 | 1 170 | 7.6–9.3 | **24k ✗** |
| SR4 | 21 | 510 | R2 | 1 161 | 4.2–5.5 | **24k ✓** |
| SR5 | 25 | 600 | R2 | 1 170 | 8.0–9.4 | **24k ✗** |
| SR6 | 25 | 600 | R2 | 1 170 | 7.9–9.4 | **24k ✗** |
| SR7 | 25 | 600 | R2 | 1 170 | 7.9–9.4 | **24k ✗** |
| XZ1 | 6 | 360 | R2 | 720 | 1.9–2.3 | **12k ✓** |
| XZ2 | 4 | 240 | R2 | 720 | 1.4–1.8 | **12k ✓** |
| XZ3 | 9 | 540 | R1 | 720 | 2.3–2.7 | **12k ✓** |
| XZ4 | 6 | 360 | R1 | 720 | 2.5–2.9 | **12k ✓** |
| KW | 35/70 | — | — | | 6.5–15.1 | mavjud 24k + 18k |
| CEO | 7 | — | — | | | mavjud |

## HISOB ASOSI

**Tashqi havo:** sinflarda 24 m³/soat·kishi (me'yoriy ~22), derazasiz xizmat xonalarida 60 m³/soat·kishi (KMK). R2 ga 2 910 m³/soat kerak — **3000 m³/soatlik model** (kanal qarshiligi ~300 Pa da).

**Split:** yuk — odamlar (115 W/kishi), yoritish, panel/kompyuter, oynali fasad (quyosh: sharq — 9:00, g'arb — 16:00; steklopaket + reklama plyonkasi), devor, tom va rekuperatordan keyingi tashqi havo qoldig'i. ✓ — yetarli; ≈ — chegarada; ✗ — eng og'ir paytda kam (oynali sinflar: tavsiyalar — konditsionerlar chizmasi, 2-varaq). Ichki blok — orqa yon devorda, oynaga yaqin; tashqi bloklar — tomda (punktir). Koworkingdagi mavjud konditsionerlar koridorlarni ham sovutadi.

Toza havo doska oldida beriladi, orqa devor yonida so'riladi. Kanallar koridorlar osma shifti ichida (~2.8 m), koworkingda — shift ostida (fasadgacha). Kanallar yo'nalishi — taklif, buyurtmachi o'zgartirishi mumkin.

**MASSHTAB 1:100**

0 1 2 3 4 5 m

## SHARTLI BELGILAR

- R1, R2 — Welkin rekuperatori (koridor shiftida)
- so'rish kanali (xonalardan rekuperatorga)
- chiqarish kanali (fasadga)
- so'rish panjarasi
- split — tashqi blok (tomda, punktir)
- toza havo kanali (rekuperatordan xonalarga)
- tashqi havo kanali (fasaddan)
- toza havo diffuzori
- split — ichki blok (devorda), yozuv: BTU/soat

| | | | |
|---|---|---|---|
| **PDP Academy · Xadra filiali** | | | |
| Chizma | **Ventilyatsiya va konditsionerlash** | | |
| Manba: mavjud holat chizmasi (foto), 2-qavat · umumiy 617 m², foydali 557,74 m² | | | |
| Toshkent sh., Xadra — 2-qavat | | | |
| Masshtab **1:100** | Sana **09.10.2026** | Versiya **v1.2** | Varaq **3 / 4** |
| Bajardi | | | |
| Tekshirdi / tasdiqladi — direktor | | | |