
PDP Academy · Xadra filiali

3-qavat rejasi — o'quv xonasi (24 o'rin) va erkaklar hojatxonasi

Masshtab 1:50 (A3) · v1.2 · 09.10.2026

0 1 2 3 4 5 m (1:50)

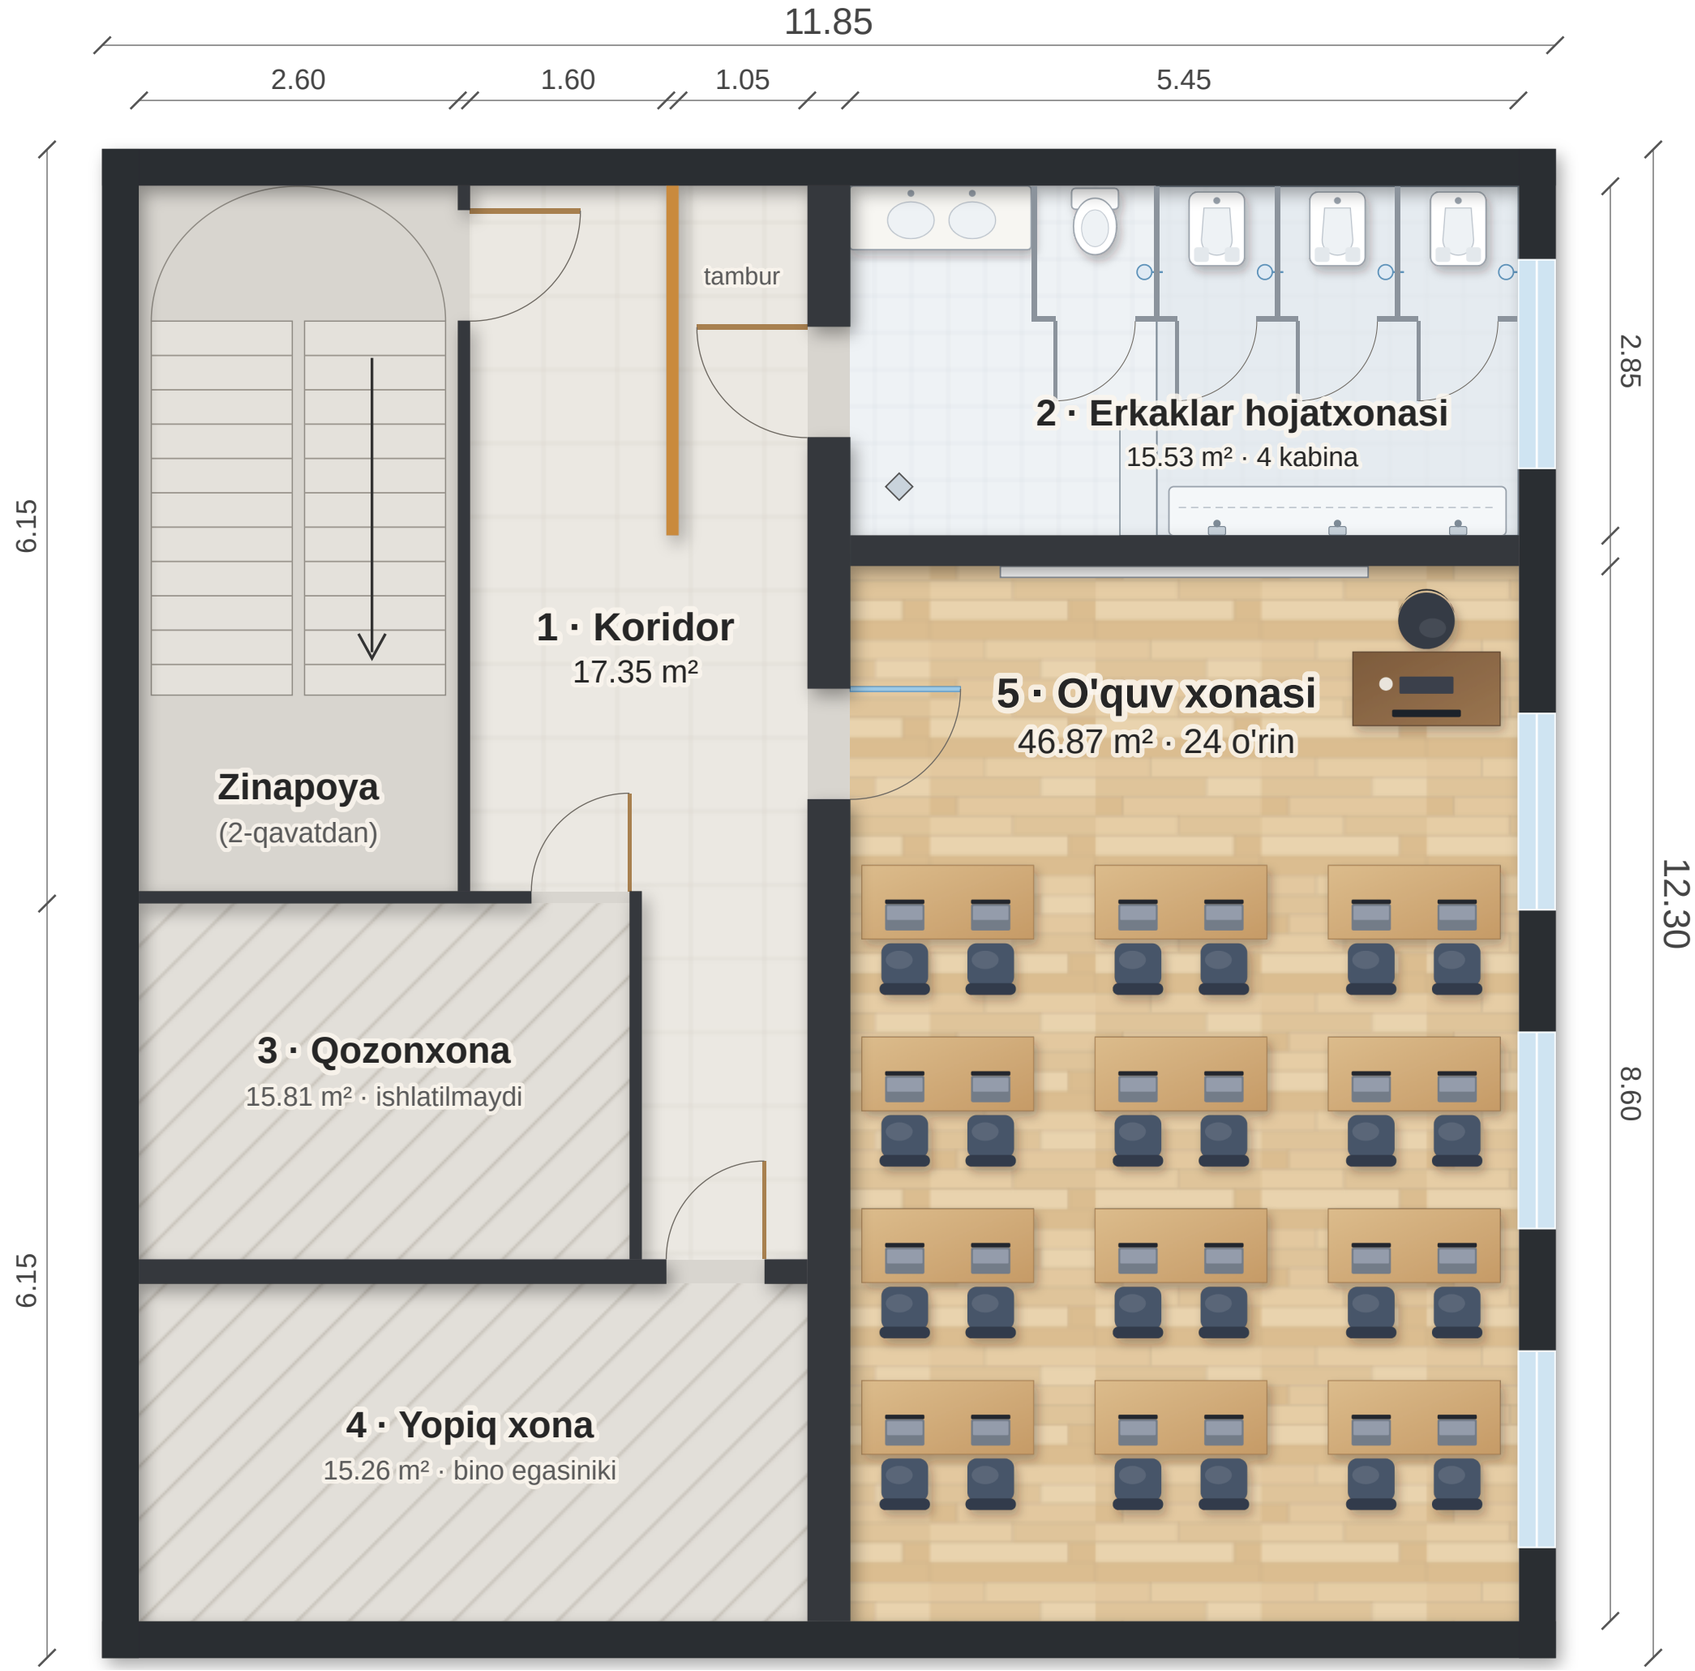

2-xona — erkaklar hojatxonasi (buyurtmachi chizgan ko'rinishda)



Reja 90° burilgan: eshik tepada (koridordan), deraza pastda.

Kirganda chapda
quyma rakovina 1.50 m (2 ta chanoq, jo'mrak bilan)

Kabinalar
4 ta, chuqurligi 1.10 m: 1 ta unitazli (1.00 m, pastki polda), 3 ta chashagenli (~0.98 m, supada); har birida mustahab; eshiklari 65 sm

Supa
eshikdan 2.50 m dan keyin pol 30 sm ko'tarilgan (usti kafel), pog'ona 15 sm; supada taxorat joyi — janubiy devor bo'ylab 2.75 m, 3 ta jo'mrak

Pol
kafel; eshik yonida trap

Devorlar
plastik (PVX) marmar panel — 3 variant (3D)

Xona	Vazifasi	m²
1	Koridor (zinapoyadan)	17.35
2	Erkaklar hojatxonasi	15.53
3	Qozonxona — ishlatilmaydi	15.81
4	Yopiq xona — bino egasiniki	15.26
5	O'quv xonasi, 24 o'rin	46.87
Umumiy / foydali maydon		**118 / 110.82**

5-xona: o'quv xonasi	
Partalar	12 ta ikki kishilik, 140 × 60 sm — 4 qator × 3
Doska	interaktiv, shimoliy devorda (kirganda chapda)
Doska → 1-parta / qator qadami	2.44 m / 1.40 m
Yo'lak / devorgacha	50 sm / 10–15 sm
Oxirgi parta (doskadan) / orqa devorgacha	7.24 m / 1.36 m
Chetki o'rindan qarash burchagi	39.2° (Beruniy — 39.8°)
Bambuk panel	3 devor, 2.5 m balandlikda

O'lchamlar 3-qavat chizmasi fotosidan olingan (11.85 × 12.30 m); derazalar joyi taxminiy — joyida o'lchanadi. 2-qavatdagi WC — ayollar hojatxonasi (2 kabina, unitazli, tambur orqali). Hojatxona ventilyatsiyasi (chiqarish) va suv/kanalizatsiya yo'li santexnik bilan aniqlanadi.