
1-varaq · Internet (RJ-45) va Wi-Fi — 2-qavat, 1:100

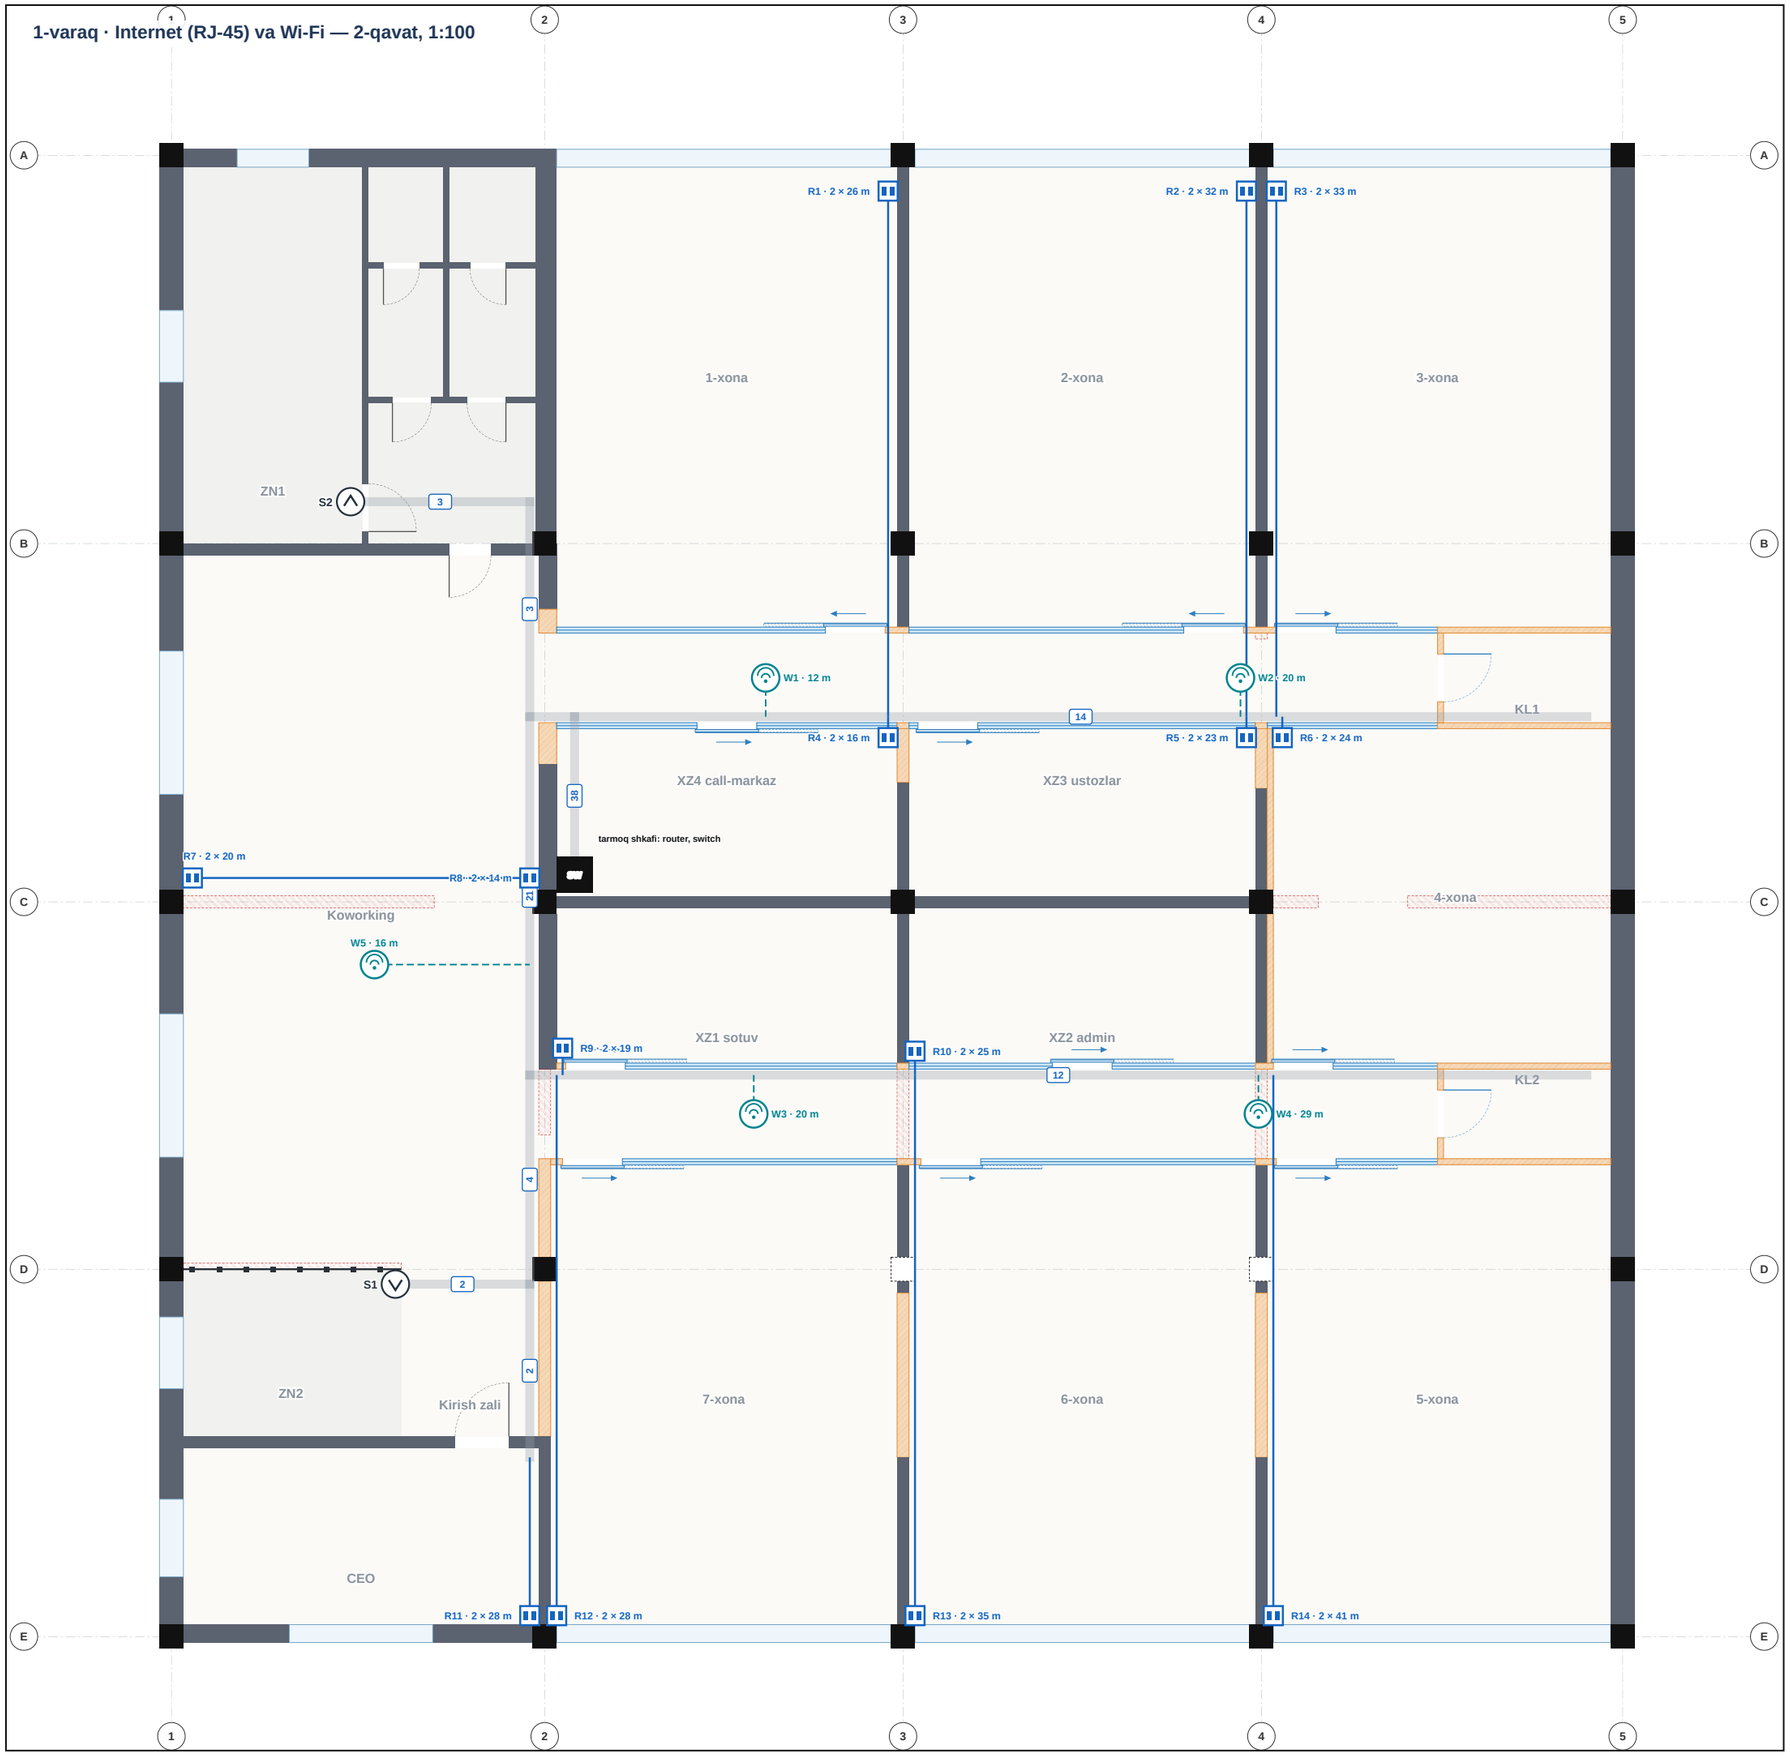

INTERNET — 16 ta RJ-45 (2 portli), 6 ta Wi-Fi nuqtasi

- RJ-45 rozetka, 2 portli, poldan 30 sm
- 2 × Cat6 (har rozetkaga)
- past tokli lotok; raqam — kabellar soni
- Wi-Fi nuqtasi (shiftda, PoE)
- Cat6 Wi-Fi nuqtasiga
- tarmoq shkafi (XZ4)

2-qavat — 14 ta rozetka, 5 ta Wi-Fi

Kod	Joy	Xona	Cat6, m
R1	RJ-45 × 2 — doska devori, deraza cheti	1-xona	2 × 26
R2	RJ-45 × 2 — doska devori, deraza cheti	2-xona	2 × 32
R3	RJ-45 × 2 — doska devori, deraza cheti	3-xona	2 × 33
R4	RJ-45 × 2 — shimoli-sharqiy burchak	XZ4 call-markaz	2 × 16
R5	RJ-45 × 2 — shimoli-sharqiy burchak	XZ3 ustozlar	2 × 23
R6	RJ-45 × 2 — doska devori, shimoliy cheti	4-xona	2 × 24
R7	RJ-45 × 2 — g'arbiy devor o'rtasida	Koworking	2 × 20
R8	RJ-45 × 2 — sahna devori (ekran ostida)	Koworking	2 × 14
R9	RJ-45 × 2 — janubi-g'arbiy burchak	XZ1 sotuv	2 × 19
R10	RJ-45 × 2 — janubi-g'arbiy burchak	XZ2 admin	2 × 25
R11	RJ-45 × 2 — janubi-sharqiy burchak	CEO	2 × 28
R12	RJ-45 × 2 — doska devori, deraza cheti	7-xona	2 × 28
R13	RJ-45 × 2 — doska devori, deraza cheti	6-xona	2 × 35
R14	RJ-45 × 2 — doska devori, deraza cheti	5-xona	2 × 41
W1	Wi-Fi nuqtasi (PoE) — koridor shifti	K1	12
W2	Wi-Fi nuqtasi (PoE) — koridor shifti	K1	20
W3	Wi-Fi nuqtasi (PoE) — koridor shifti	K2	20
W4	Wi-Fi nuqtasi (PoE) — koridor shifti	K2	29
W5	Wi-Fi nuqtasi (PoE) — koworking markazi	Koworking	16

Uzunlik: rozetkadan lotokkacha, lotok bo'ylab shkafgacha × 1.1 + rozetkaga 3.0 m tushish (devorda, gofra quvurda), shkafda 2.3 m + zaxira 2 m. Rozetkaga 2 ta kabel (2 port). Lotokdagi raqam — kabellar soni.

- Kabel — Cat6 U/UTP LSZH; har port alohida kabel bilan shkafdagi patch-panelga (≤ 90 m), uchlari belgilanadi (R1-1, R1-2 …).
- Wi-Fi nuqtalari shiftda, PoE orqali; koridorda — lotok yonida, koworkingda — markazda.

PDP Academy · Xadra filiali


Chizma	**Internet va Wi-Fi — 2-qavat**

Ish chizmasi — ustalar uchun. Qurilmalar joyi — buyurtmachi belgilagan (18.10). Toshkent sh., Xadra — 2-qavat


Masshtab	Sana	Versiya	Varaq
1:100	18.10.2026	v1.2	1 / 2

Bajardi: _____ Tekshirdi: _____


3-QAVAT

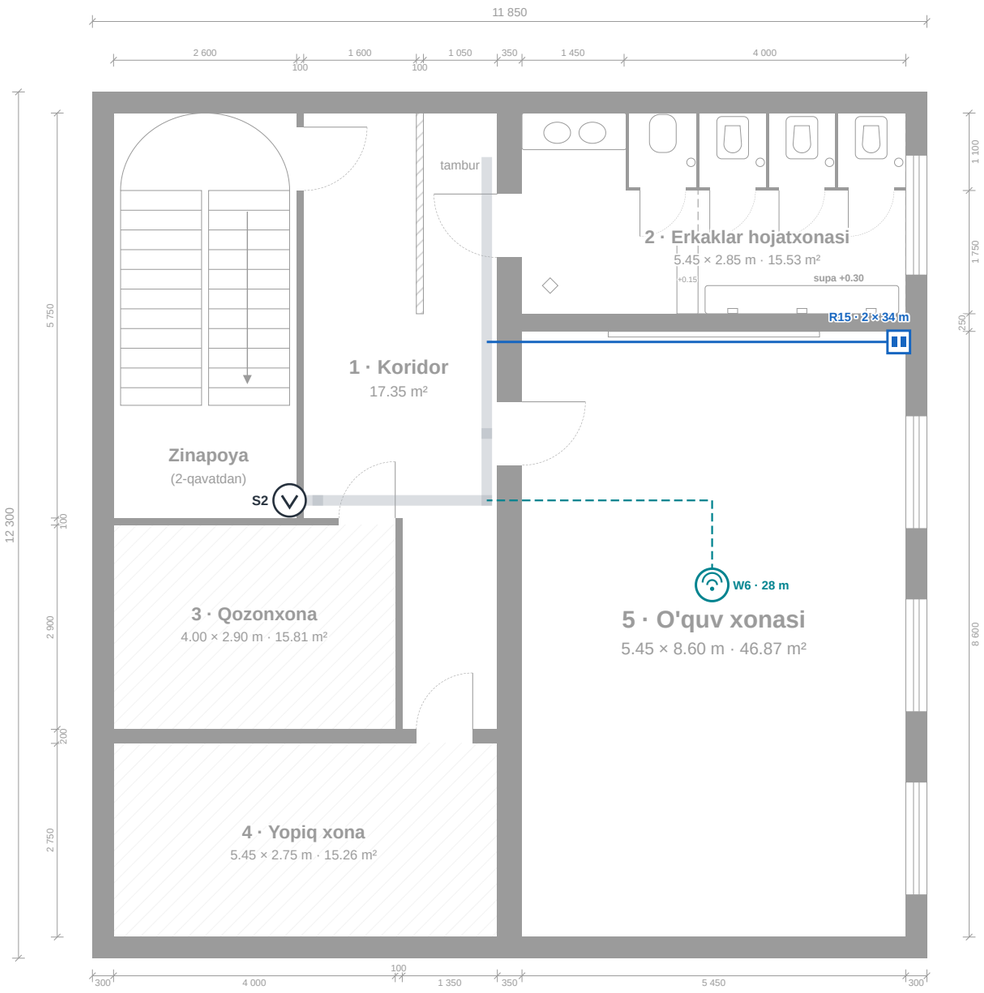

1-QAVAT (kirish zali)

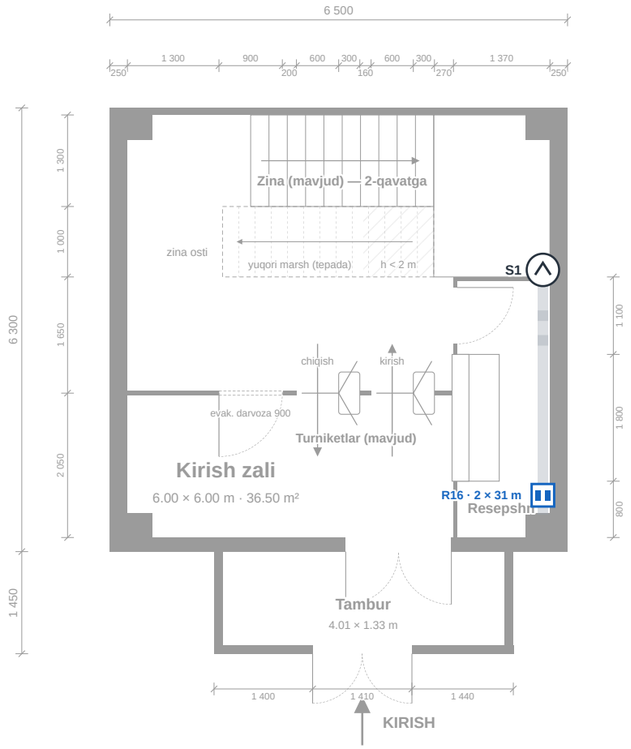

TUZILMA SXEMASI

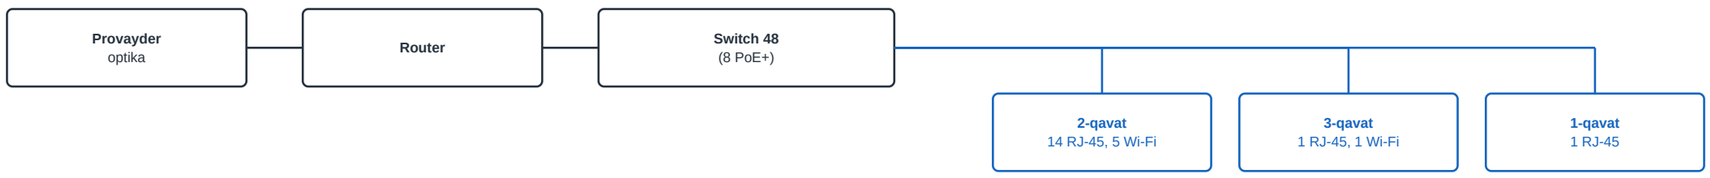

INTERNET — 3- VA 1-QAVAT, SHKAF

- RJ-45 rozetka, 2 portli, poldan 30 sm
- 2 × Cat6 (har rozetkaga)
- past tokli lotok; raqam — kabellar soni
- Wi-Fi nuqtasi (shiftda, PoE)
- Cat6 Wi-Fi nuqtasiga
- tarmoq shkafi (XZ4)

3-qavat va 1-qavat

Kod	Joy	Xona	Cat6, m
R15	RJ-45 × 2 — doska devori, deraza cheti	3-q. 5-xona (o'quv)	2 × 34
R16	RJ-45 × 2 — resepshn stoykasi ortida	1-q. zal	2 × 31
W6	Wi-Fi nuqtasi (PoE) — o'quv xonasi o'rtasi	3-q. 5-xona (o'quv)	28

Shkafdagi jihozlar (kamera bilan umumiy shkaf, XZ4)

Jihoz	Soni
Router (2 WAN, ≥ 1 Gbit/s)	1
Switch 48 port (8 tasi PoE+ — Wi-Fi uchun), gigabit	1
Patch-panel 24 port Cat6 (internet: 32 + 6 port)	2
Wi-Fi nuqtasi (shift, PoE, Wi-Fi 6, kontrollersiz/bulutli)	6
RJ-45 rozetka, 2 portli, Cat6 (ramka bilan)	16

Kabel

Nomi	m
Cat6 U/UTP LSZH — 32 port + 6 Wi-Fi	**983**

PDP Academy · Xadra filiali

Chizma	**Internet va Wi-Fi — 3- va 1-qavat**

Ish chizmasi — ustalar uchun. Qurilmalar joyi — buyurtmachi belgilagan (18.10). Toshkent sh., Xadra — 3- va 1-qavat

Masshtab	Sana	Versiya	Varaq
~1:90	18.10.2026	v1.2	2 / 2

Bajardi: _____ Tekshirdi: _____